



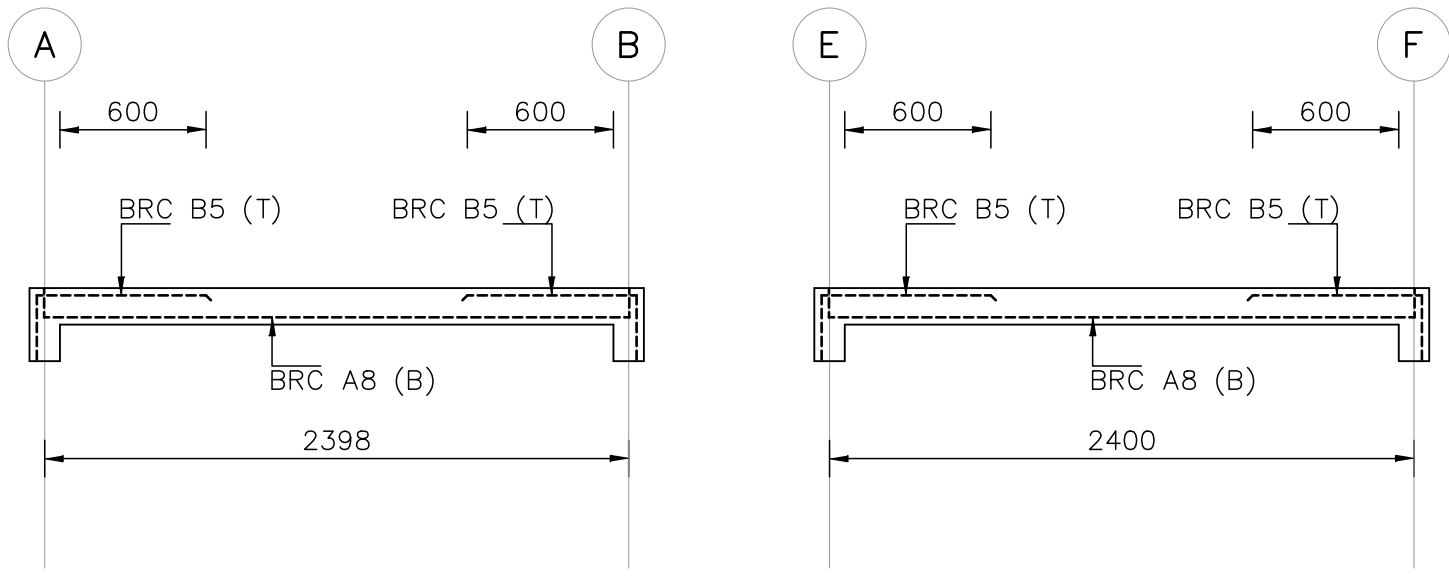

FS1 (150 thk.) Slab Cut Section No. 1 FS4 (150 thk.)

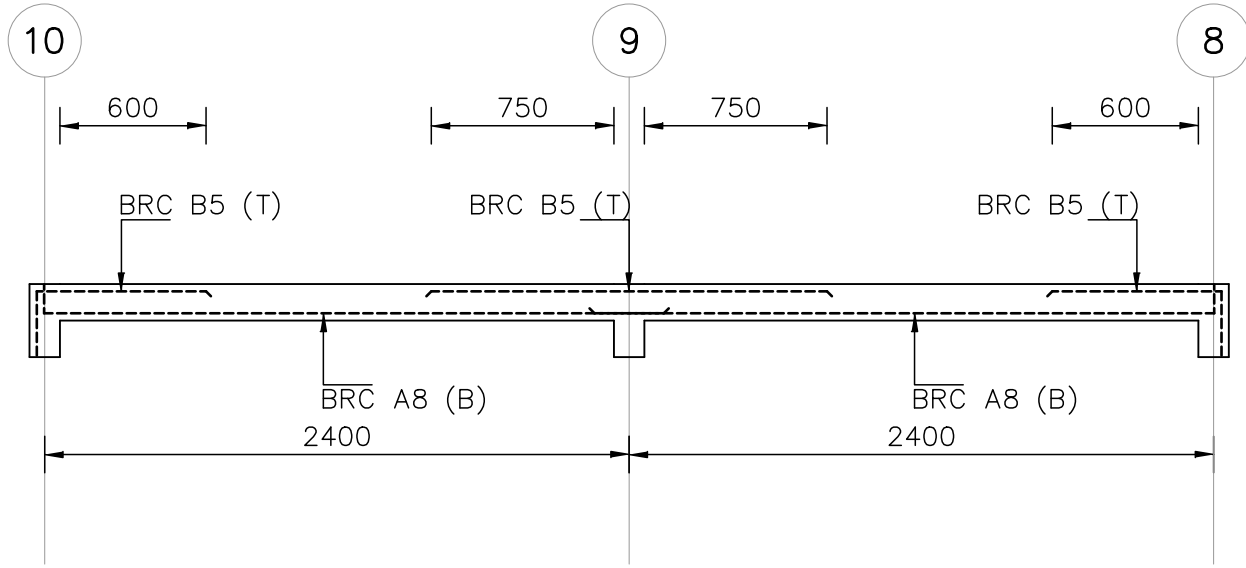

FS4 (150 thk.) FS3 (150 thk.) Slab Cut Section No. 2

NO. FAIL (KEGUNAAN PEJABAT)

COP KELULUSAN (KEGUNAAN PEJABAT)

BIL.	TARIKH	PINDAAN

TAJUK PERMOHONAN :

CADANGAN MEMBINA 1 UNIT SURAU 1 TINGKAT DIATAS LOT 20093, TAMAN JUASSEH SENTOSA, PEKAN JUASSEH, DAERAH KUALA PILAH, NEGERI SEMBILAN DARUL KHUSUS

UNTUK

TETUAN JABATAN HAL EHWAL AGAMA ISLAM NEGERI SEMBILAN

TAJUK LUKISAN :

SLAB DETAIL

ROOF SLAB SECTION 01

PEMILIK :

"Saya bersetuju bertanggung jawab sekiranya berlaku kerosakan kepada bangunan di lot sebelah-menyebelah akibat dari kerja-kerja dalam permohonan ini."

JABATAN HAL EHWAL AGAMA ISLAM KUALA PILAH NEGERI SEMBILAN

PEGAWAI AGAMA DAERAH : HARDI BIN MOHAMAD SADALI

NO. KP : 750908-10-5985

NO TEL : 06-4821029

EMAIL : paidkualapilah.jheains@nns.gov.my

ALAMAT : JHEAINS Kuala Pilah, 70200 Kuala Pilah Negeri Sembilan

JURUTERA PERUNDING :

JURUTERA BUDIMAN SENDIRIAN BERHAD

73B & 75B, Jalan SS 21/37, Damansara Utama, 47400 Petaling Jaya, Selangor Darul Ehsan, Tel: 03-7727 2515 Fax: 03-7727 7606 Email: juruterabudiman@gmail.com (Company No. 235335-P)

TANDATANGAN JURUTERA BERTAULIAH

I hereby certify that these works have been designed by me in accordance with sound engineering practice and that I take full responsibility for the design and proper performance of the same.

JURUTERA BUDIMAN SDN.BHD. (235335-P)

Pengarah

Scale	1:200 (A1)	Designed By	MIMA
Date	DECEMBER 2025	Checked By	Ir Shahrizal
Drawn By	SMK	Approved By	Ir Mohd Naspi

DRAWING NO:

SJ/1225/STRUC/SC/02/R00

SUBMISSION DRAWING