

NO FILE RUJUKAN :

UNTUK KEGUNAAN MBS

TAJUK PROJEK:

CADANGAN MEMBINA 1 UNIT SURAU 1 TINGKAT
DIATAS LOT 20093,
TAMAN JUASSEH SENTOSA,
PEKAN JUASSEH, DAERAH KUALA PILAH
NEGERI SEMBILAN DARUL KHUSUS
UNTUK
TETUAN JABATAN HAL EHWAL AGAMA ISLAM
NEGERI SEMBILAN

TANDATANGAN PEMILIK TANAH / BANGUNAN :

"Saya/Kami bersetuju untuk mematuhi pelan bangunan yang diluluskan. Dengan ini saya/kami bersetuju untuk dikenakan tindakan undang-undang yang berkaitan dengannya jika gagal mematuhiinya".

[Signature]

JABATAN HAL EHWAL AGAMA ISLAM
KUALA PILAH NEGERI SEMBILAN
PECAWAN AGAMA DAERAH : HARDI BIN MOHAMAD SADALI
NO. K/P : 750908-10-5965
NO TEL : 06-4821029
EMAIL : paldkualapilah.jheains@ns.gov.my
ALAMAT : JHEAINS Kuala Pilah, 70200 Kuala Pilah
Negeri Sembilan

ARKITEK:

"SAYA MEMPERAKUI BAHAWA BUTIRAN - BUTIRAN DI DALAM PELAN - PELAN INI ADALAH MENURUT KEHENDAK - KEHENDAK UNDANG - UNDANG KECIL BANGUNAN SERAGAM (PBTNS) 1986 DAN SAYA SETUJU TERIMA TANGGUNGJAWAB PENUH DENGAN SEWAJARNYA"



[Signature]
Ar. Wan Azami Bin Hamzah
ARKITEK PROFESIONAL
No Pendaftaran LAM: A/W 56



NO. 2 JALAN MERAH PELANGI SATU
U9/19a KELAB GOLF MONTEREZ
40150 SHAH ALAM, SELANGOR MALAYSIA
NO. TEL : 019 2063 100 / 012 324 0914
EMAIL : wah.architect@gmail.com


STATUS LUKISAN :

☐ PRELIMINARY ☒ SUBMISSION ☐ CONSTRUCTION
☐ INFORMATION ☐ TENDER ☐ DEVELOPMENT ORDER


TAJUK LUKISAN:

FENCING AND GATE


DILUKIS OLEH	JW
DISEMAK OLEH	WA
TARIKH	DEC 2025
SKALA	AS SHOWN
NO DWG.	SWS/BP/006

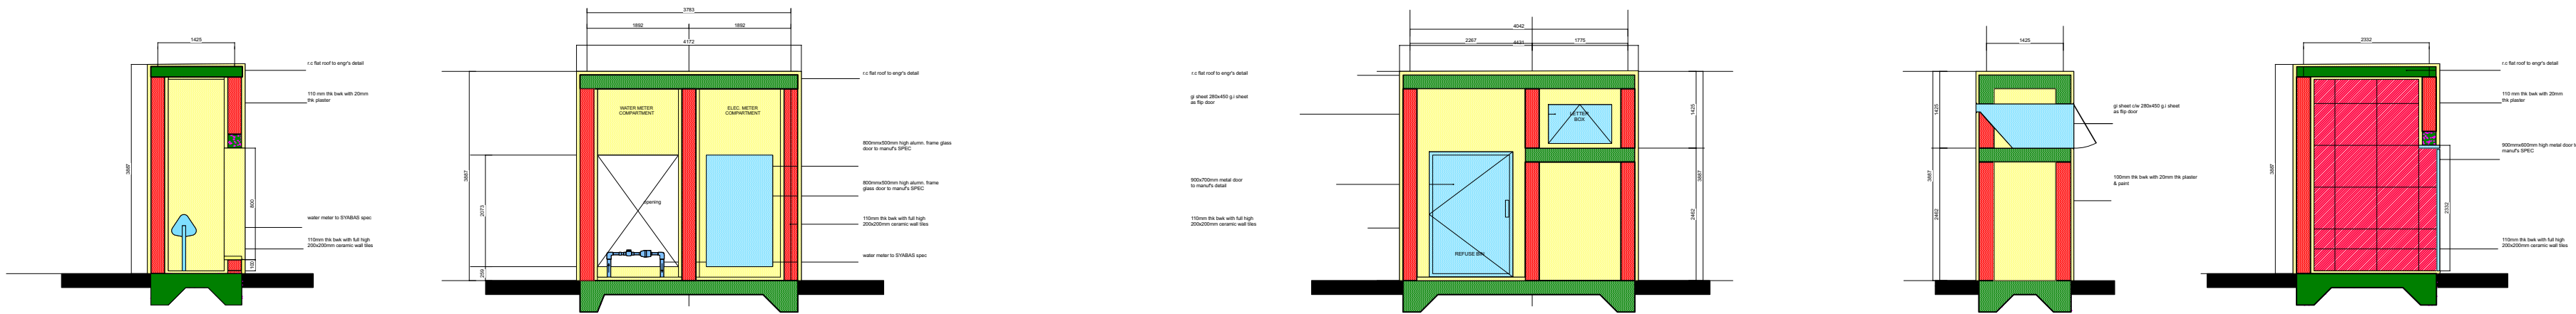


SECTIONAL DETAILS

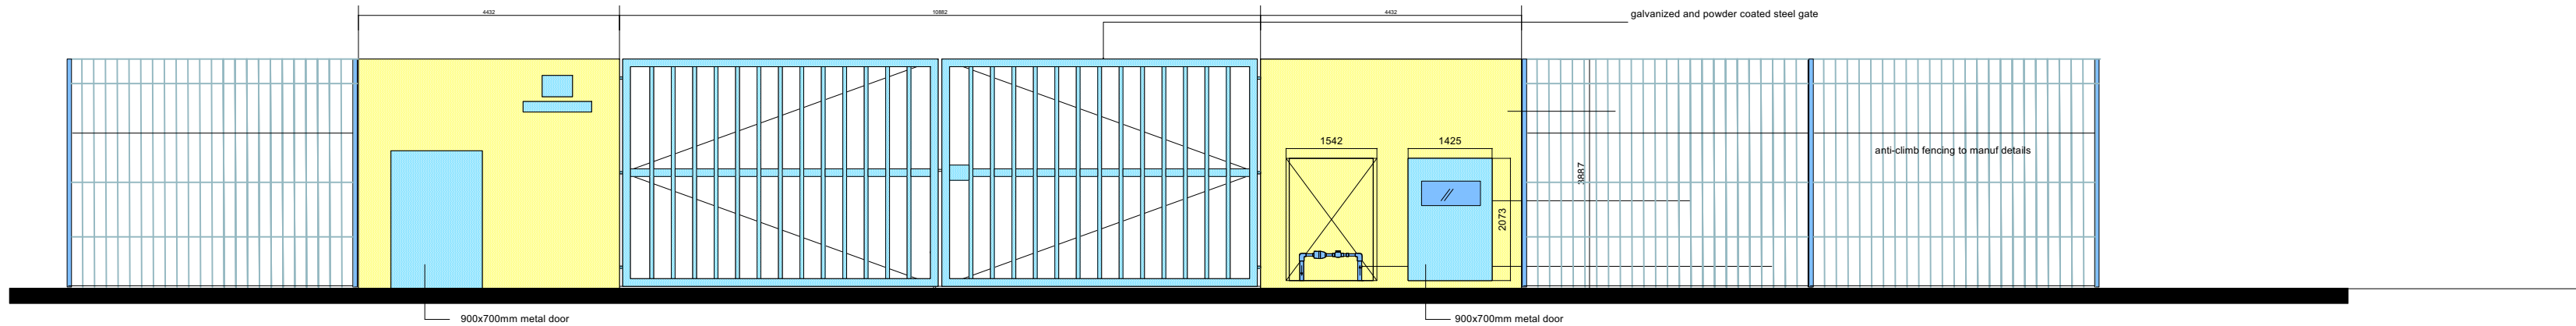

ELEVATION FROM ROAD OUTSIDE

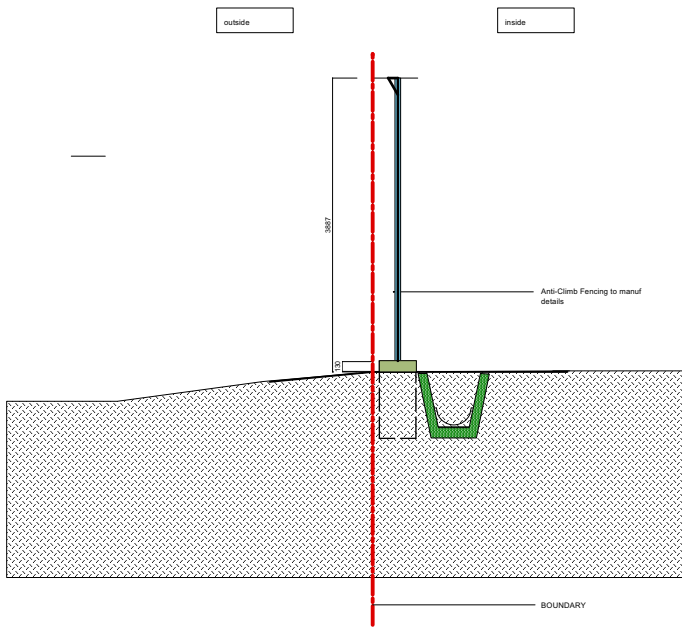

FENCING SECTION

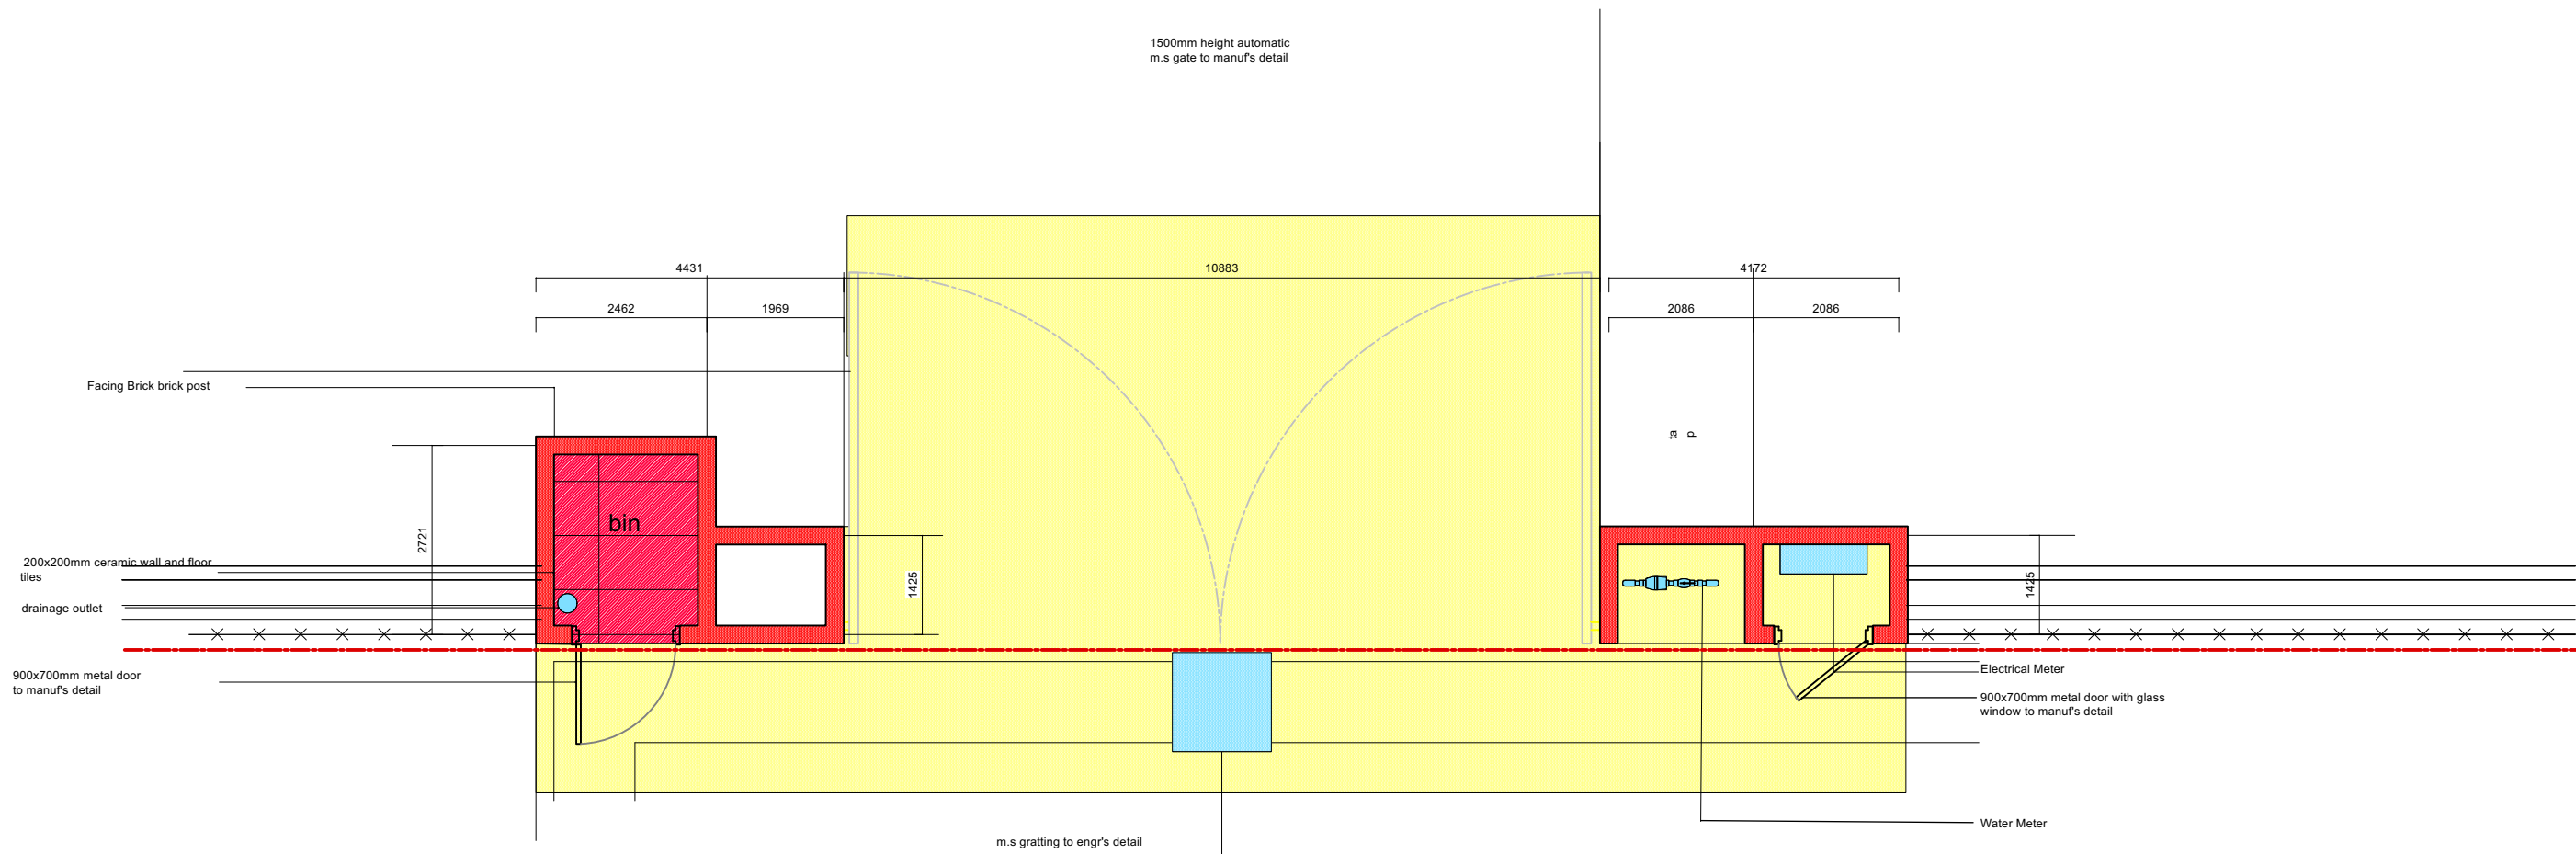

PLAN

scale 1:50