


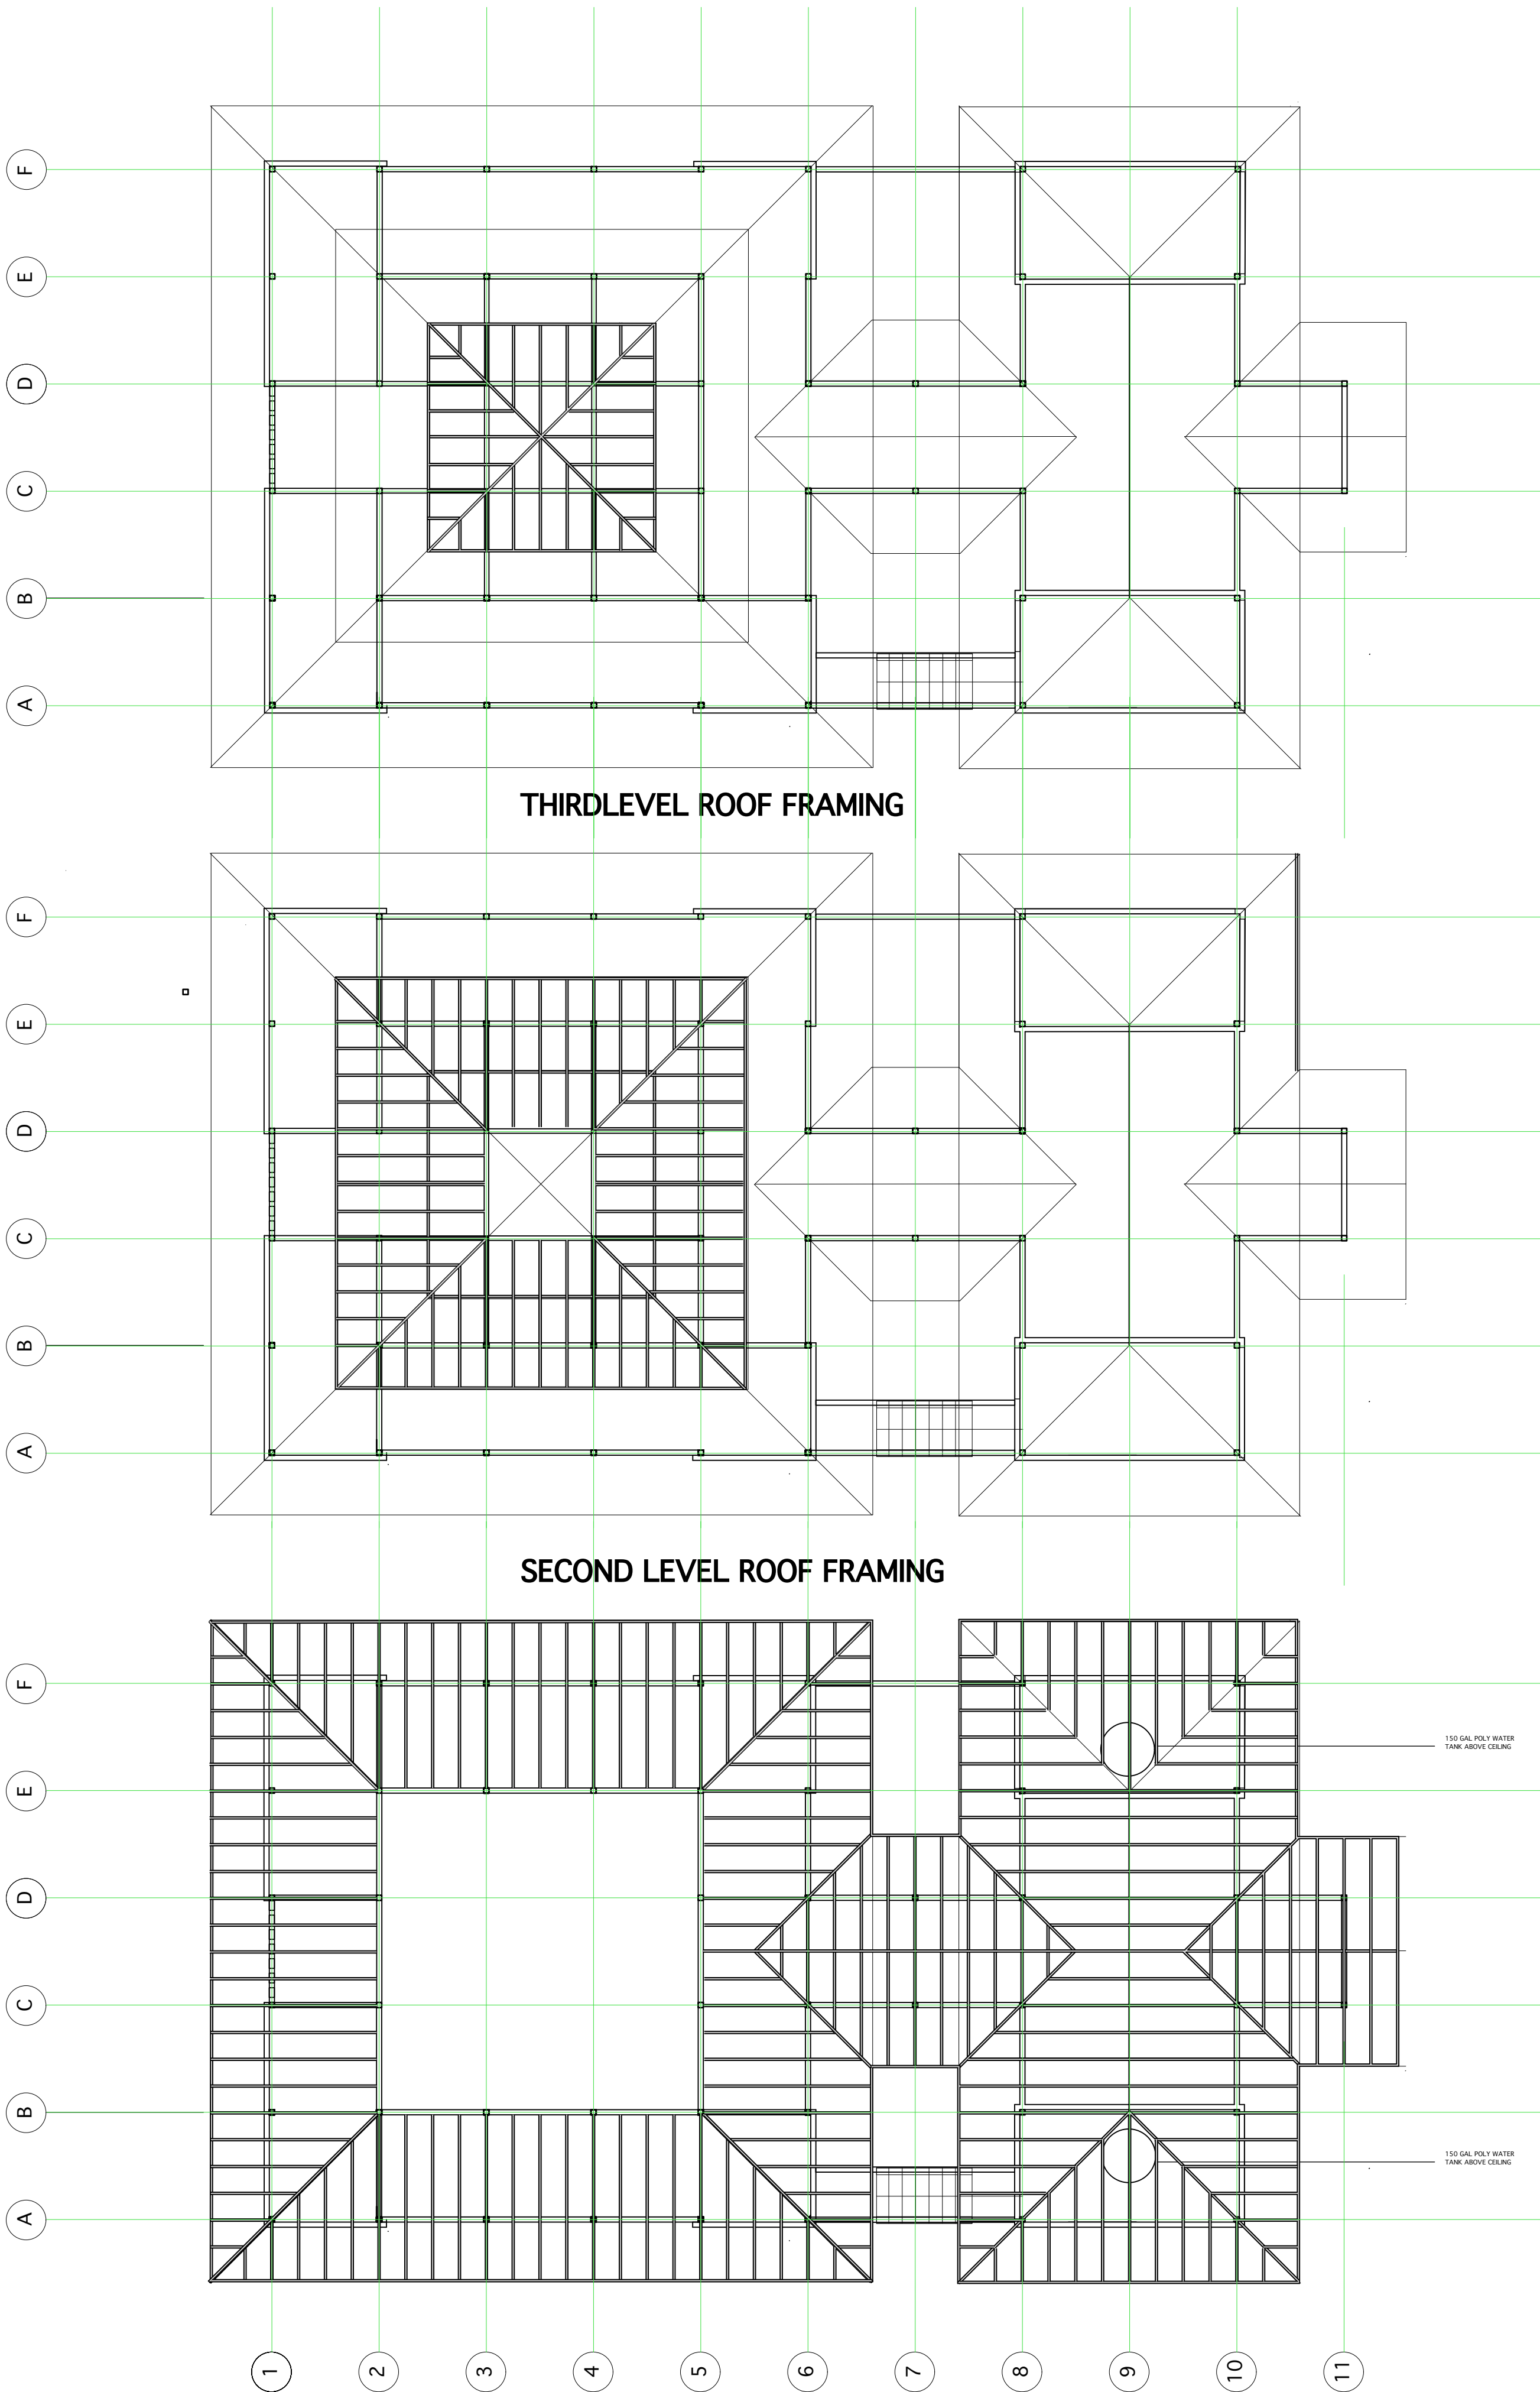

THIRDLEVEL ROOF FRAMING

SECOND LEVEL ROOF FRAMING

FIRST LEVEL ROOF FRAMING

NOTE:
-ALL GI RAFTERS AND ASSOCIATED ROOF SUPPORTING PURLINS TO BE PLAIN GI AND NOT COLOURED TYPE
- ALL EXPOSED MILD STEEL BEAMS AND COLUMNS TO BE PAINTED WITH ANTI-RUST PRIMER AND THREE COATS OF APPROVED MICACEAOUS PAINT

NO FILE RUJUKAN :

UNTUK KEGUNAAN MDKP

TAJUK PROJEK:

CADANGAN MEMBINA 1 UNIT SURAU 1 TINGKAT
DIATAS LOT 20093,
TAMAN JUASSEH SENTOSA,
PEKAN JUASSEH, DAERAH KUALA PILAH
NEGERI SEMBILAN DARUL KHUSUS
UNTUK
TETUAN JABATAN HAL EHWAL AGAMA ISLAM
NEGERI SEMBILAN

TANDATANGAN PEMILIK TANAH / BANGUNAN :

"Saya/Kami bersetuju untuk mematuhi pelan bangunan yang diluluskan. Dengan ini saya/kami bersetuju untuk dikenakan tindakan undang-undang yang berkaitan dengannya jika gagal mematuhi nya".

JABATAN HAL EHWAL AGAMA ISLAM
KUALA PILAH NEGERI SEMBILAN
PECAWAN AGAMA DAERAH : HARDI BIN MOHAMAD SADALI
NO. K/P : 750098-10-5965
NO TEL : 06-46211029
EMAIL : pad@kualapilah.jheains@ns.gov.my
ALAMAT : JHEAINS Kuala Pilah, 70200 Kuala Pilah
Negeri Sembilan

ARKITEK:

"SAYA MEMPERAKUI BAHAWA BUTIRAN - BUTIRAN DI DALAM PELAN - PELAN INI ADALAH MENURUT KEHENDAK - KEHENDAK UNDANG - UNDANG KECIL BANGUNAN SERAGAM (PBTNS) 1986 DAN SAYA SETUJU TERIMA TANGGUNGJAWAB PENUH DENGAN SEWAJARNYA"



Ar. Wan Azami Bin Hamzah
ARKITEK PROFESIONAL
No Pendaftaran LAM : A/W 56



NO. 2 JALAN MERAH PELANGI SATU
U9/19a KELAB GOLF MONTEREZ
40150 SHAH ALAM, SELANGOR MALAYSIA
NO. TEL : 019 2063 100 / 012 324 0914
EMAIL : wah.architect@gmail.com

STATUS LUKISAN :

☐ PRELIMINARY ☐ SUBMISSION ☒ CONSTRUCTION
☐ INFORMATION ☒ TENDER ☐ DEVELOPMENT ORDER

TAJUK LUKISAN:

FLOOR PLAN, ROOF PLAN,
DOOR, WINDOW &
LIGHTING AND VENTILATION
SCHEDULES

DILUKIS OLEH	JW
DISEMAK OLEH	WA
TARIKH	Dec 2025
SKALA	1:100
NO DWG.	SJS/BP/002