




NOTES ON EARTHWORKS:

1. ALL LEVELS ARE IN METRE.
2. ALL LEVELS SHOWN ARE FINISHED PLATFORM / ROAD LEVELS.
3. THIS DRAWING SHALL BE READ IN CONJUNCTION WITH THE ARCHITECT'S DRAWINGS AND ANY DISCREPANCY TO BE BROUGHT FORWARD TO ENGINEER'S NOTICE.
4. SOIL EROSION CONTROL SHALL BE ERRECTED BEFORE EARTH CUTTING AND FILLING COMMENCE.
5. ALL SLOPES OF CUTTING SHALL HAVE A MINIMUM SLOPE OF 1 TO 1.5 AND FILL EMBANKMENTS AT SLOPE OF 1 TO 2.
6. BACKFILLING OF EMBANKMENTS SLOPES AND PLATFORM SHALL NOT EXCEED 230mm THK. IN LAYERS AND TO BE WELL COMPACTED BY 15 TONS (150KN) VIBRATING ROLLER.
7. ALL EXCAVATED EARTH TO BE CARRIED AWAY AS DIRECTED BY THE SUPERINTENDING OFFICER.
8. LOCATION FOR DUMPING OF EXCAVATED EARTH TO BE APPROVED BY THE LOCAL AUTHORITY.
9. WHERE THE GROUND IS CONSIDERED UNSATISFACTORY BY THE ENGINEER, THE CONTRACTOR SHALL EXCAVATE FURTHER TO GOODROCK AND BACKFILL WITH SELECTED EARTH AT EVERY 150mm THK. IN LAYERS AND TO BE WELL COMPACTED BY MECHANICAL MEANS.
10. ANY DAMAGE TO EXISTING ROADS AND DRAINS ARE TO BE MADE GOOD BY THE CONTRACTOR.
11. THE OPEN SPACE AND SIDE TABLE TO BE LEVELLED AND SPOT TURFED UNLESS OTHERWISE STATED.
12. ALL SILT TRAP, EARTHDRAINS AND EARTH SUMPS ARE TEMPORARY AND TO BE REMOVED AND BACKFILLED AFTER EARTHWORKS BECOME STABILISED AND PROPER DRAINAGE CONSTRUCTED.
13. THE CONTRACTOR SHALL CONSTRUCT A WASH TROUGH COMPLETE WITH A PRESSURE WATER JET.
14. THE FINISHED LEVEL OF THE PROPOSED ROADS AND PLATFORM LEVELS ARE SUCH THAT THEY WILL PERMIT CONNECTION OF ROADS TO ADJOINING EXISTING OR FUTURE ROADS.
15. NO PONDING WILL OCCUR AS A RESULT OF THE THE PROPOSED EARTHWORKS.
16. NO ENCROACHMENT INTO ADJACENT LOT WILL OCCUR UNLESS WITH THE CONSENT OF ADJOINING LAND OWNER.
17. CONTRACTOR SHALL INSTALL GEOTECTILE BELOW THE ROAD AND PARKING AREA.

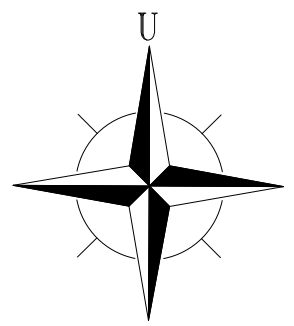


SKALA 1 : 400 (A1)
SYIT PAIAWAI : 49-A-II

TBM 1
RL= 83.530m.
Paku atas konkrit

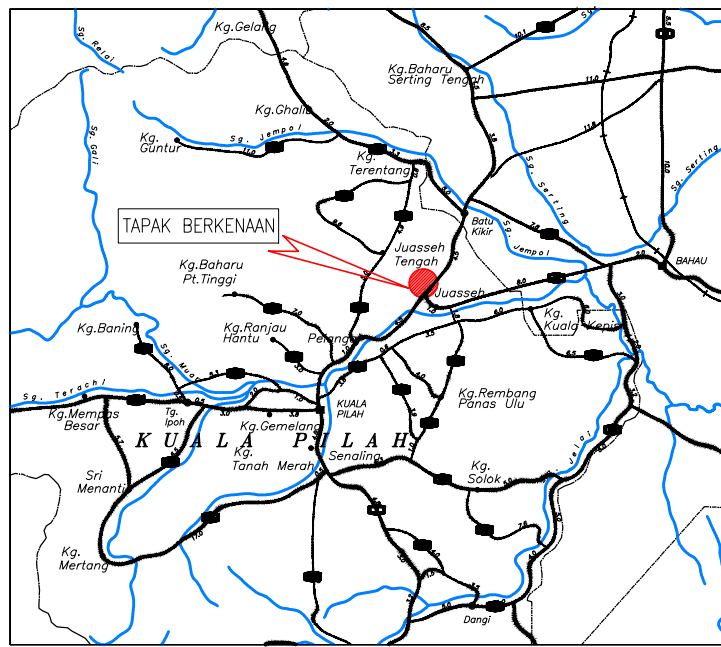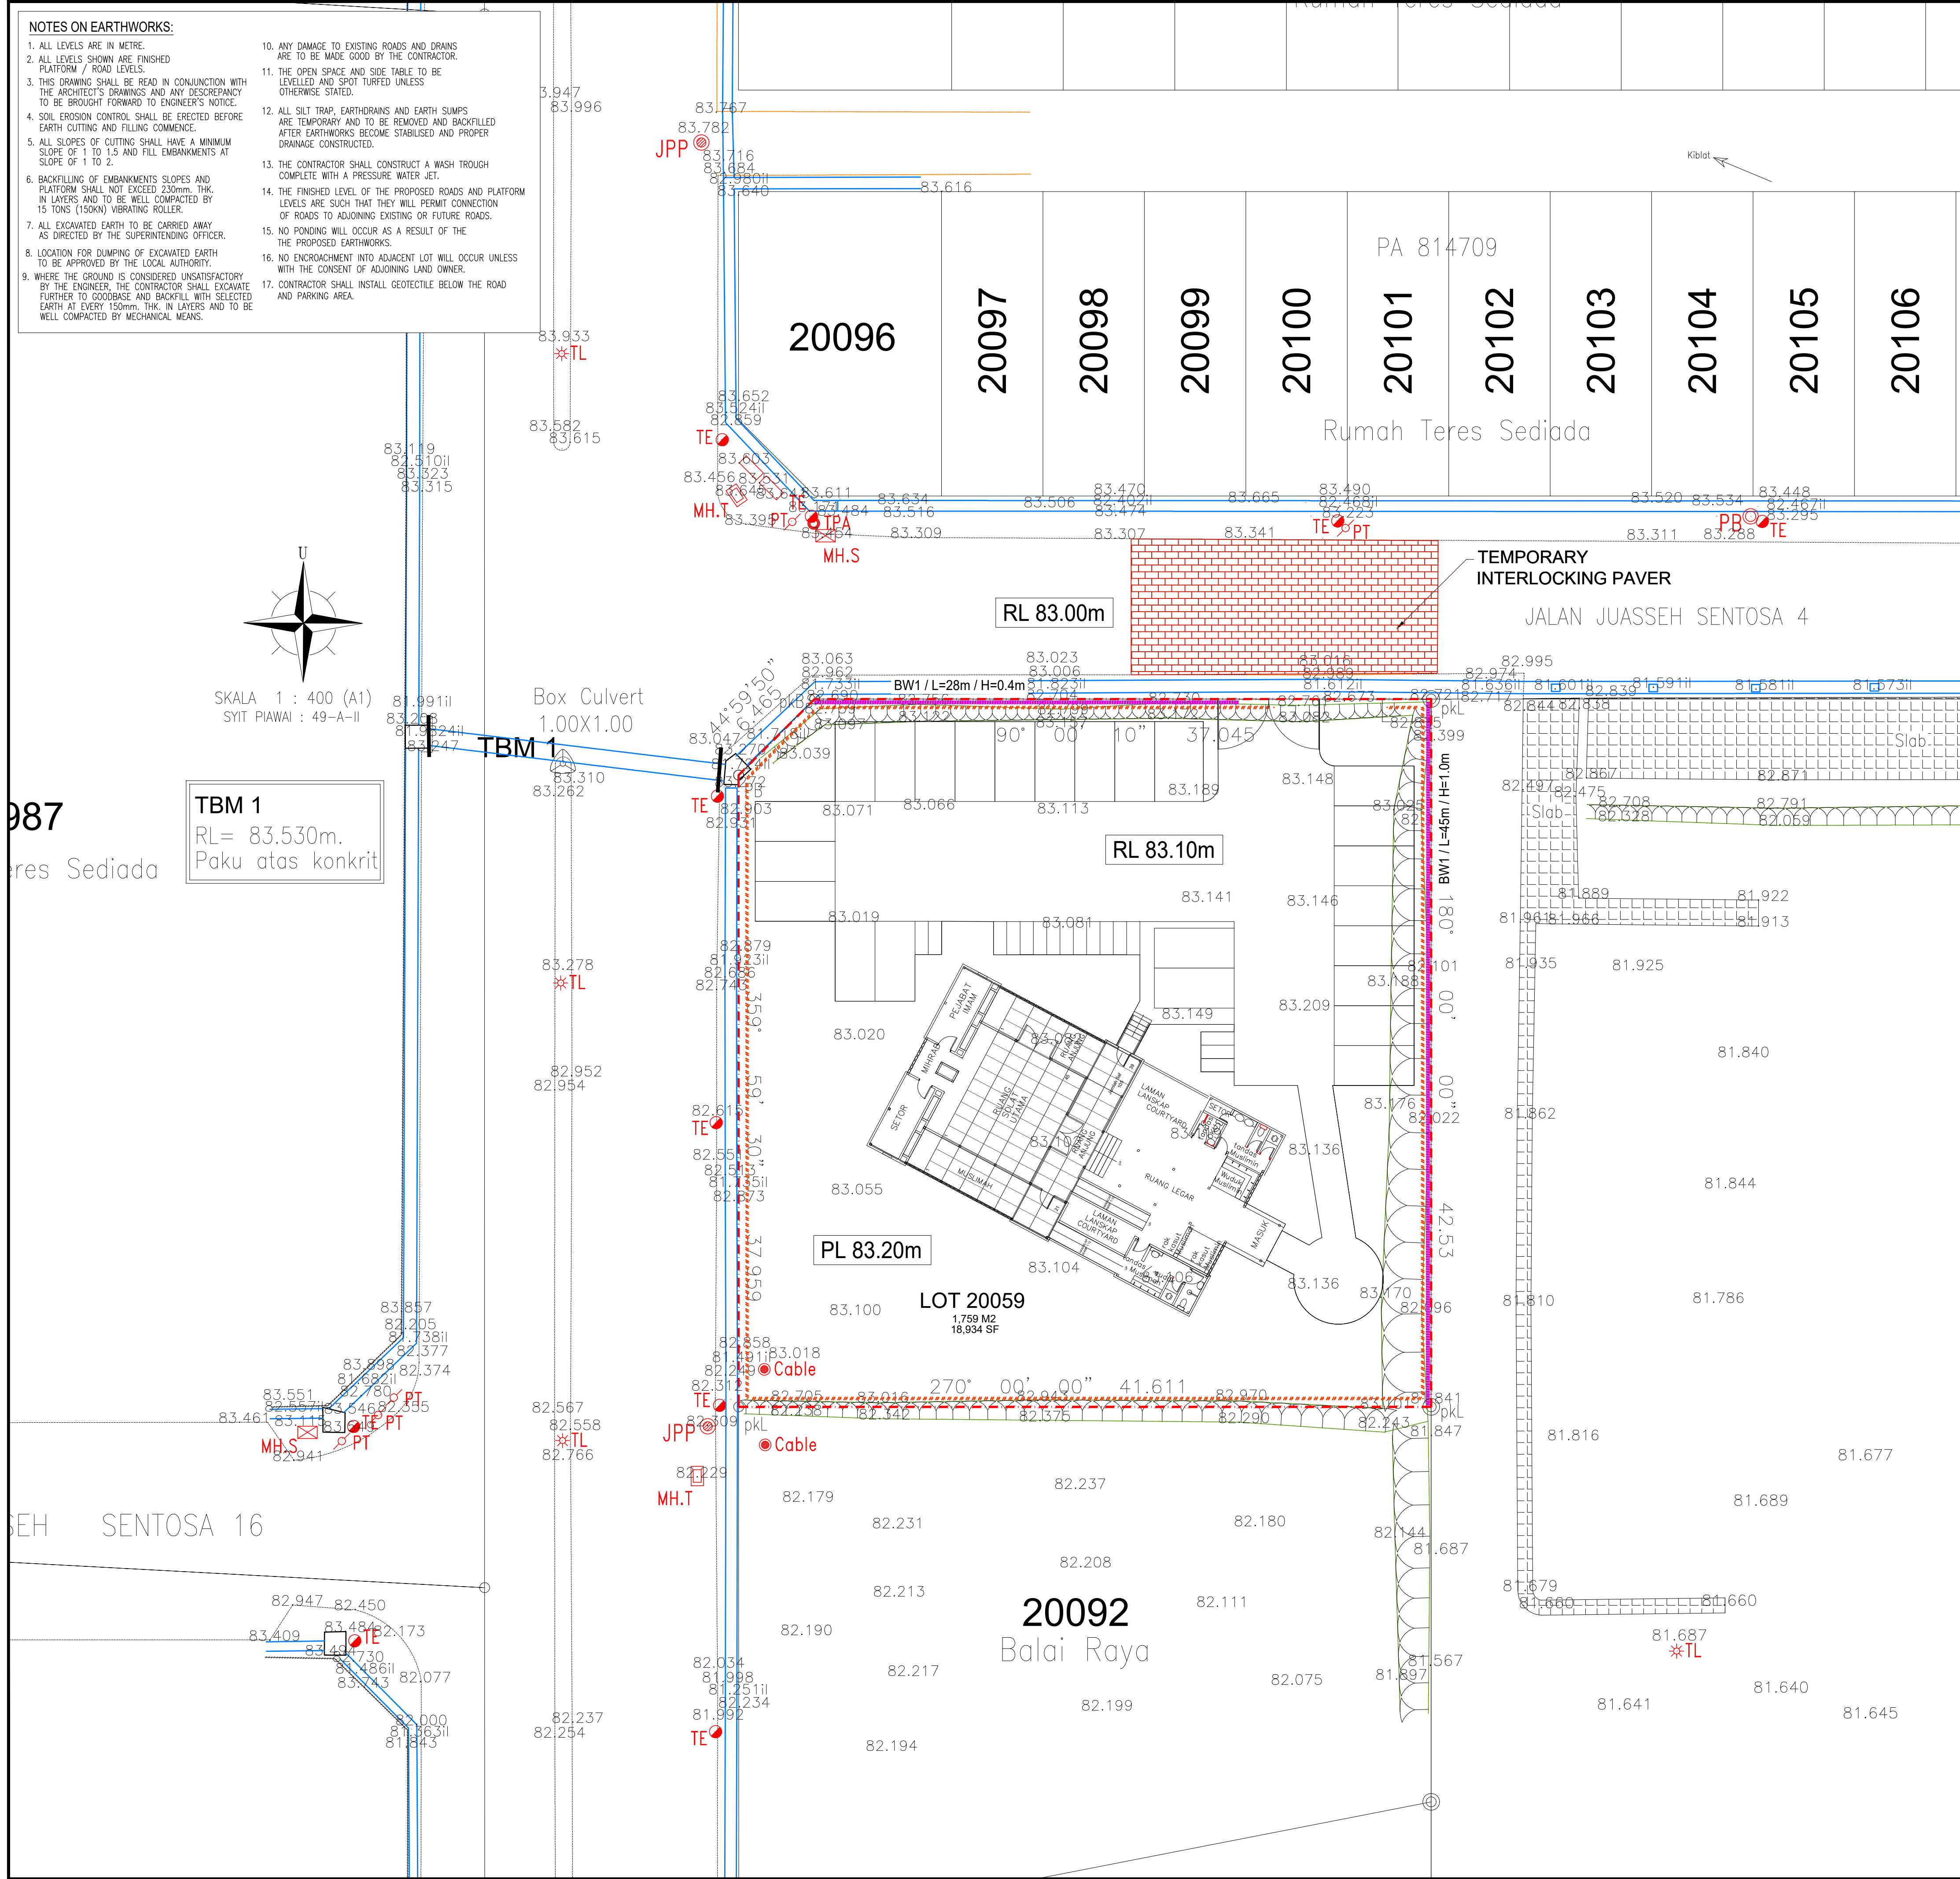

PELAN KUNCI

SKALA : TANPA SKALA

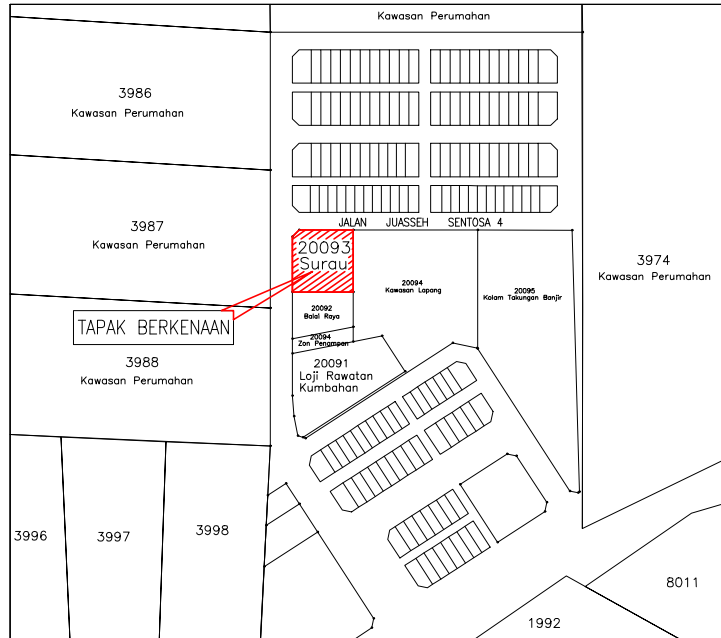

PELAN LOKASI

SKALA : 8 INCH SENG

LEGEND :

- BOUNDARY LINE
- PROPOSED BRICK WALL
- PROPOSED FINISHED EARTH PLATFORM LEVEL
- PROPOSED FINISHED ROAD LEVEL
- SILT FENCE
- TEMPORARY EARTH DRAIN

DECLARATION

DUE TO THE SITE CONSTRAINT, SILT TRAP AND WASH TROUGH CAN'T BE PROVIDED. HOWEVER, I/WE HEREBY UNDERTAKE TO ENSURE THE SILT WATER WOULD NOT RETAINED WITHIN THE SITE AND THE CLEANLINESS OF THE PUBLIC ROADS TO BE MAINTAINED IN ORDER TO COMPLY FULLY WITH THE REQUIREMENTS THE STREET, DRAINAGE AND BUILDING ACT 1974 AND THE EARTHWORKS (FEDERAL TERRITORY OF KUALA LUMPUR) BY LAWS 1988.

PENGESAHAN PERUNDING

1. THE FINISHED PLATFORM LEVEL OF PROPOSED ROADS AND PLATFORM LEVELS ARE SUCH THAT THEY WILL PERMIT CONNECTION OF ROADS TO ADJOINING EXISTING OF FUTURE ROADS
2. NO WATER PONDING WILL OCCUR AS A RESULT OF THE PROPOSED EARTHWORKS.
3. NO ENCROACHMENT TO THE ADJACENT LOT WILL OCCUR.

SUBMISSION DRAWING

NO. FAIL (KEGUNAAN PEJABAT)

COP KELULUSAN (KEGUNAAN PEJABAT)

BIL	TARIKH	PINDAAN

TAJUK PERMOHONAN :

CADANGAN MEMBINA 1 UNIT SURAU 1 TINGKAT DIATAS LOT 20093, TAMAN JUASSEH SENTOSA, PEKAN JUASSEH, DAERAH KUALA PILAH, NEGERI SEMBILAN DARUL KHUSUS UNTUK TETUAN JABATAN HAL EHWAL AGAMA ISLAM NEGERI SEMBILAN

TAJUK LUKISAN :

ESCP
KEY PLAN, LOCATION PLAN AND LAYOUT PLAN

PEMILIK :

"Saya bersektu bertanggung jawab sekiranya berlaku kerosakan kepada bangunan di lot setelah-menyebelah akibat dari kerja-kerja dalam permohonan ini."

JABATAN HAL EHWAL AGAMA ISLAM KUALA PILAH NEGERI SEMBILAN
PEGAWAI AGAMA DAERAH : HARDI BIN MOHAMAD SADALI
NO. KP : 709068-10-5965
NO TEL : 06-4821029
EMAIL : paidkuatplah.jheains@ns.gov.my
ALAMAT : JHEAINS Kuala Pilah, 70200 Kuala Pilah Negeri Sembilan

JURUTERA PERUNDING :

JURUTERA BUDIMAN SENDIRIAN BERHAD
73B & 75B, Jalan SS 21/37, Damansara Utama, 47400 Petaling Jaya, Selangor Darul Ehsan, Tel: 03-7727 2515 Fax: 03-7727 7606 Email: juruterabudiman@gmail.com (Company No. 235335-P)

TANDATANGAN JURUTERA BERTAULIAH

I hereby certify that these works have been designed by me in accordance with sound engineering practice and that I take full responsibility for the design and proper performance of the same.

JURUTERA BUDIMAN SDN.BHD.
(235335-P)
I, MOHD NASPI BUSTAMAN
C110264
MALAYSIA
Pengarah

Scale	1:200 (A1)	Designed By	MI
Date	DECEMBER 2025	Checked By	Ir Shahrizal
Drawn By	SMK	Approved By	Ir Mohd Naspi

DRAWING NO:
SJ/ESCP/LP/01