


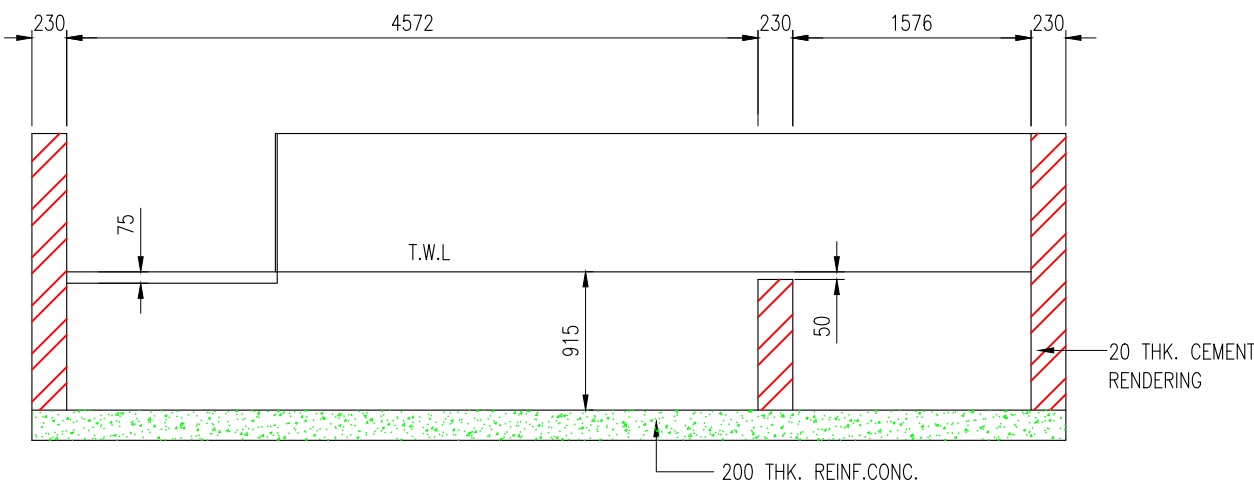


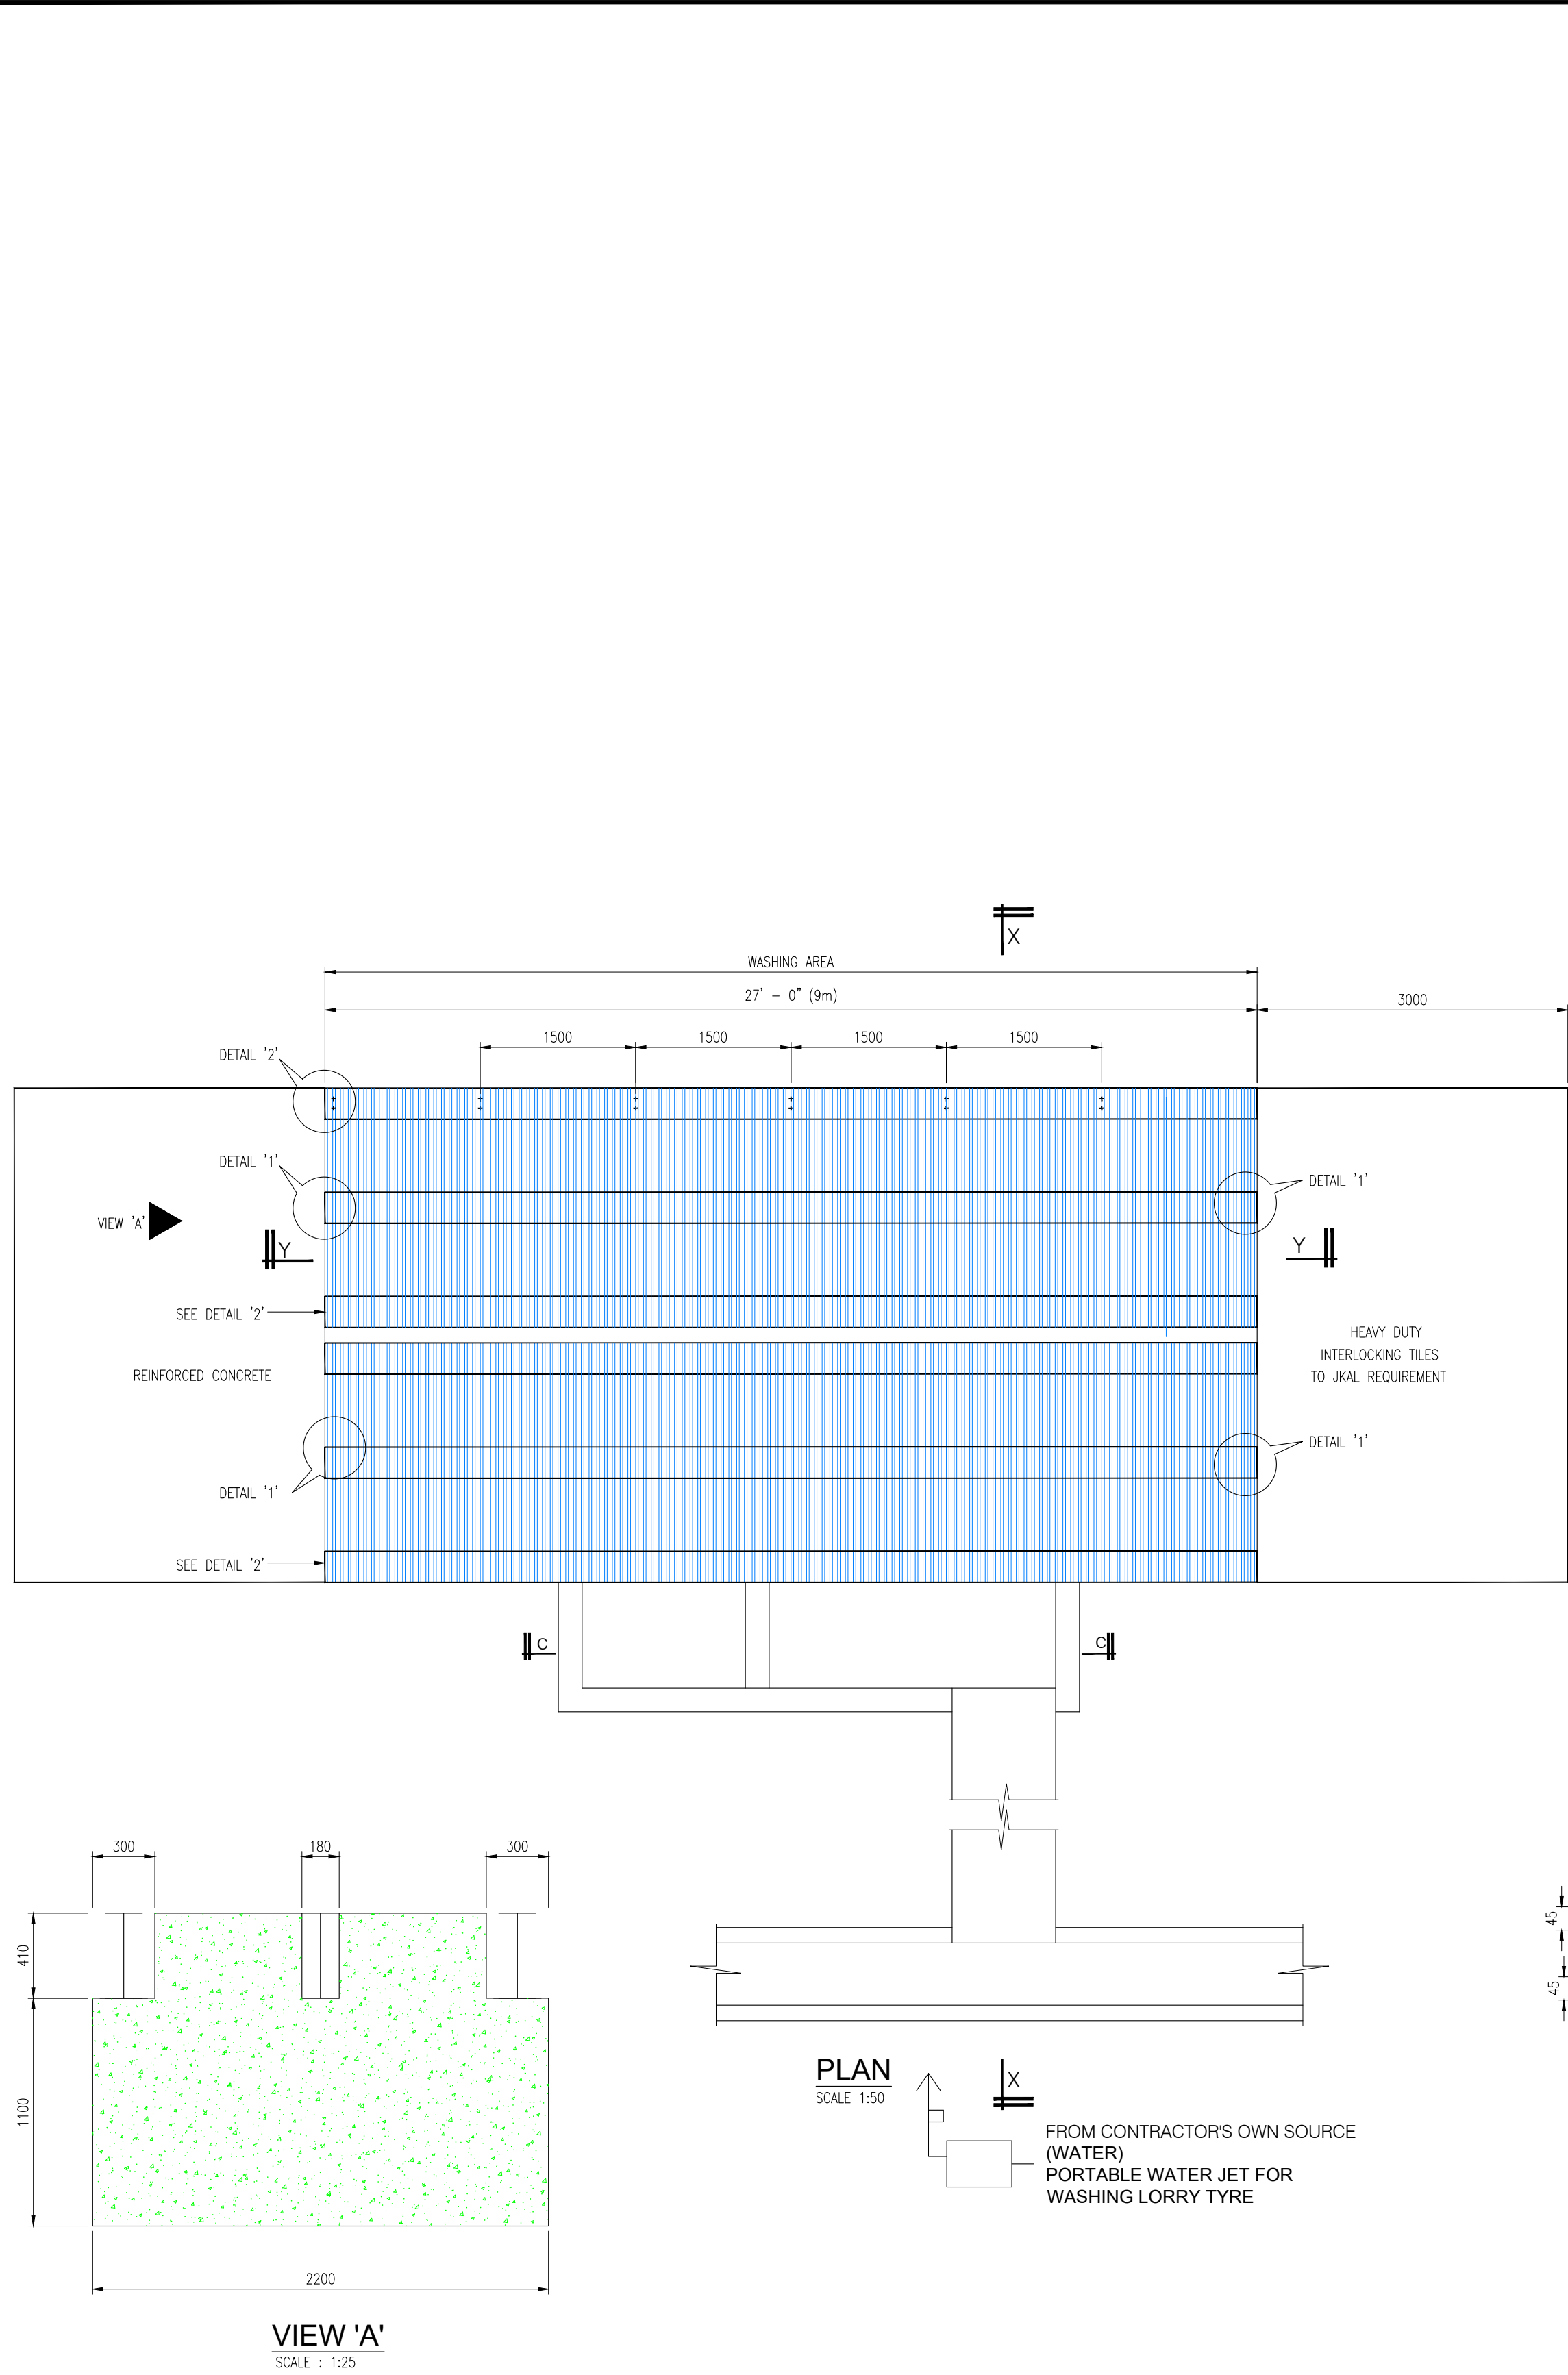

SECTION C - C
SCALE 1:50

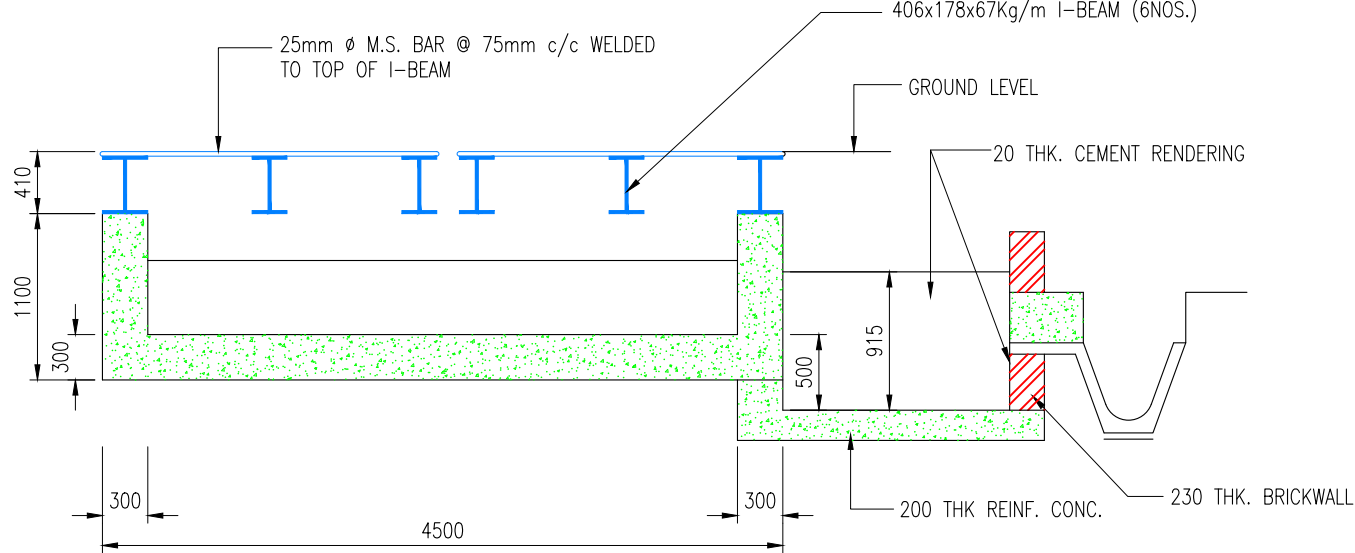


CROSS SECTION (X-X)
SCALE 1:50

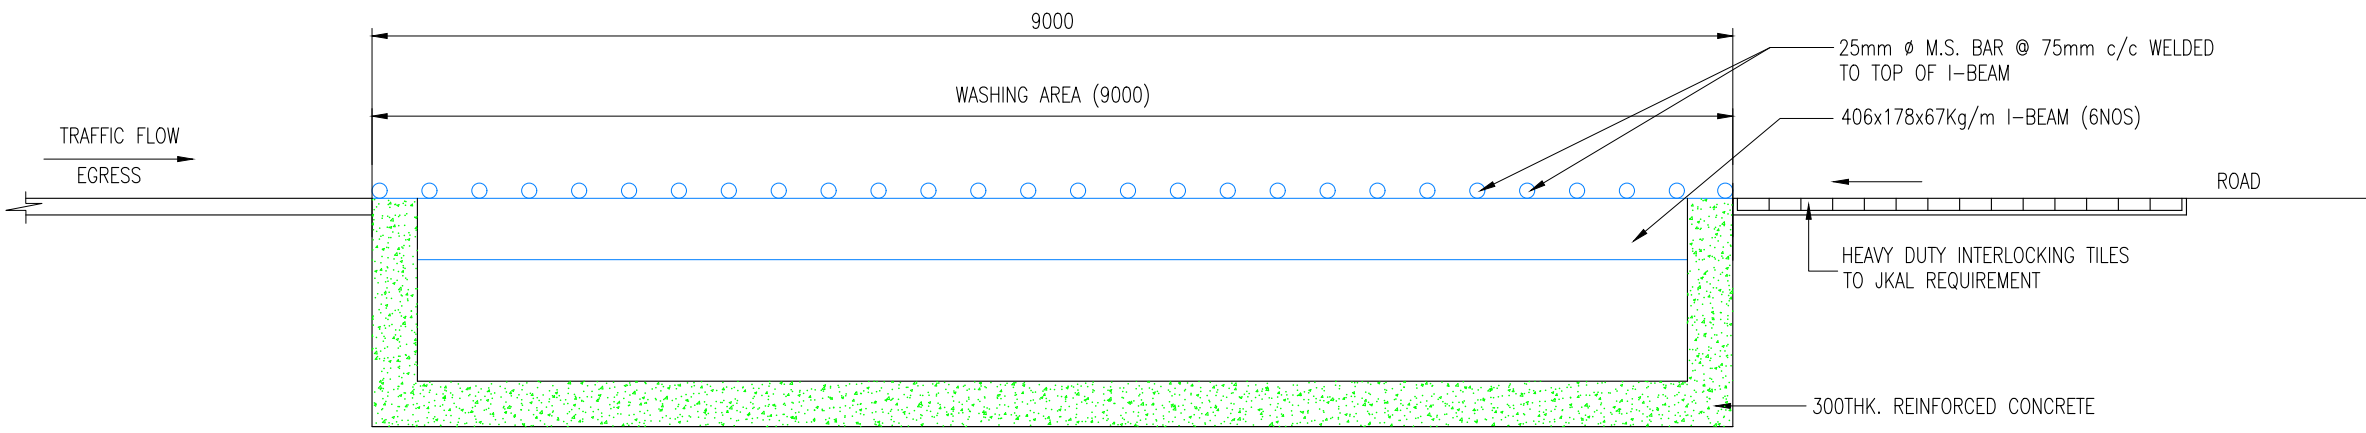


LONGITUDINAL SECTION (Y - Y)
SCALE 1:50


NOTE:
1. TO PROVIDE WASH TROUGH AT INGRESS & EGRESS.
2. LOCATION OF WASH TROUGH TO BE DECIDED ON SITE.
3. DETAILS SUBJECT TO MPJBT APPROVAL.

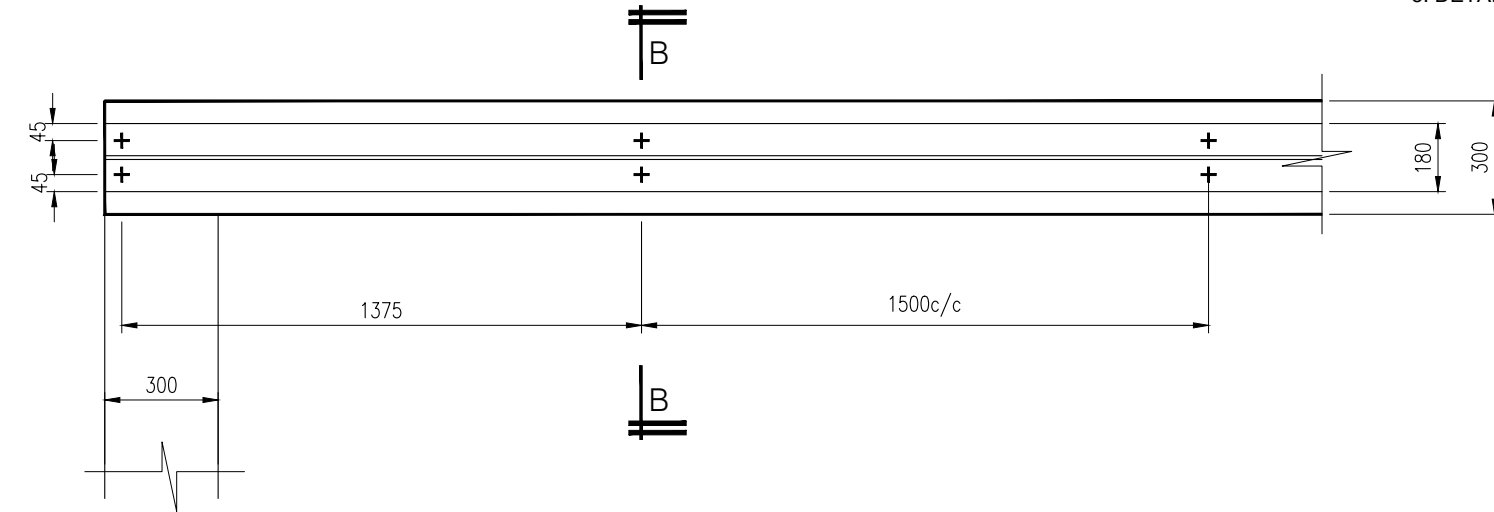


DETAIL '2'
SCALE : 1:20

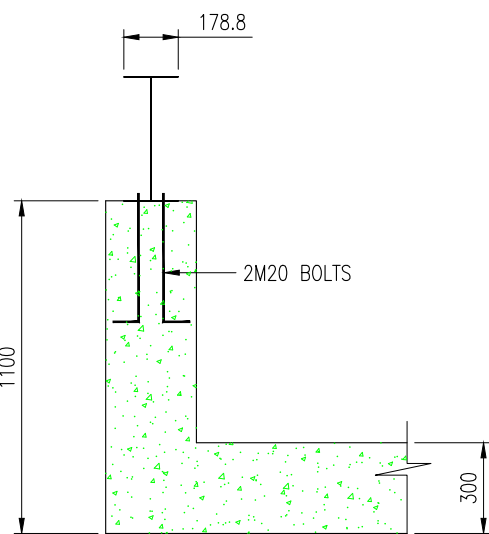


SECTION B-B
SCALE : 1:25

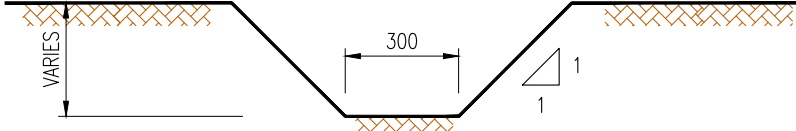

TEMPORARY EARTH DRAIN
DURING CONSTRUCTION
SCALE 1:20

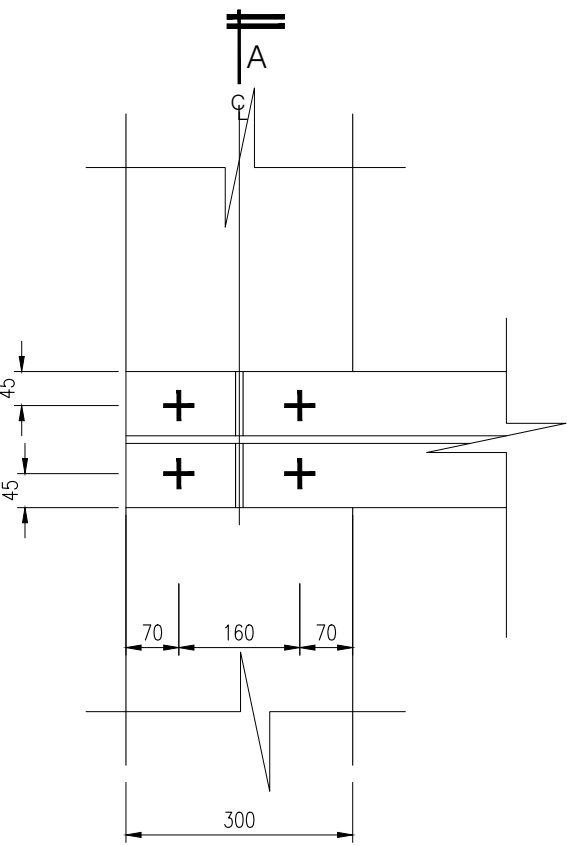

DETAIL '1'
SCALE : 1:10

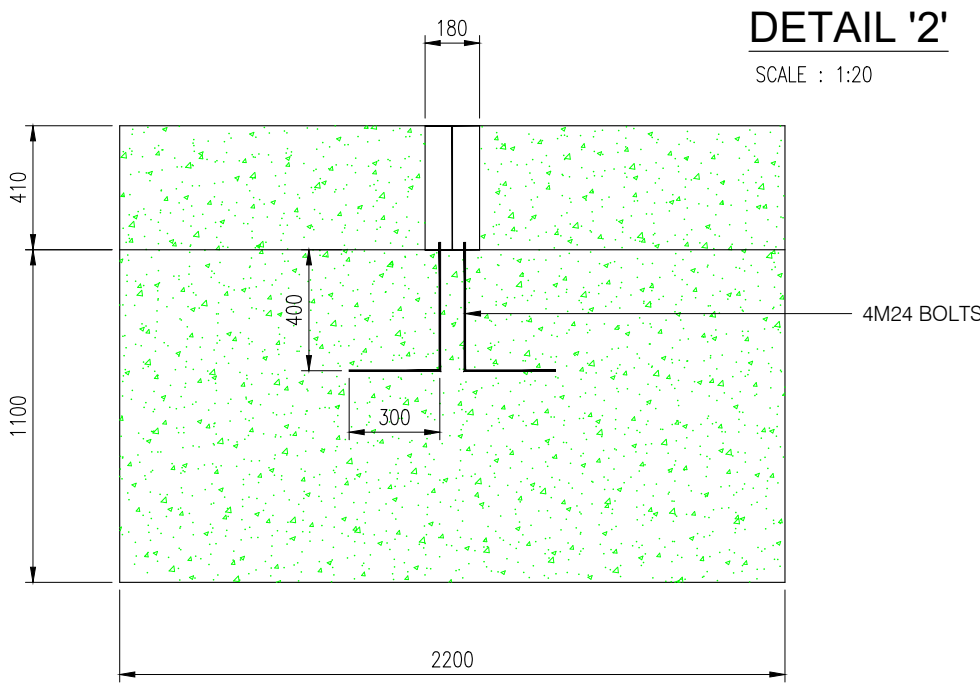

SECTION A-A
SCALE : 1:25

PLAN
SCALE 1:50

FROM CONTRACTOR'S OWN SOURCE
(WATER)
PORTABLE WATER JET FOR
WASHING LORRY TYRE

NO. FAIL (KEGUNAAN PEJABAT)

COP KELULUSAN (KEGUNAAN PEJABAT)

BIL	TARIKH	PINDAAN

TAJUK PERMOHONAN :
CADANGAN MEMBINA 1 UNIT SURAU 1 TINGKAT
DIATAS LOT 20093, TAMAN JUASSEH SENTOSA,
PEKAN JUASSEH, DAERAH KUALA PILAH, NEGERI
SEMBILAN DARUL KHUSUS
UNTUK
TETUAN JABATAN HAL EHWAL AGAMA ISLAM
NEGERI SEMBILAN

TAJUK LUKISAN :
EARTHWORK
WASH TROUGH AND TEMPORARY EARTH DRAIN DETAILS

PEMILIK :
"Saya bersetuju bertanggung jawab sekiranya berlaku kerosakan kepada bangunan di lot
sebelah-menyebelah akibat dari kerja-kerja dalam permohonan ini."

KUALA PILAH NEGERI SEMBILAN
PEGAWAI AGAMA DAERAH : HARDI BIN MOHAMAD SADALI
NO. KIP : 750908-10-5065
NO TEL : 06-4821029
EMAIL : paidkualapilah.jheains@ns.gov.my
ALAMAT : JHEAINS Kuala Pilah, 70200 Kuala Pilah
Negeri Sembilan

JURUTERA PERUNDING :
JURUTERA BUDIMAN SENDIRIAN BERHAD
73B & 75B, Jalan SS 21/37, Damansara Utama,
47400 Petaling Jaya, Selangor Darul Ehsan,
Tel: 03-7727 2515 Fax: 03-7727 7606
Email: juruterabudiman@gmail.com
(Company No. 235335-P)

TANDATANGAN JURUTERA BERTAULIAH
I hereby certify that these works have been designed
by me in accordance with sound engineering practice
and that I take full responsibility for the design and
proper performance of the same.

JURUTERA BUDIMAN SDN.BHD.
AWAM
I: MOHD NASPI BUSTAMAN
C110264
MALAYSIA
Rengarah

Scale	1:200 (A1)	Designed By	MI
Date	DECEMBER 2025	Checked By	Ir Shahrizal
Drawn By	SMK	Approved By	Ir Mohd Naspi

DRAWING NO: SJ/EW/DT/01

SUBMISSION DRAWING