



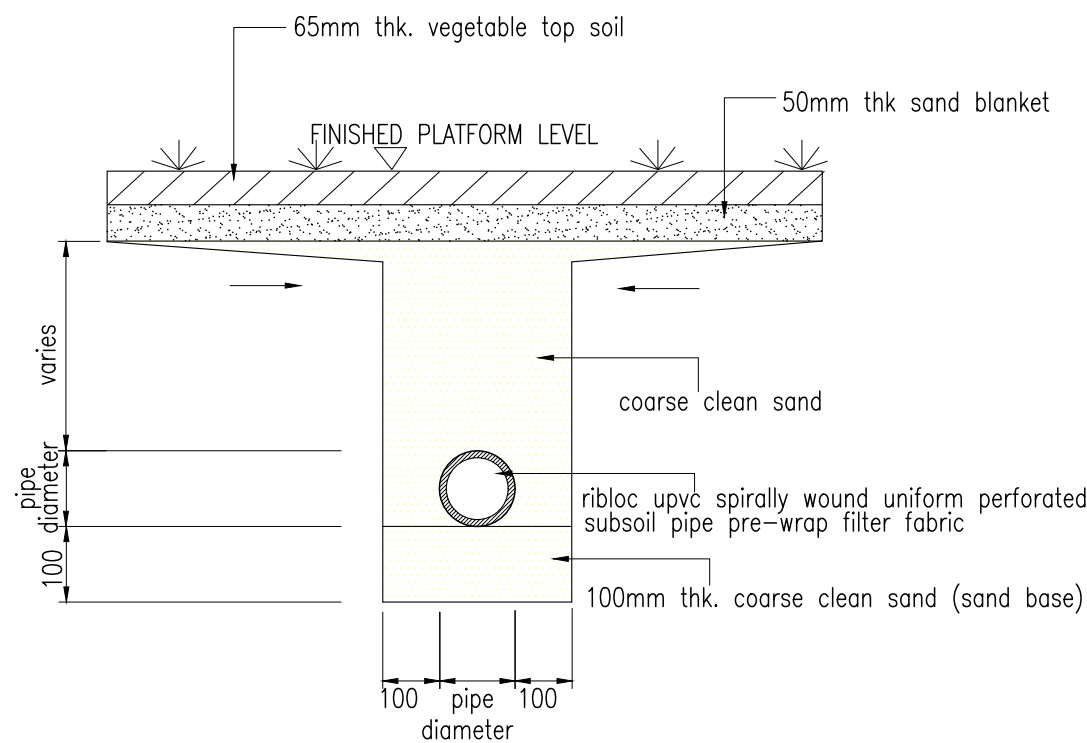

ON-FIELD TRENCH DESIGN

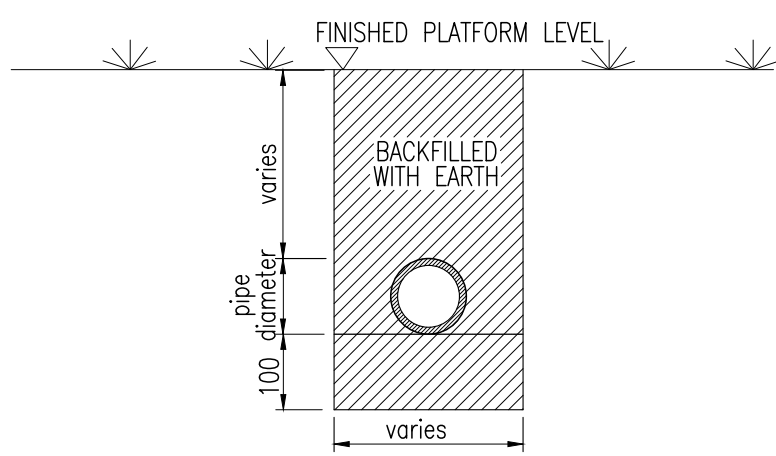


OFF-FIELD TRENCH DESIGN

TYPICAL PLAYING FIELD  
N.T.S


NOTES :

- CONTRACTORS ARE ADVISED TO FOLLOW THE CROWNSWEAR FLEXIBLE PERMEABLE HOSE SUPPLIER'S SPECIFICATION FOR INSTALLATION METHOD.
- TRENCHES SHALL BE EXCAVATED TO THE DESIGN SLOPE OF MINIMUM 2 % GRADIENT.
- ANY SHARP OBJECT OR POINTED EDGES SHALL BE REMOVED FROM THE BASE OF TRENCH.
- BACKFILL SHALL BE CARRIED OUT TO THE SPECIFIED THICKNESS
- NO HEAVY EQUIPMENT SHALL BE ALLOWED TO CROSS THE PERMEABLE HOSE BEFORE COMPACTION WORK COMPLETED.


| HOSE DIAMETER (mm) | TRENCH MINIMUM WIDTH (mm) | TRENCH MINIMUM DEPTH (mm) |
|--------------------|---------------------------|---------------------------|
| 100                | 400                       | 400                       |
| 150                | 450                       | 450                       |
| 200                | 500                       | 500                       |

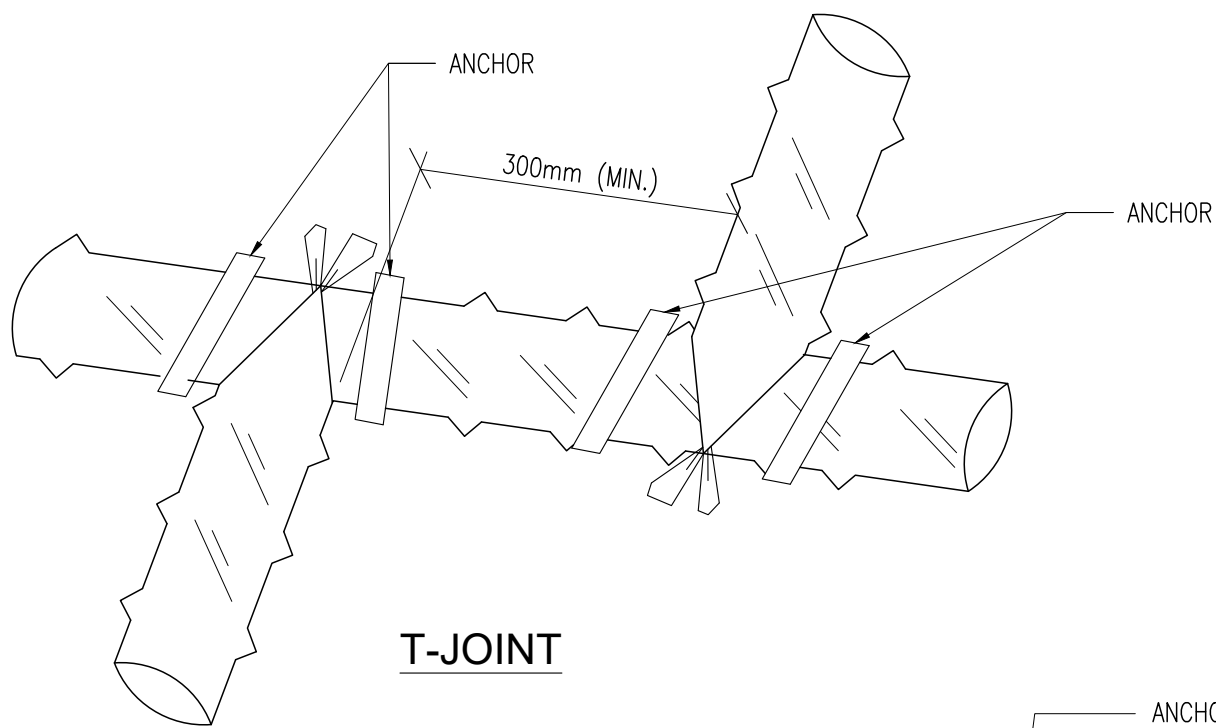


T-JOINT

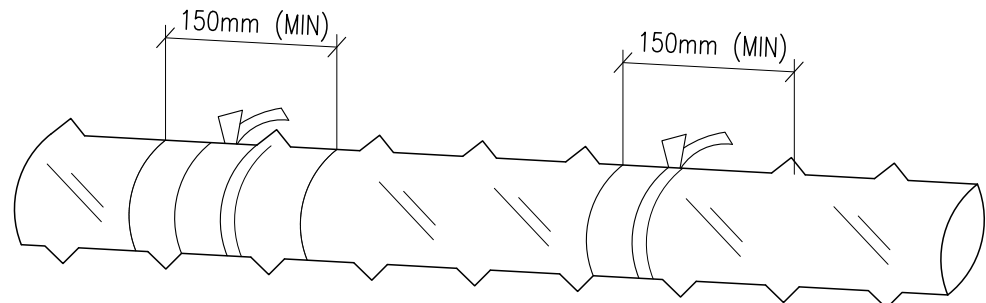


STRAIGHT

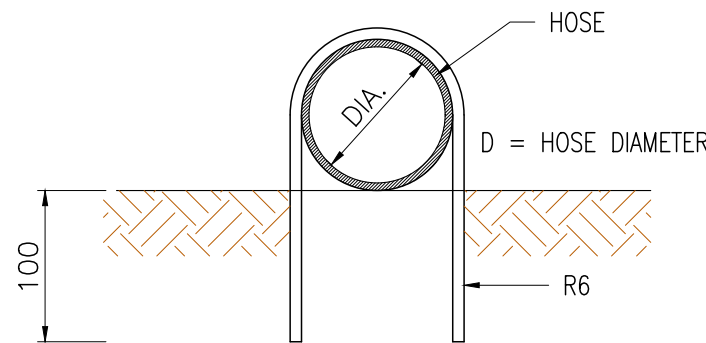


ANCHOR ROD DETAIL.

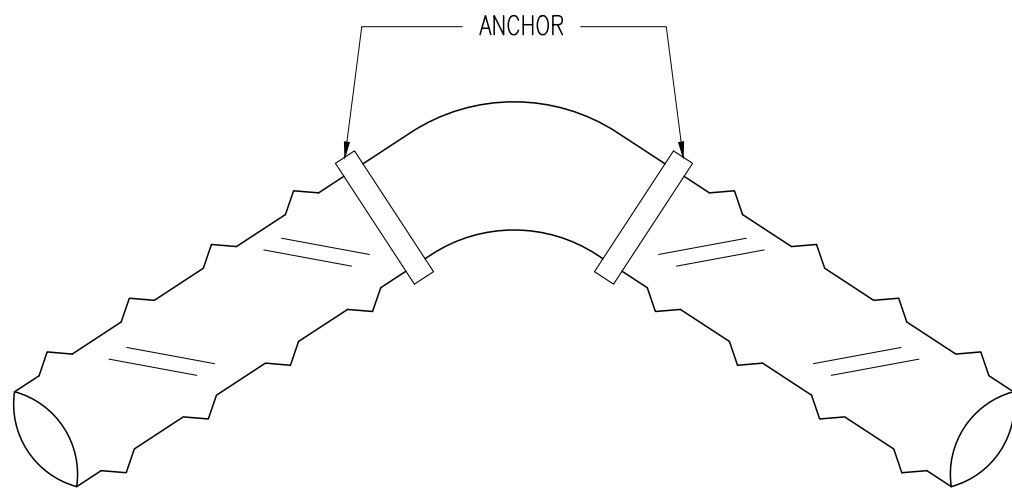

INSTALLATION OF BEND

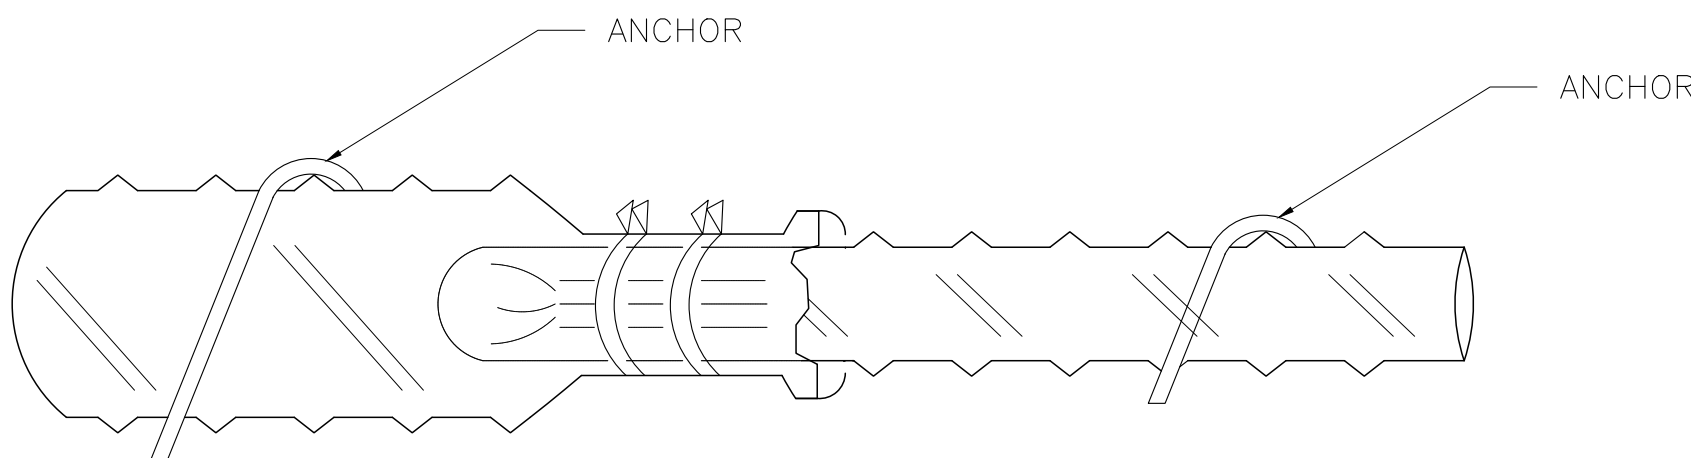

JOINTING DISSIMILAR DIA.  
HOSES IN STRAIGHT

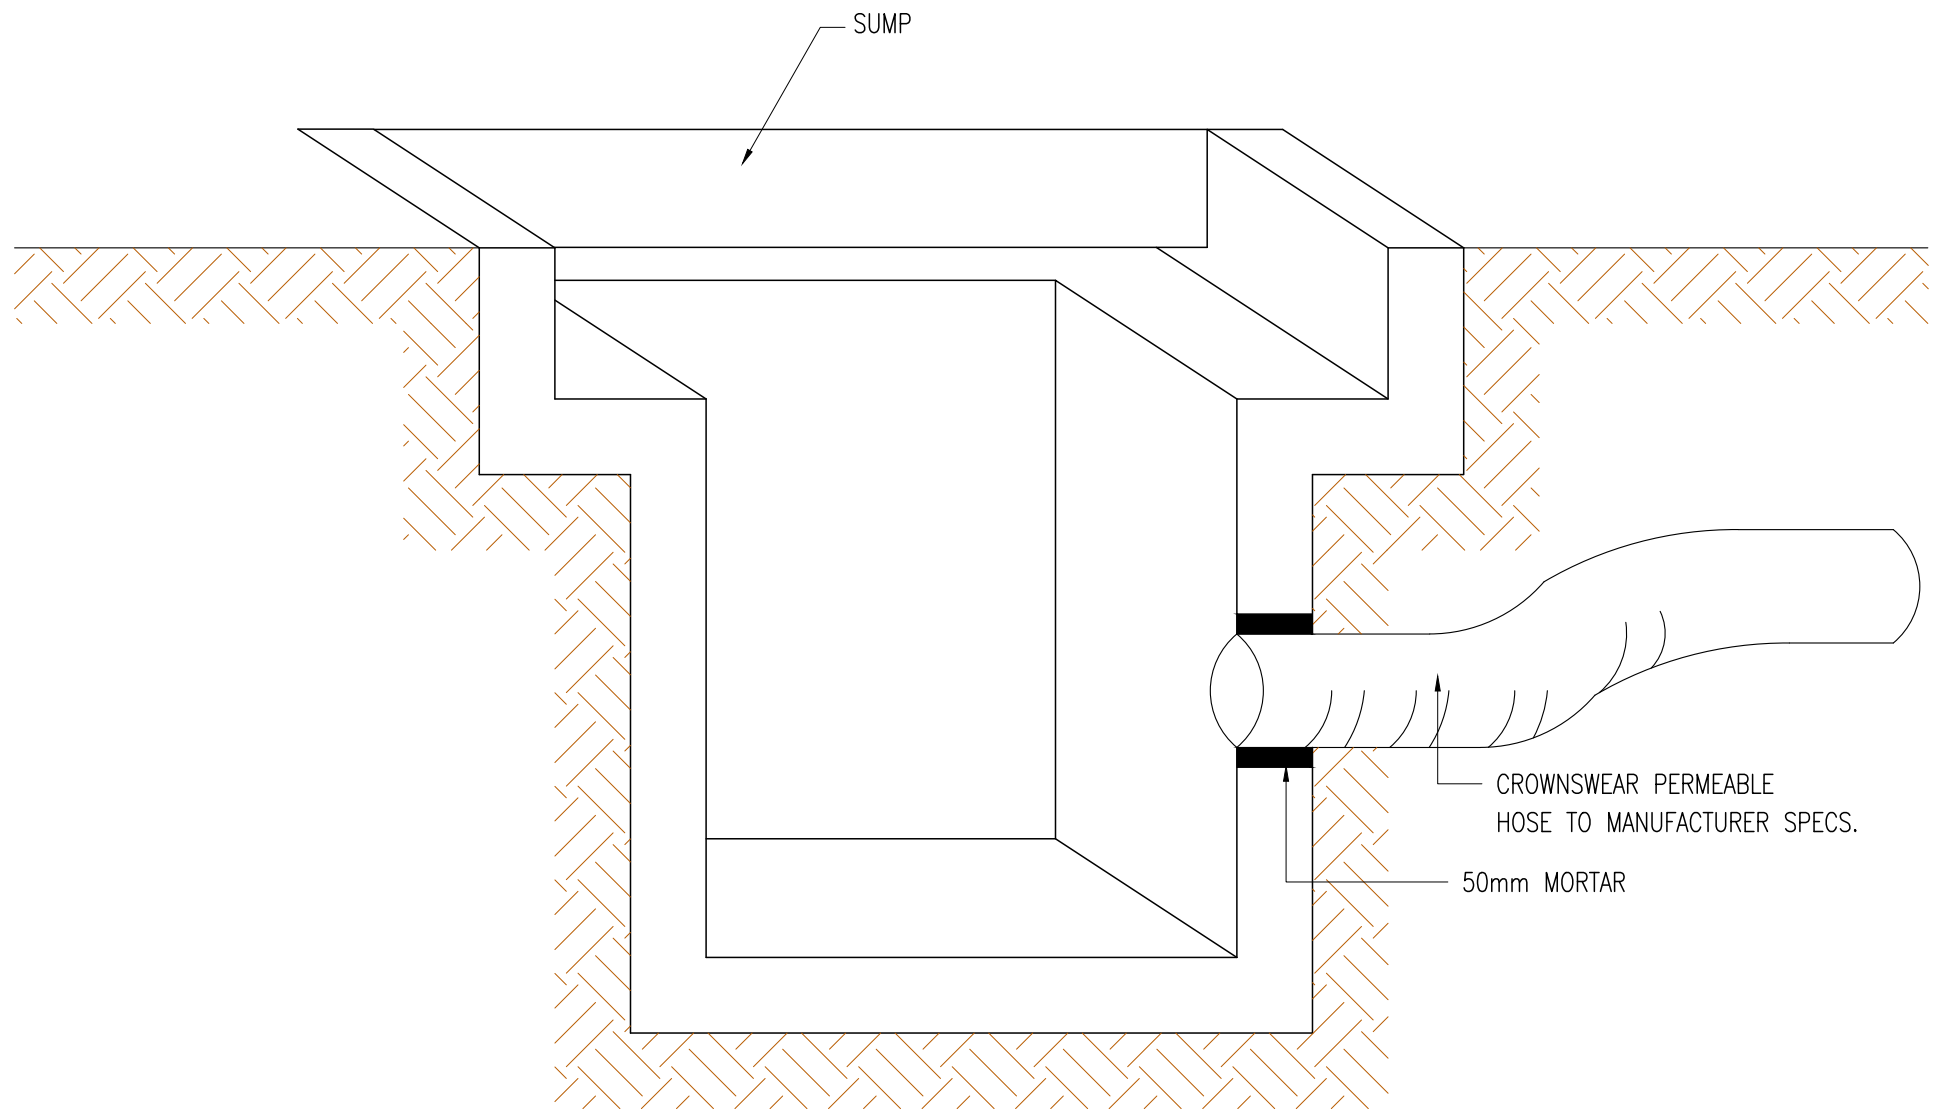

JOINTING TO SUMP

NO. FAIL (KEGUNAAN PEJABAT)

COP KELULUSAN (KEGUNAAN PEJABAT)

| BIL | TARIKH | PINDAAN |
|-----|--------|---------|
|     |        |         |
|     |        |         |
TAJUK PERMOHONAN :  
CADANGAN MEMBINA 1 UNIT SURAU 1 TINGKAT DIATAS LOT 20093, TAMAN JUASSEH SENTOSA, PEKAN JUASSEH, DAERAH KUALA PILAH, NEGERI SEMBILAN DARUL KHUSUS UNTUK TETUAN JABATAN HAL EHWAL AGAMA ISLAM NEGERI SEMBILAN

TAJUK LUKISAN :  
ROAD & DRAINAGE  
SUBSOIL DRAIN DETAILS

PEMILIK :  
"Saya bersetuju bertanggung jawab sekiranya berlaku kerosakan kepada bangunan di lot sebelah-menyebelah akibat dari kerja-kerja dalam permohonan ini."

KUALA PILAH NEGERI SEMBILAN  
PEGAWAI AGAMA DAERAH : HARDI BIN MOHAMAD SADALI  
NO. KIP : 750908-10-5965  
NO TEL : 06-4821029  
EMAIL : paidkualapilah.jheains@ns.gov.my  
ALAMAT : JHEAINS Kuala Pilah, 70200 Kuala Pilah Negeri Sembilan

JURUTERA PERUNDING :  
JURUTERA BUDIMAN SENDIRIAN BERHAD  
73B & 75B, Jalan SS 21/37, Damansara Utama, 47400 Petaling Jaya, Selangor Darul Ehsan, Tel: 03-7727 2515 Fax: 03-7727 7606 Email: juruterabudiman@gmail.com (Company No. 235335-P)

TANDATANGAN JURUTERA BERTAULIAH  
I hereby certify that these works have been designed by me in accordance with sound engineering practice and that I take full responsibility for the design and proper performance of the same.

JURUTERA BUDIMAN SDN.BHD.  
AWAM  
I: MOHD NASPI BUSTAMAN  
C110264  
MALAYSIA  
Rengarah

|                         |               |             |               |
|-------------------------|---------------|-------------|---------------|
| Scale                   | AS SHOWN      | Designed By | MI            |
| Date                    | DECEMBER 2025 | Checked By  | Ir Shahrizal  |
| Drawn By                | SMK           | Approved By | Ir Mohd Naspi |
| DRAWING NO: SJ/RD/DT/02 |               |             |               |

SUBMISSION DRAWING