
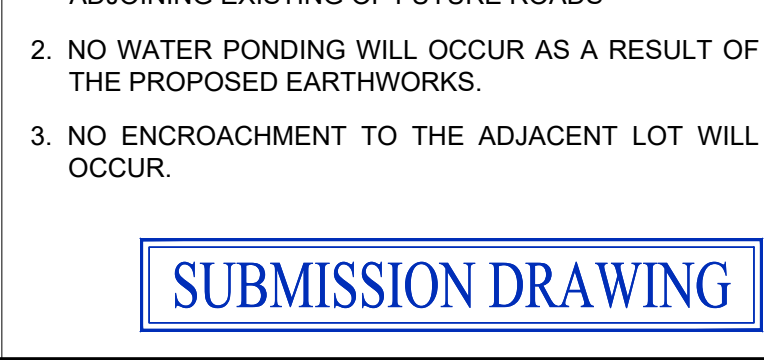
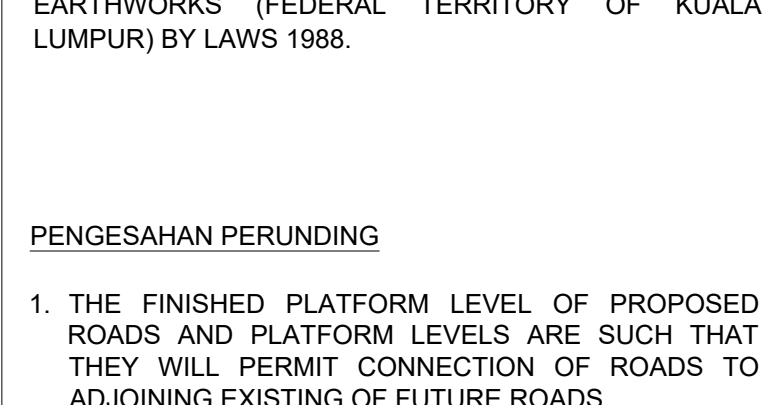
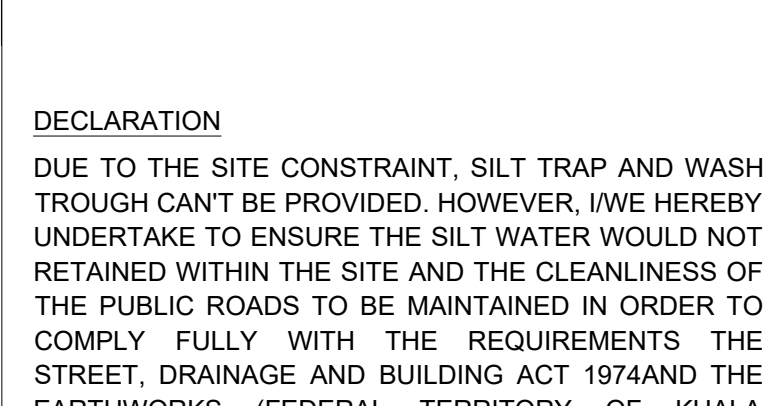
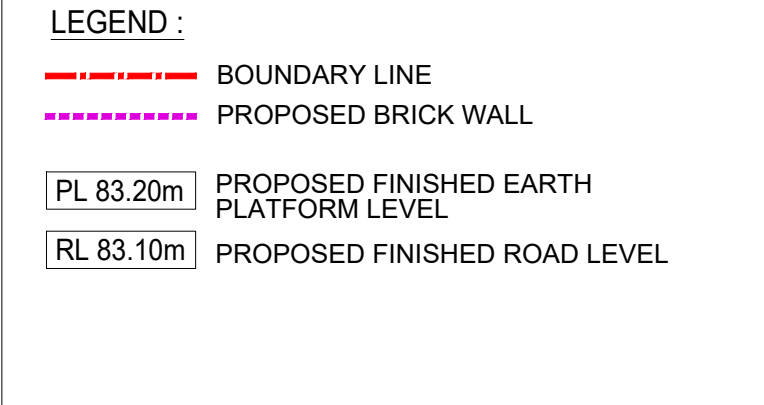
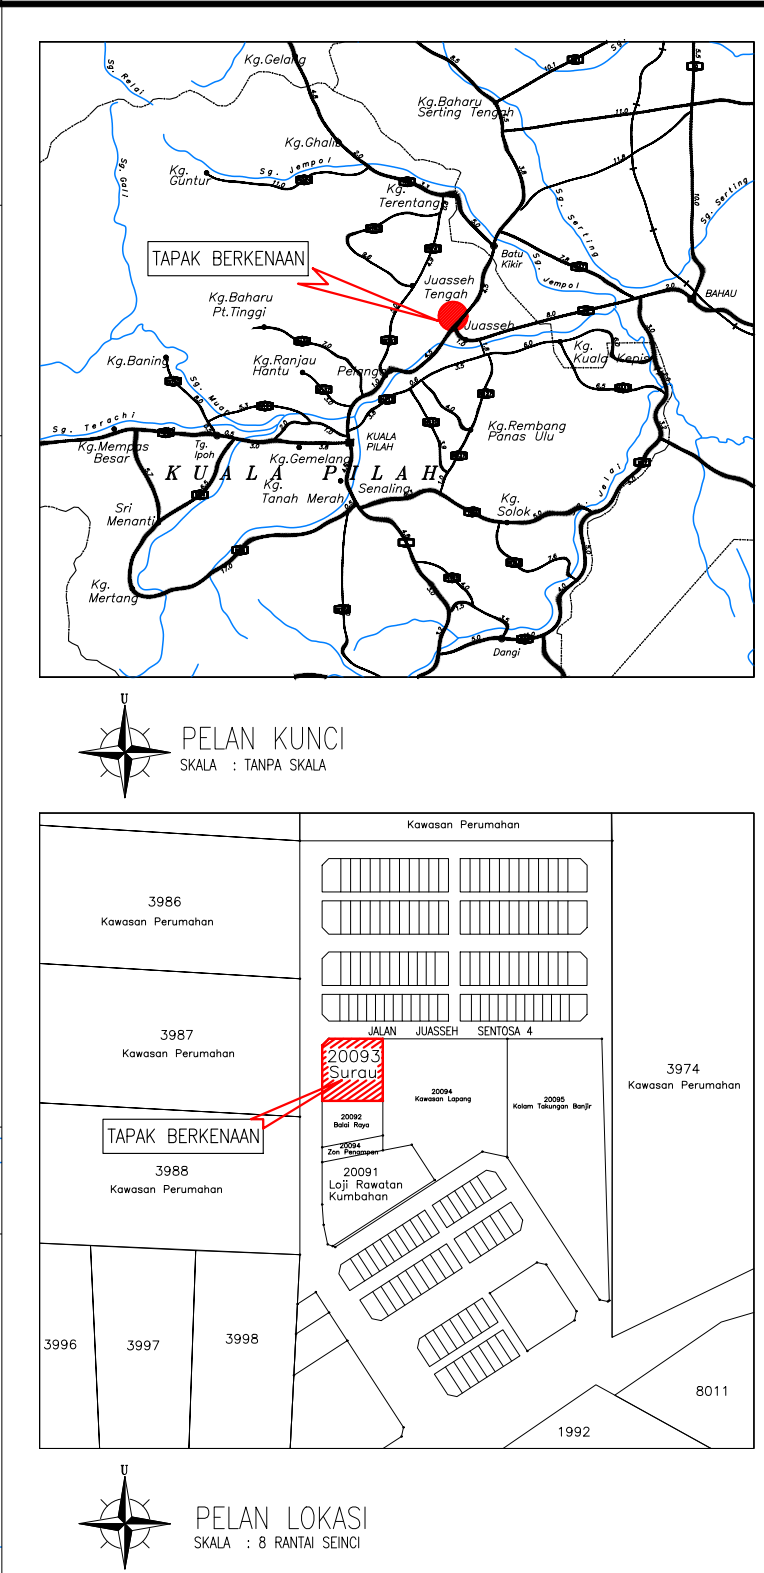


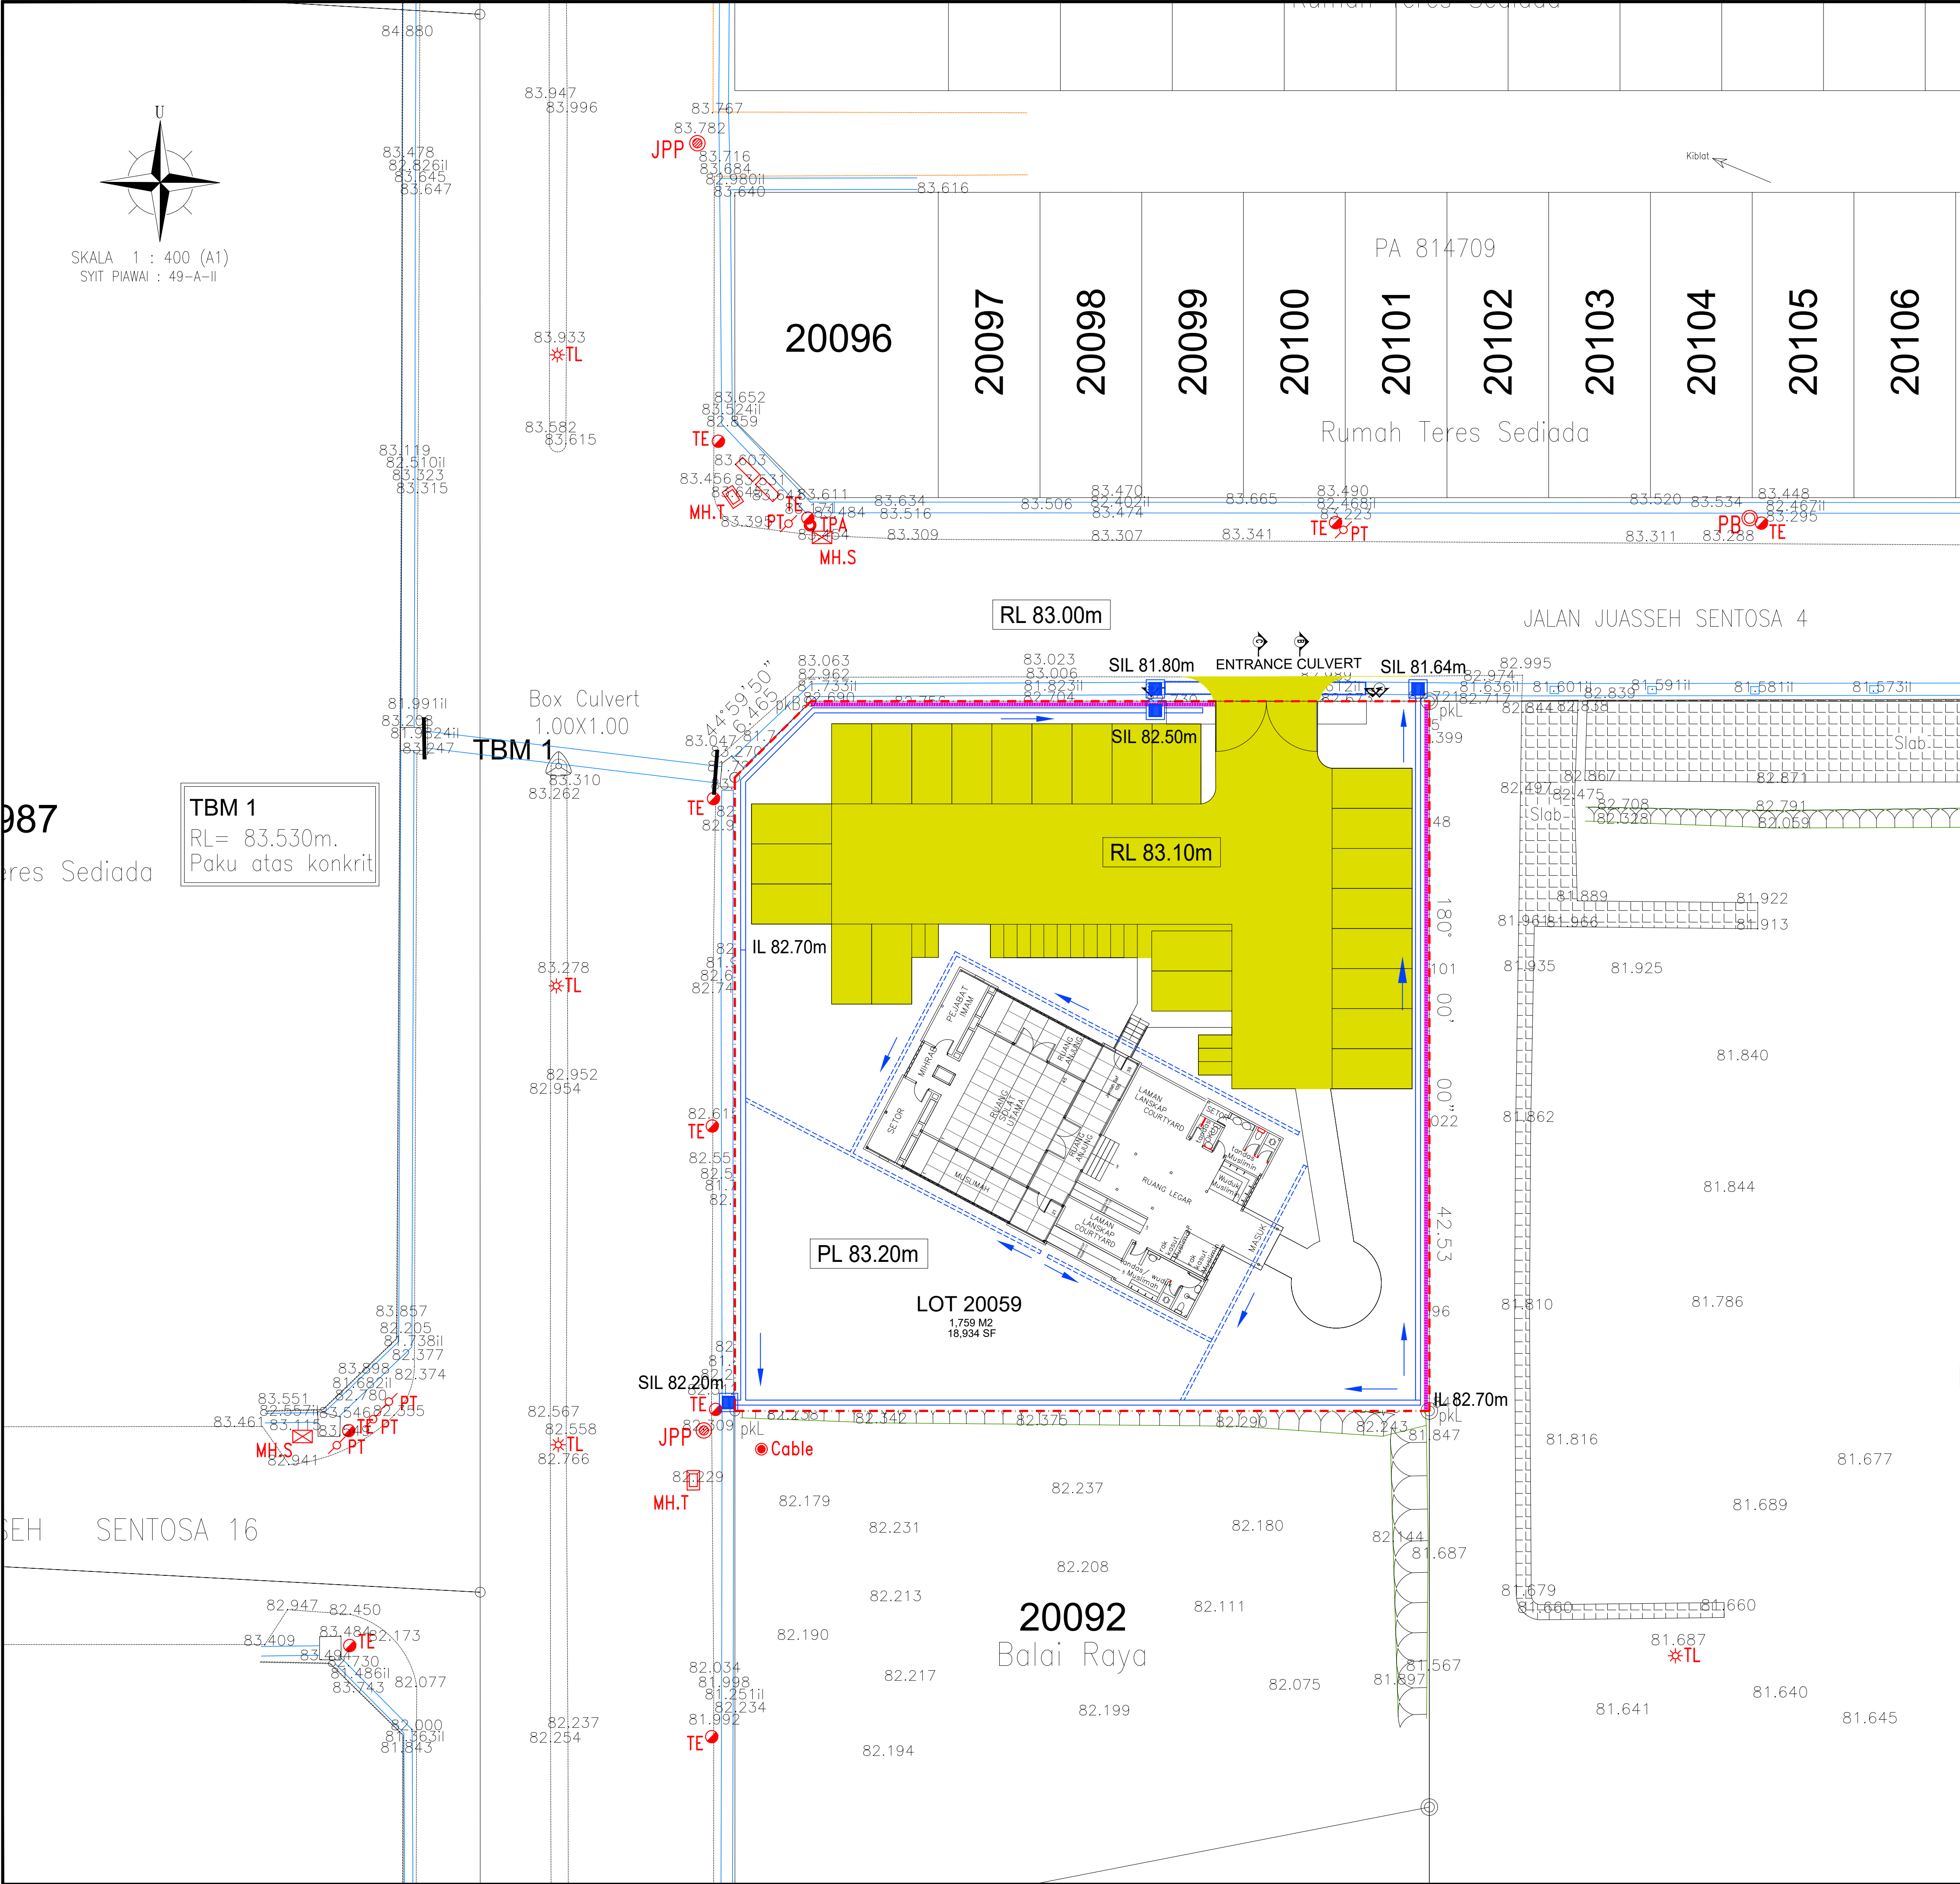

NO. FAIL (KEGUNAAN PEJABAT)

COP KELULUSAN (KEGUNAAN PEJABAT)

BIL	TARIKH	PINDAAN

TAJUK PERMOHONAN :

CADANGAN MEMBINA 1 UNIT SURAU 1 TINGKAT DIATAS LOT 20093, TAMAN JUASSEH SENTOSA, PEKAN JUASSEH, DAERAH KUALA PILAH, NEGERI SEMBILAN DARUL KHUSUS UNTUK TETUAN JABATAN HAL EHWAL AGAMA ISLAM NEGERI SEMBILAN

TAJUK LUKISAN :

ROAD AND DRAIN
KEY PLAN, LOCATION PLAN AND LAYOUT PLAN

PEMILIK :

"Saya bersetuju bertanggung jawab sekiranya berlaku kerosakan kepada bangunan di lot sebelah-menjebelah akibat dari kerja-kerja dalam permohonan ini."

JABATAN HAL EHWAL AGAMA ISLAM KUALA PILAH NEGERI SEMBILAN

PEGAWAI AGAMA DAERAH : HARDI BIN MOHAMAD SADALI
NO. KIP : 750906-10-5965
NO TEL : 06-4821029
EMAIL : paidkuatpilah.jheains@ns.gov.my
ALAMAT : JHEAINS Kuala Pilah, 70200 Kuala Pilah Negeri Sembilan

JURUTERA PERUNDING :

JURUTERA BUDIMAN J B SENDIRIAN BERHAD

73B & 75B, Jalan SS 21/37, Damansara Utama, 47400 Petaling Jaya, Selangor Darul Ehsan, Tel: 03-7727 2515 Fax: 03-7727 7606 Email: juruterabudiman@gmail.com (Company No. 235335-P)

TANDATANGAN JURUTERA BERTUALIAH

I hereby certify that these works have been designed by me in accordance with sound engineering practice and that I take full responsibility for the design and proper performance of the same.

JURUTERA BUDIMAN SDN.BHD. (235335-P)

Ir. MOHD NASPI BUSTAMAN C110264 MALAYSIA

Perang

Scale : 1:200 (A1)

Date : DECEMBER 2025

Drawn By : SMK

Designed By : MI

Checked By : Ir Shahrizal

Approved By : Ir Mohd Napi

DRAWING NO. : SJ/RD/LP/01

SUBMISSION DRAWING