




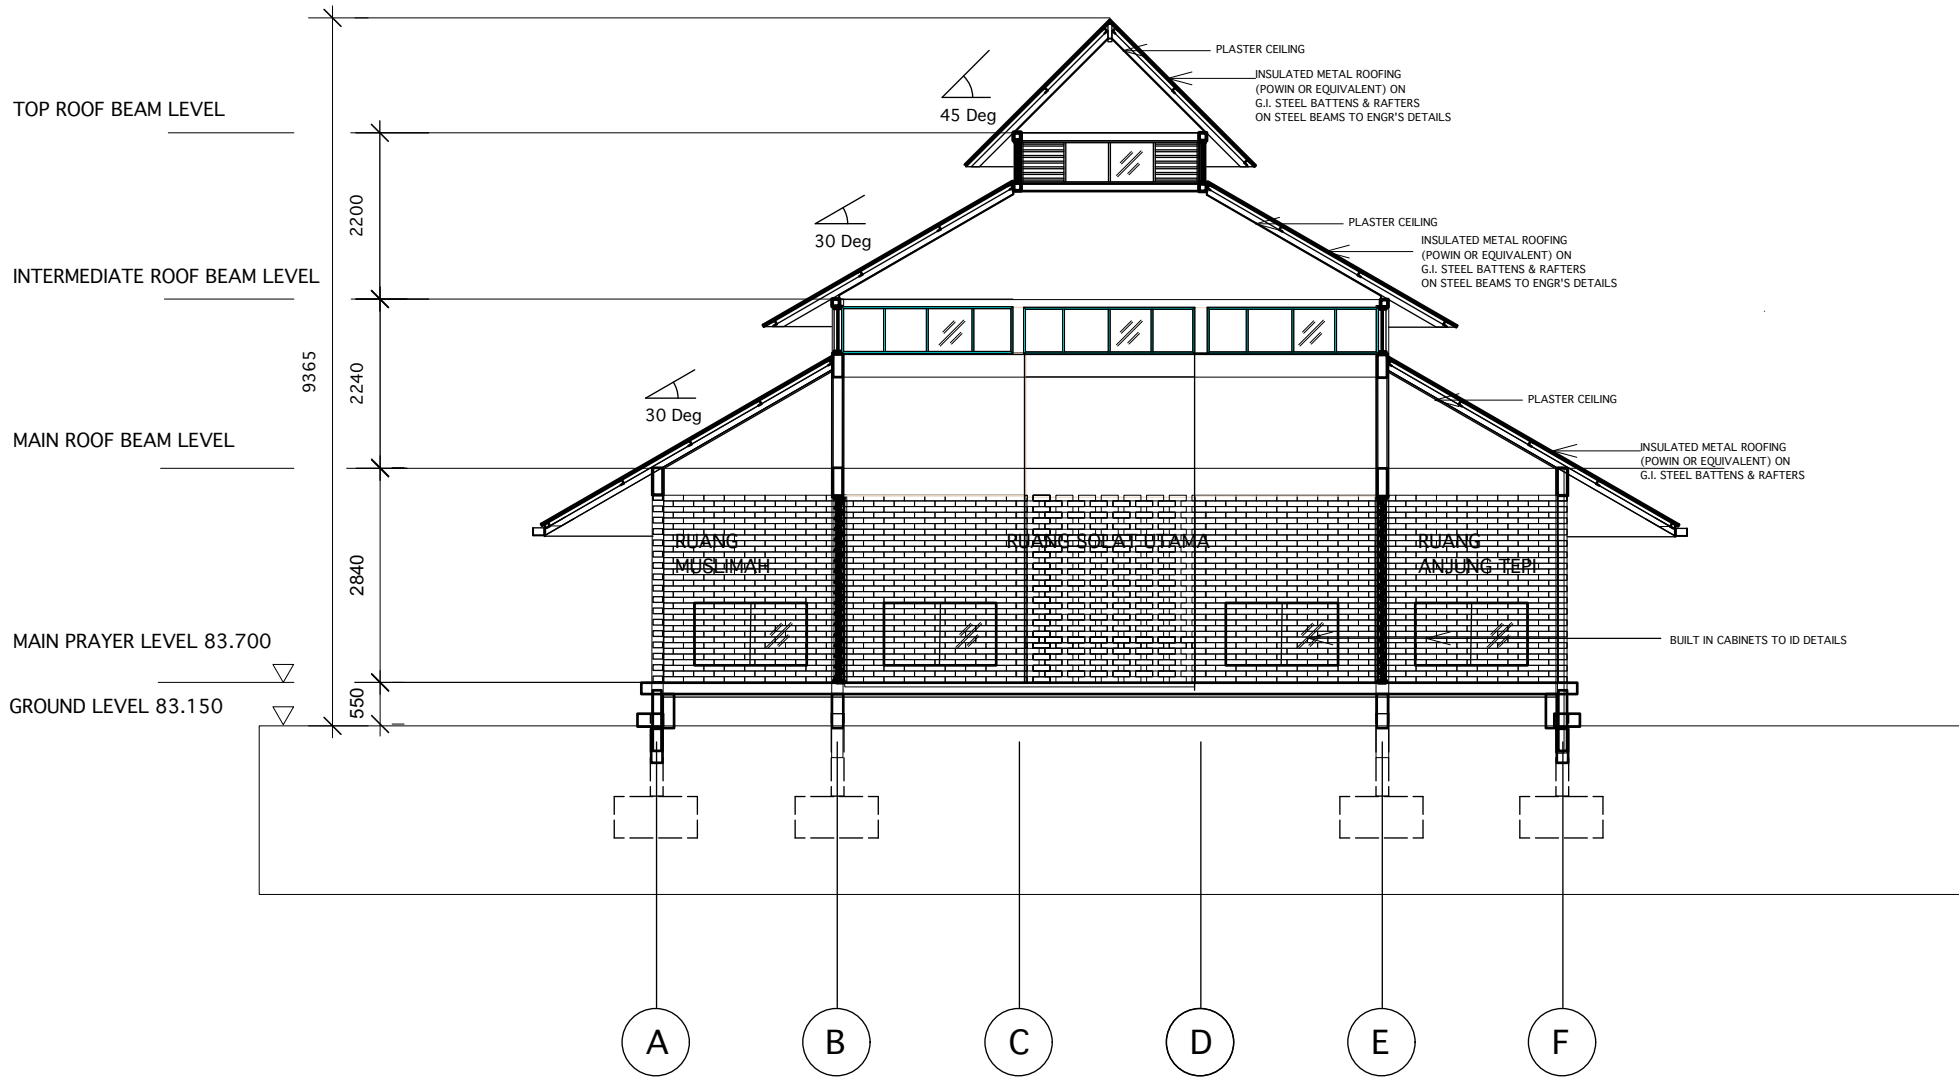


SECTION A-A

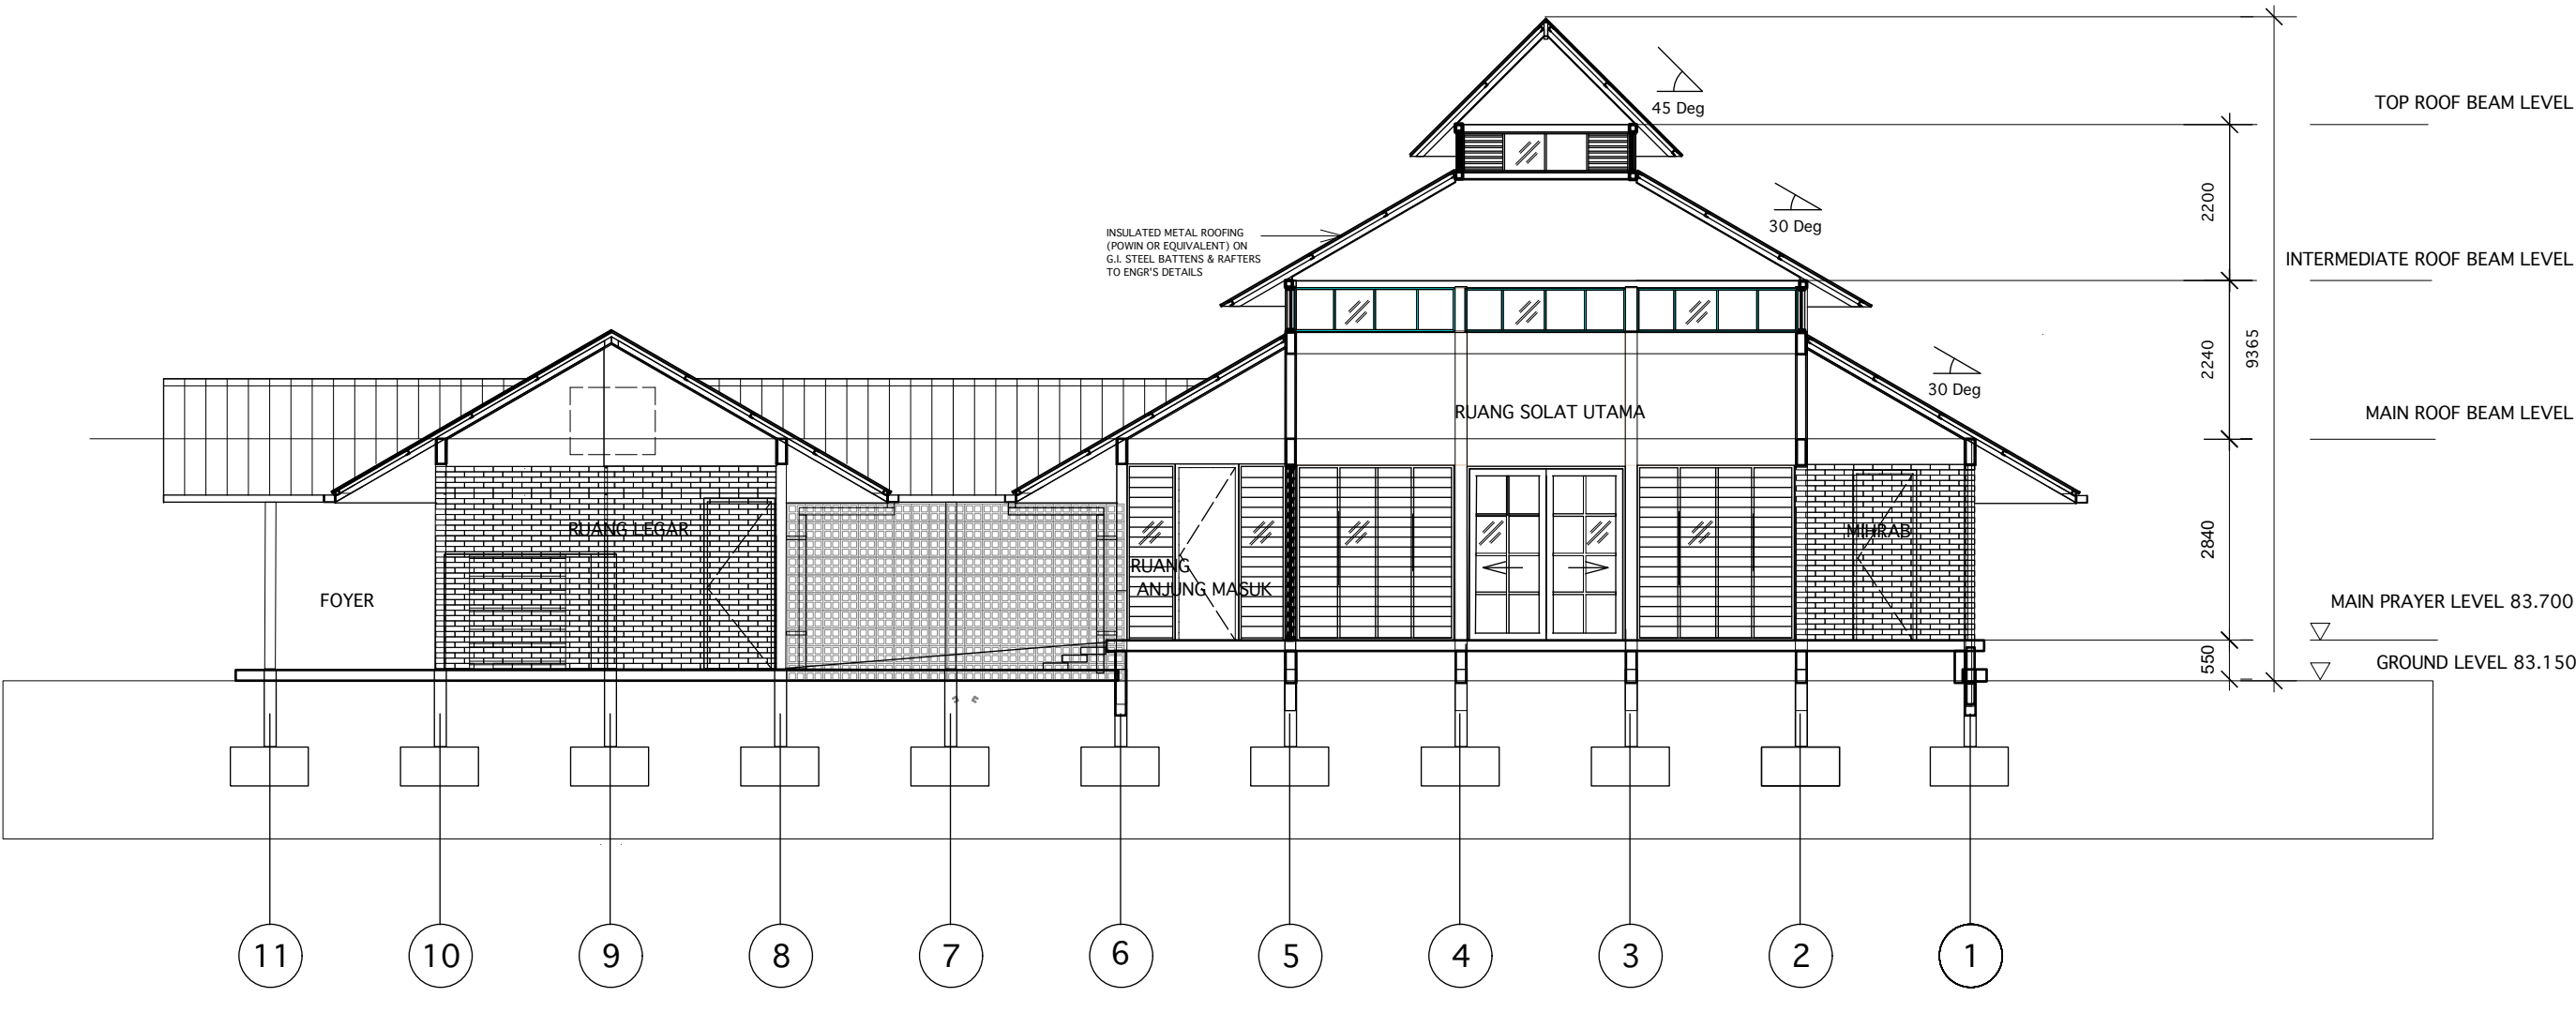


SECTION C-C

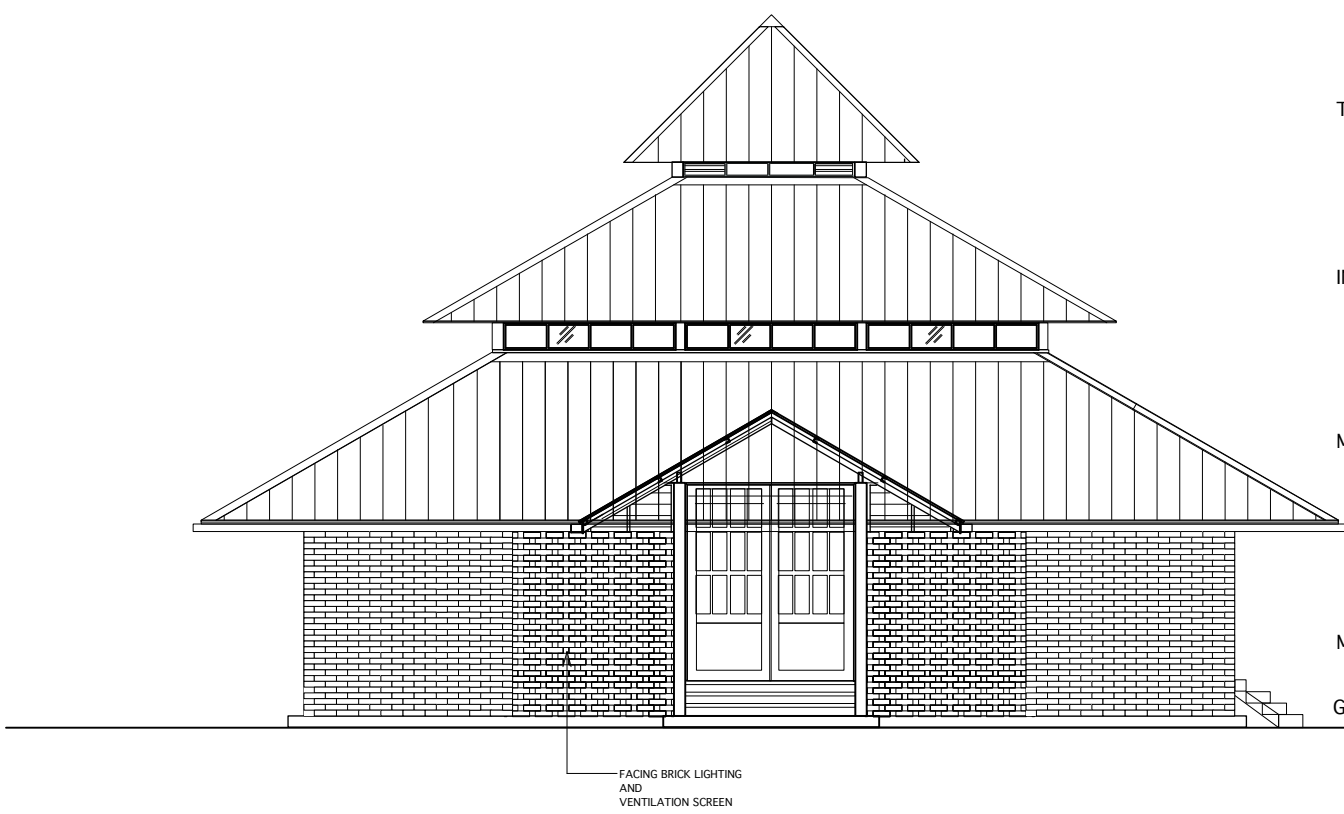


EAST ELEVATION

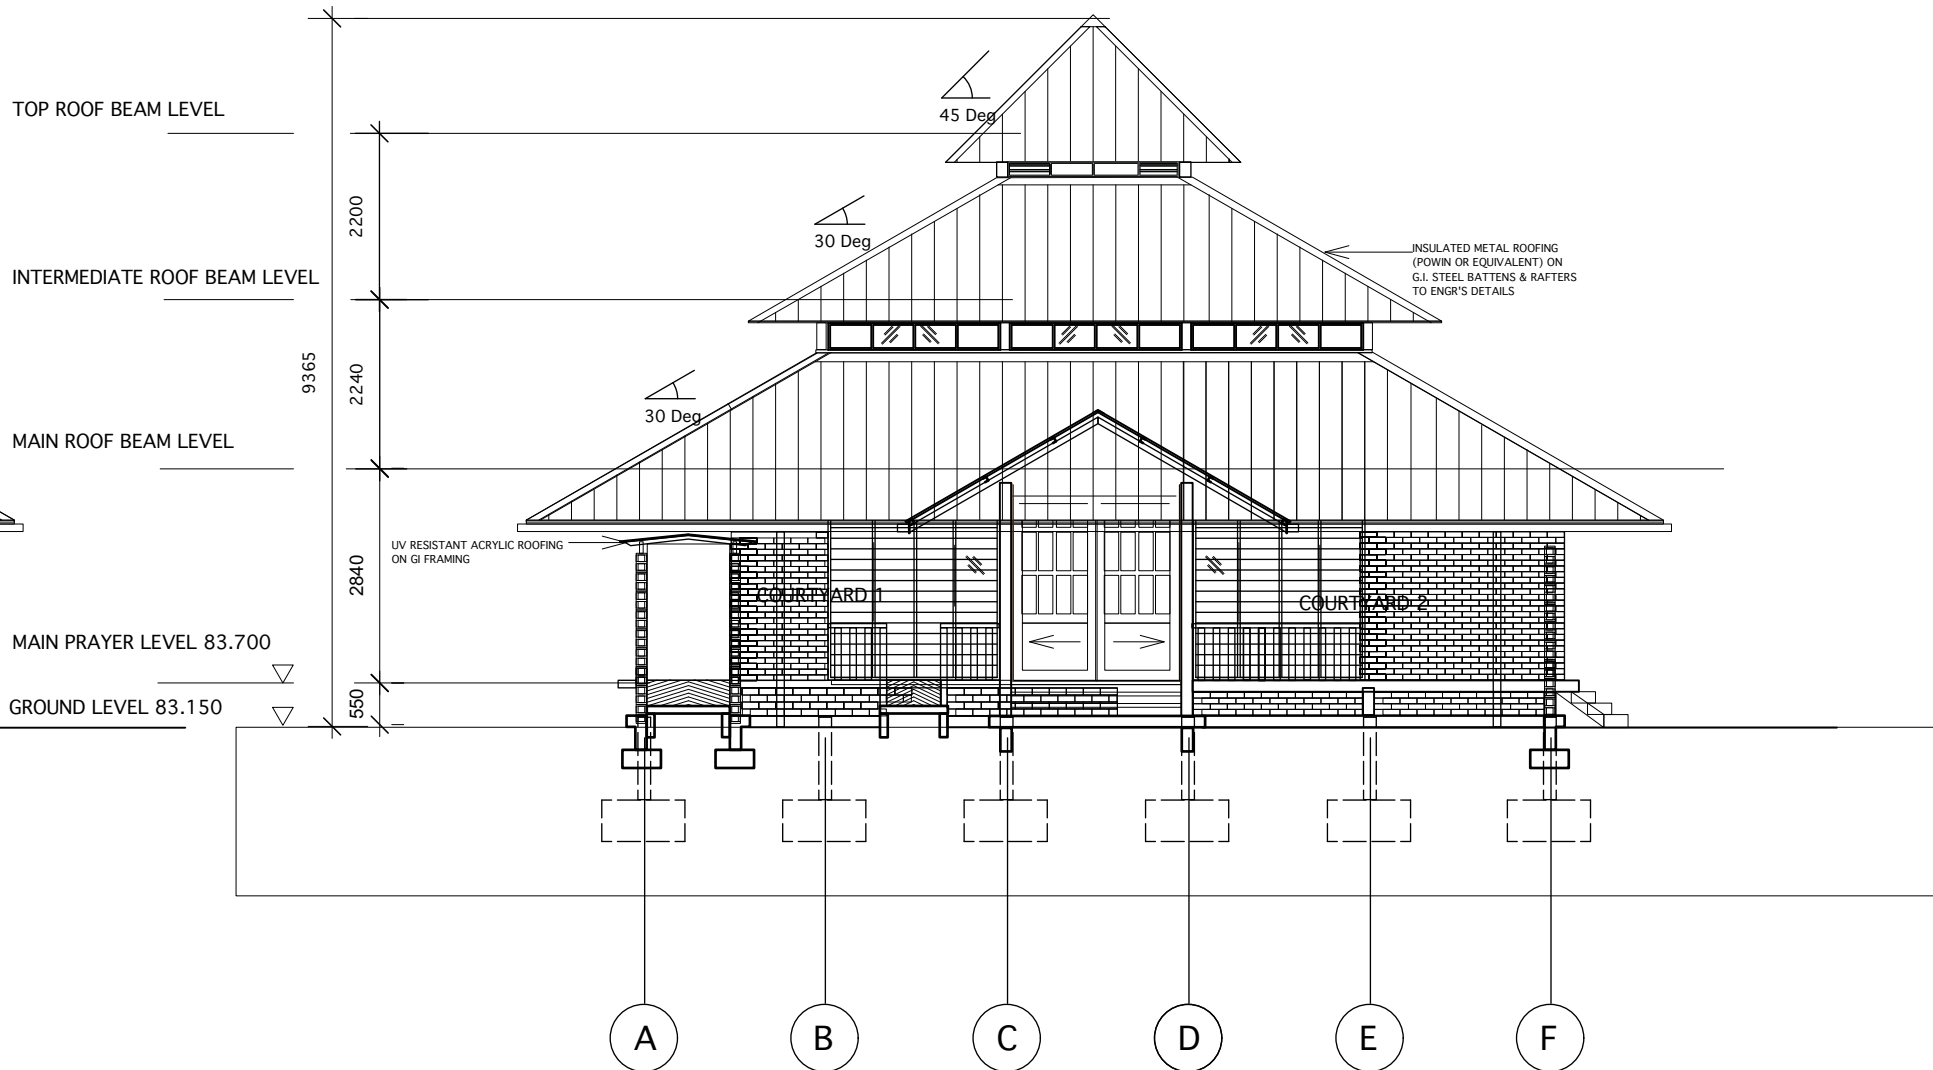


SECTION B-B

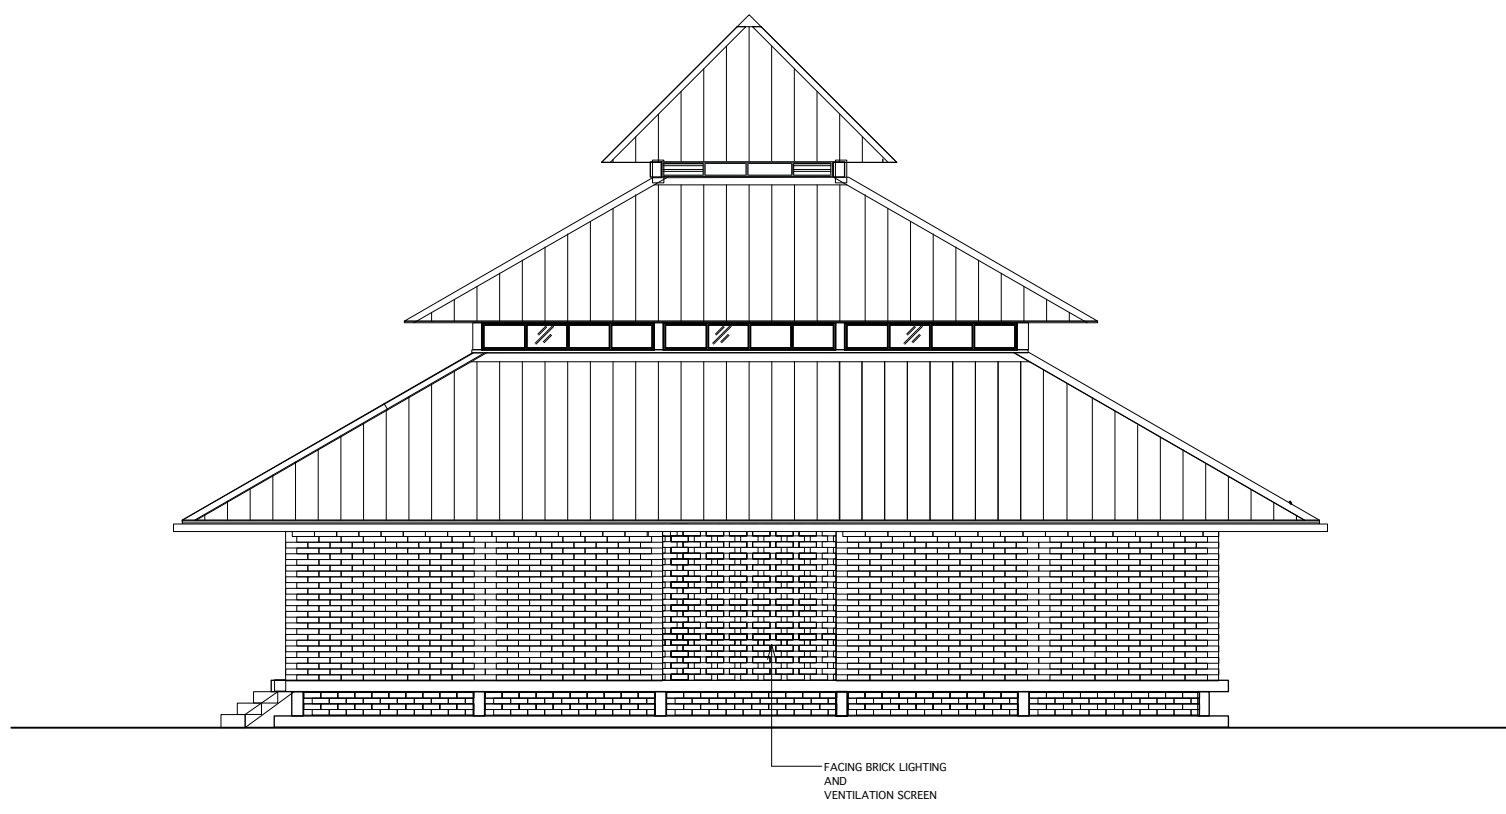

WEST ELEVATION

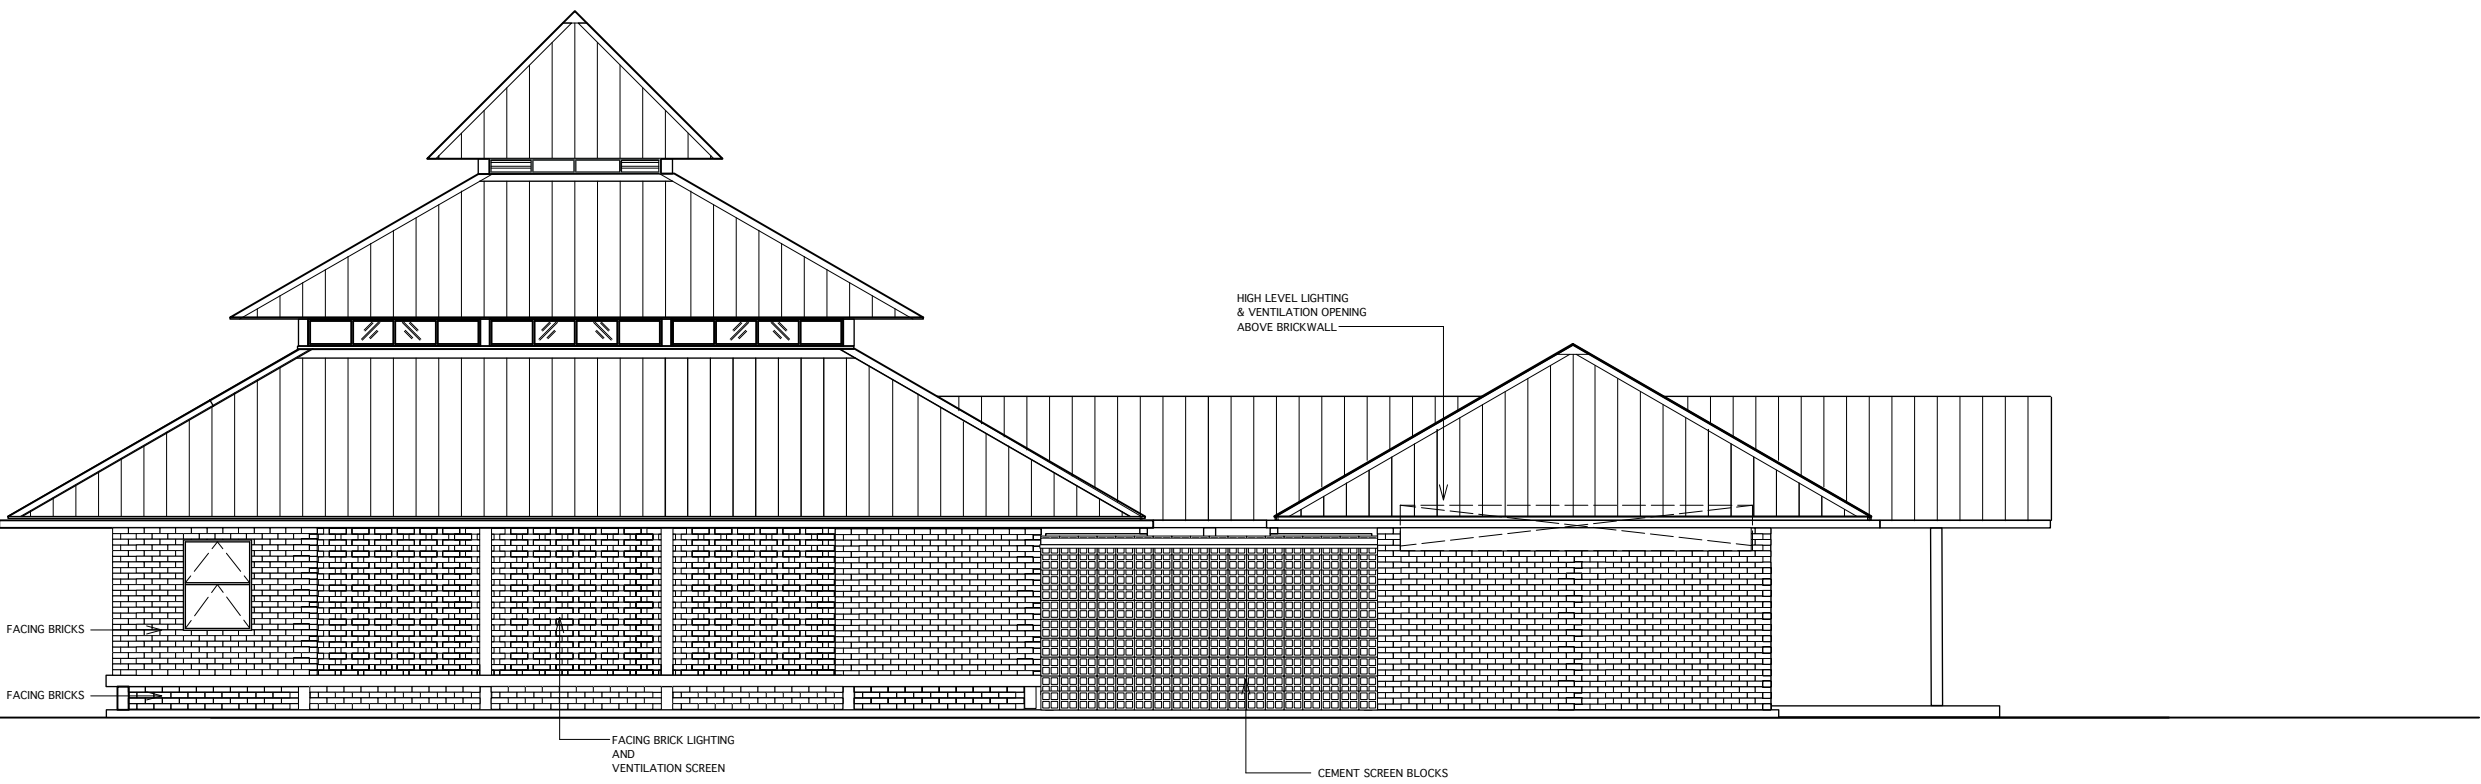

SOUTH ELEVATION

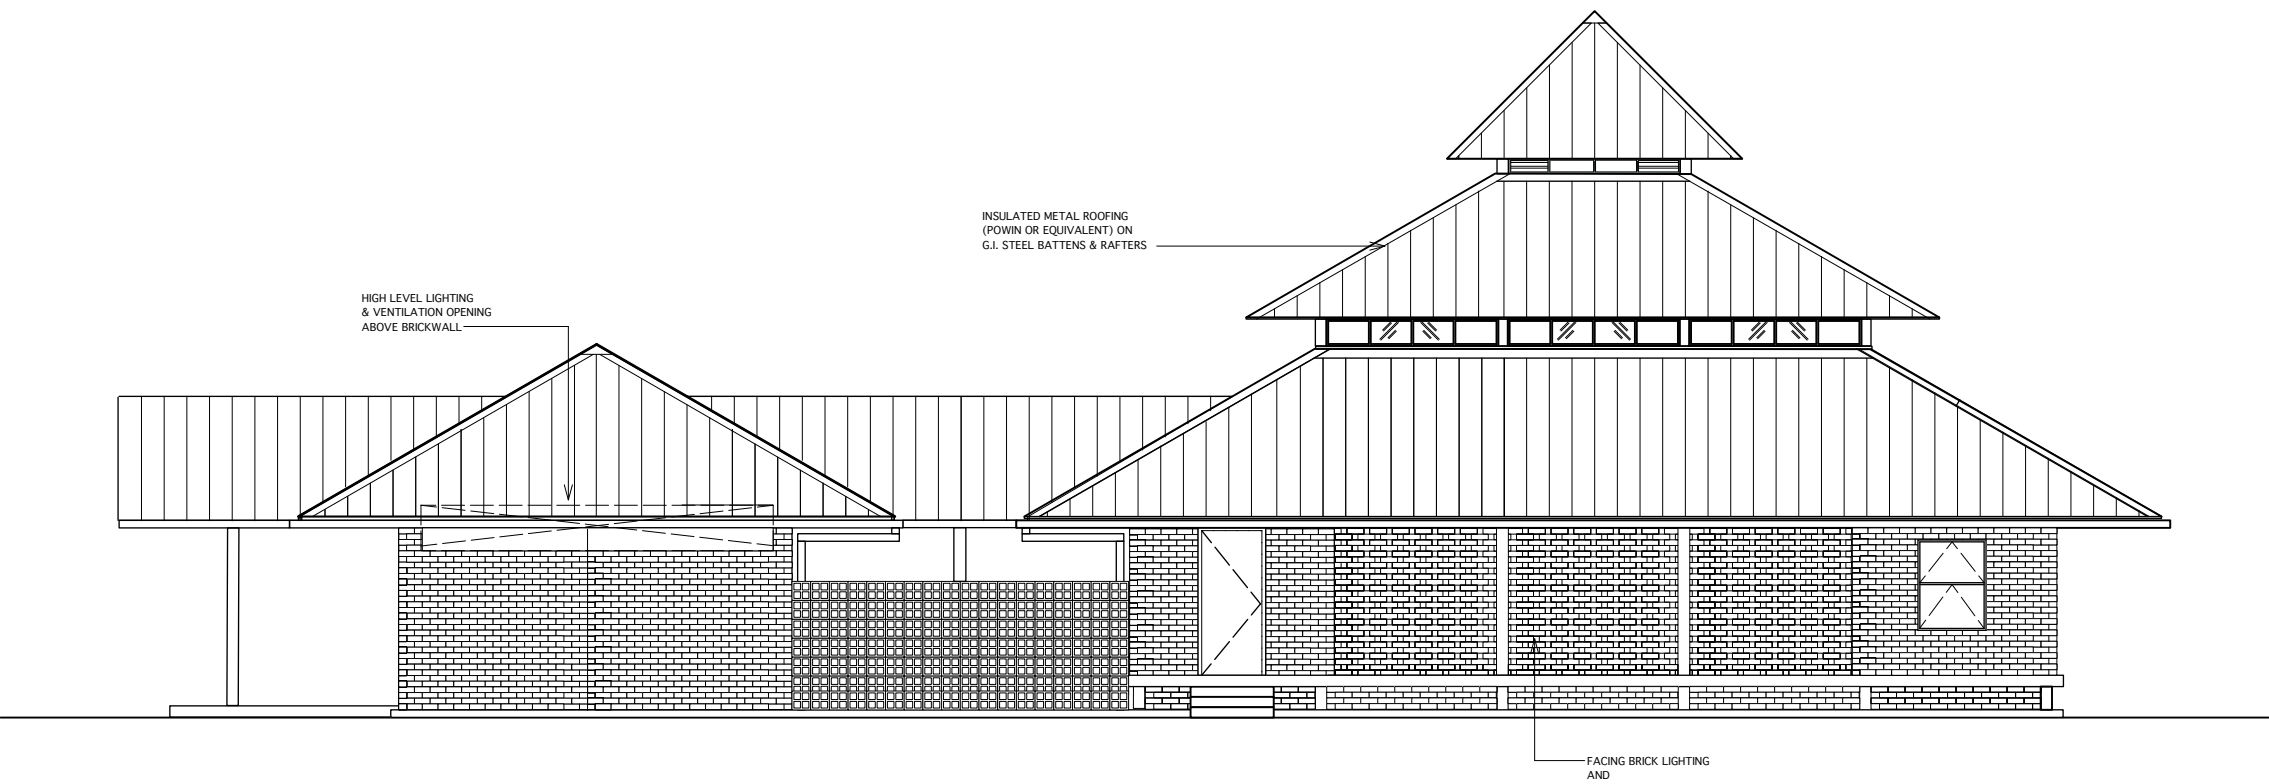

NORTH ELEVATION

NOTE:
-ALL BRICKS TO BE SELECTED TAIWAN KILN BRICKS SUPPLIED IN PALLETS TO SITE AND PROTECTED
-ALL BRICKWORK TO BE IN NEAT & CLEANED OF SLURRY FAIRFACE CONSTRUCTION, WITH MOCK UP TO BE APPROVED BY ARCHITECT
- ALL BRICKWORK & BREEZE BLOCKS UNLESS PLASTERED TO BE PROTECTED WITH 3 COATS OF SISSONS MATT WATERPROOF SILICON SEALANT INSIDE AND OUTSIDE

NO FILE RUJUKAN :

UNTUK KEGUNAAN MDKP

TAJUK PROJEK:

CADANGAN MEMBINA 1 UNIT SURAU 1 TINGKAT
DIATAS LOT 20093,
TAMAN JUASSEH SENTOSA,
PEKAN JUASSEH, DAERAH KUALA PILAH
NEGERI SEMBILAN DARUL KHUSUS
UNTUK
TETUAN JABATAN HAL EHWAL AGAMA ISLAM
NEGERI SEMBILAN

TANDATANGAN PEMILIK TANAH / BANGUNAN :


"Saya/Kami bersetuju untuk mematuhi pelan bangunan yang diluluskan. Dengan ini saya/kami bersetuju untuk dikenakan tindakan undang-undang yang berkaitan dengannya jika gagal mematuhiya".

JABATAN HAL EHWAL AGAMA ISLAM
KUALA PILAH NEGERI SEMBILAN
PEKAN JUASSEH
NO. KIP : 750908-10-5665
NO. TEL : 06-4821109
EMAIL : padkualapilah.jheains@ns.gov.my
ALAMAT : JHEAINS Kuala Pilah, 70200 Kuala Pilah
Negeri Sembilan

ARKITEK:
"SAYA MEMPERAKUI BAHAWA BUTIRAN - BUTIRAN DI DALAM PELAN - PELAN INI ADALAH MENURUT KEHENDAK - KEHENDAK UNDANG - UNDANG KECIL BANGUNAN SERAGAM (PBTNS) 1986 DAN SAYA SETUJU TERIMA TANGGUNGJAWAB PENUH DENGAN SEWAJARNYA"



Ar. Wan Azami Bin Hamzah
ARKITEK PROFESIONAL
No Pendaftaran LAM: A/W 56

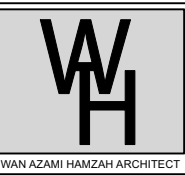

NO. 2 JALAN MERAH PELANGI SATU
U9/19a KELAB GOLF MONTEREZ
40150 SHAH ALAM, SELANGOR MALAYSIA
NO. TEL : 019 2063 100 / 012 324 0914
EMAIL : wah.architect@gmail.com

STATUS LUKISAN :

☐ PRELIMINARY ☐ SUBMISSION ☒ CONSTRUCTION
☐ INFORMATION ☒ TENDER ☐ DEVELOPMENT ORDER

TAJUK LUKISAN:

SECTIONS AND ELEVATIONS

DILUKIS OLEH	JW
DISEMAK OLEH	WA
TARIKH	DEC 2025
SKALA	1:100
NO DWG.	SJS/BP/003