

NO FILE RUJUKAN :

UNTUK KEGUNAAN MDKP

TAJUK PROJEK:

CADANGAN MEMBINA 1 UNIT SURAU 1 TINGKAT
DIATAS LOT 20093,
TAMAN JUASSEH SENTOSA,
PEKAN JUASSEH, DAERAH KUALA PILAH
NEGERI SEMBILAN DARUL KHUSUS
UNTUK
TETUAN JABATAN HAL EHWAL AGAMA ISLAM
NEGERI SEMBILAN

TANDATANGAN PEMILIK TANAH / BANGUNAN :

"Saya/Kami bersetuju untuk mematuhi pelan bangunan yang diluluskan. Dengan ini saya/kami bersetuju untuk dikenakan tindakan undang-undang yang berkaitan dengannya jika gagal mematuhiya".

JABATAN HAL EHWAL AGAMA ISLAM
KUALA PILAH NEGERI SEMBILAN
REGIONAL AGAMA DAERAH : HARDI BIN MOHAMAD SADALI
NO. K/P : 750098-10-5965
NO TEL : 06-4621029
EMAIL : padkualapilah.jheains@ns.gov.my
ALAMAT : JHEAINS Kuala Pilah, 70200 Kuala Pilah
Negeri Sembilan

ARKITEK:

"SAYA MEMPERAKUI BAHAWA BUTIRAN - BUTIRAN DI DALAM PELAN - PELAN INI ADALAH MENURUT KEHENDAK - KEHENDAK UNDANG - UNDANG KECIL BANGUNAN SERAGAM (PBTNS) 1986 DAN SAYA SETUJU TERIMA TANGGUNGJAWAB PENUH DENGAN SEWAJARNYA"



Ar. Wan Azami Bin Hamzah
ARKITEK PROFESIONAL
No Pendaftaran LAM: A/W 56



NO. 2 JALAN MERAH PELANGI SATU
U9/19a KELAB GOLF MONTEREZ
40150 SHAH ALAM, SELANGOR MALAYSIA
NO. TEL : 019 2063 100 / 012 324 0914
EMAIL : wah.architect@gmail.com

STATUS LUKISAN :

☐ PRELIMINARY ☐ SUBMISSION ☒ CONSTRUCTION
☐ INFORMATION ☒ TENDER ☐ DEVELOPMENT ORDER

TAJUK LUKISAN:

FLOOR PLAN, ROOF PLAN,
DOOR, WINDOW &
LIGHTING AND VENTILATION
SCHEDULES

DILUKIS OLEH JW

DISEMAK OLEH WA

TARIKH Dec 2025

SKALA 1:100


NO DWG. SJS/BP/002

WINDOW SCHEDULE

SYMBOL	SIZE (W)x(H) mm	DESCRIPTION
W1	900 X 1200	Top Hung Powder Coated Aluminium framed window with 8mm thk clear glass glazing
W2	2280 x 2400	Breezeway Altair Adjustable glass louvres with Tempered glass panels to manufacturer's specifications
W3	750 x 2400	Breezeway Altair Adjustable glass louvres with Tempered glass panels to manufacturer's specifications
W4	4650 x 600	High level Lighting and Ventilation opening only with no windows
W5	2250 x 600	High level Lighting and Ventilation opening only with no windows
W6	1150 x 600	High level Lighting and Ventilation opening only with no windows
BS1	2300 x 2400	Lighting and Ventilation opening by way of brick screen with average opening of 50% per panel

DOOR SCHEDULE

SYMBOL	SIZE (W)x(H)	DESCRIPTION
D1	900 X 2400	Solid Timber door to detail
D2	2300 X 2400	Powder coated Aluminium sliding doors with 10mm thk clear Tempered glass glazing to manuf spec
D3	1000 X 2400	Solid Timber door to detail

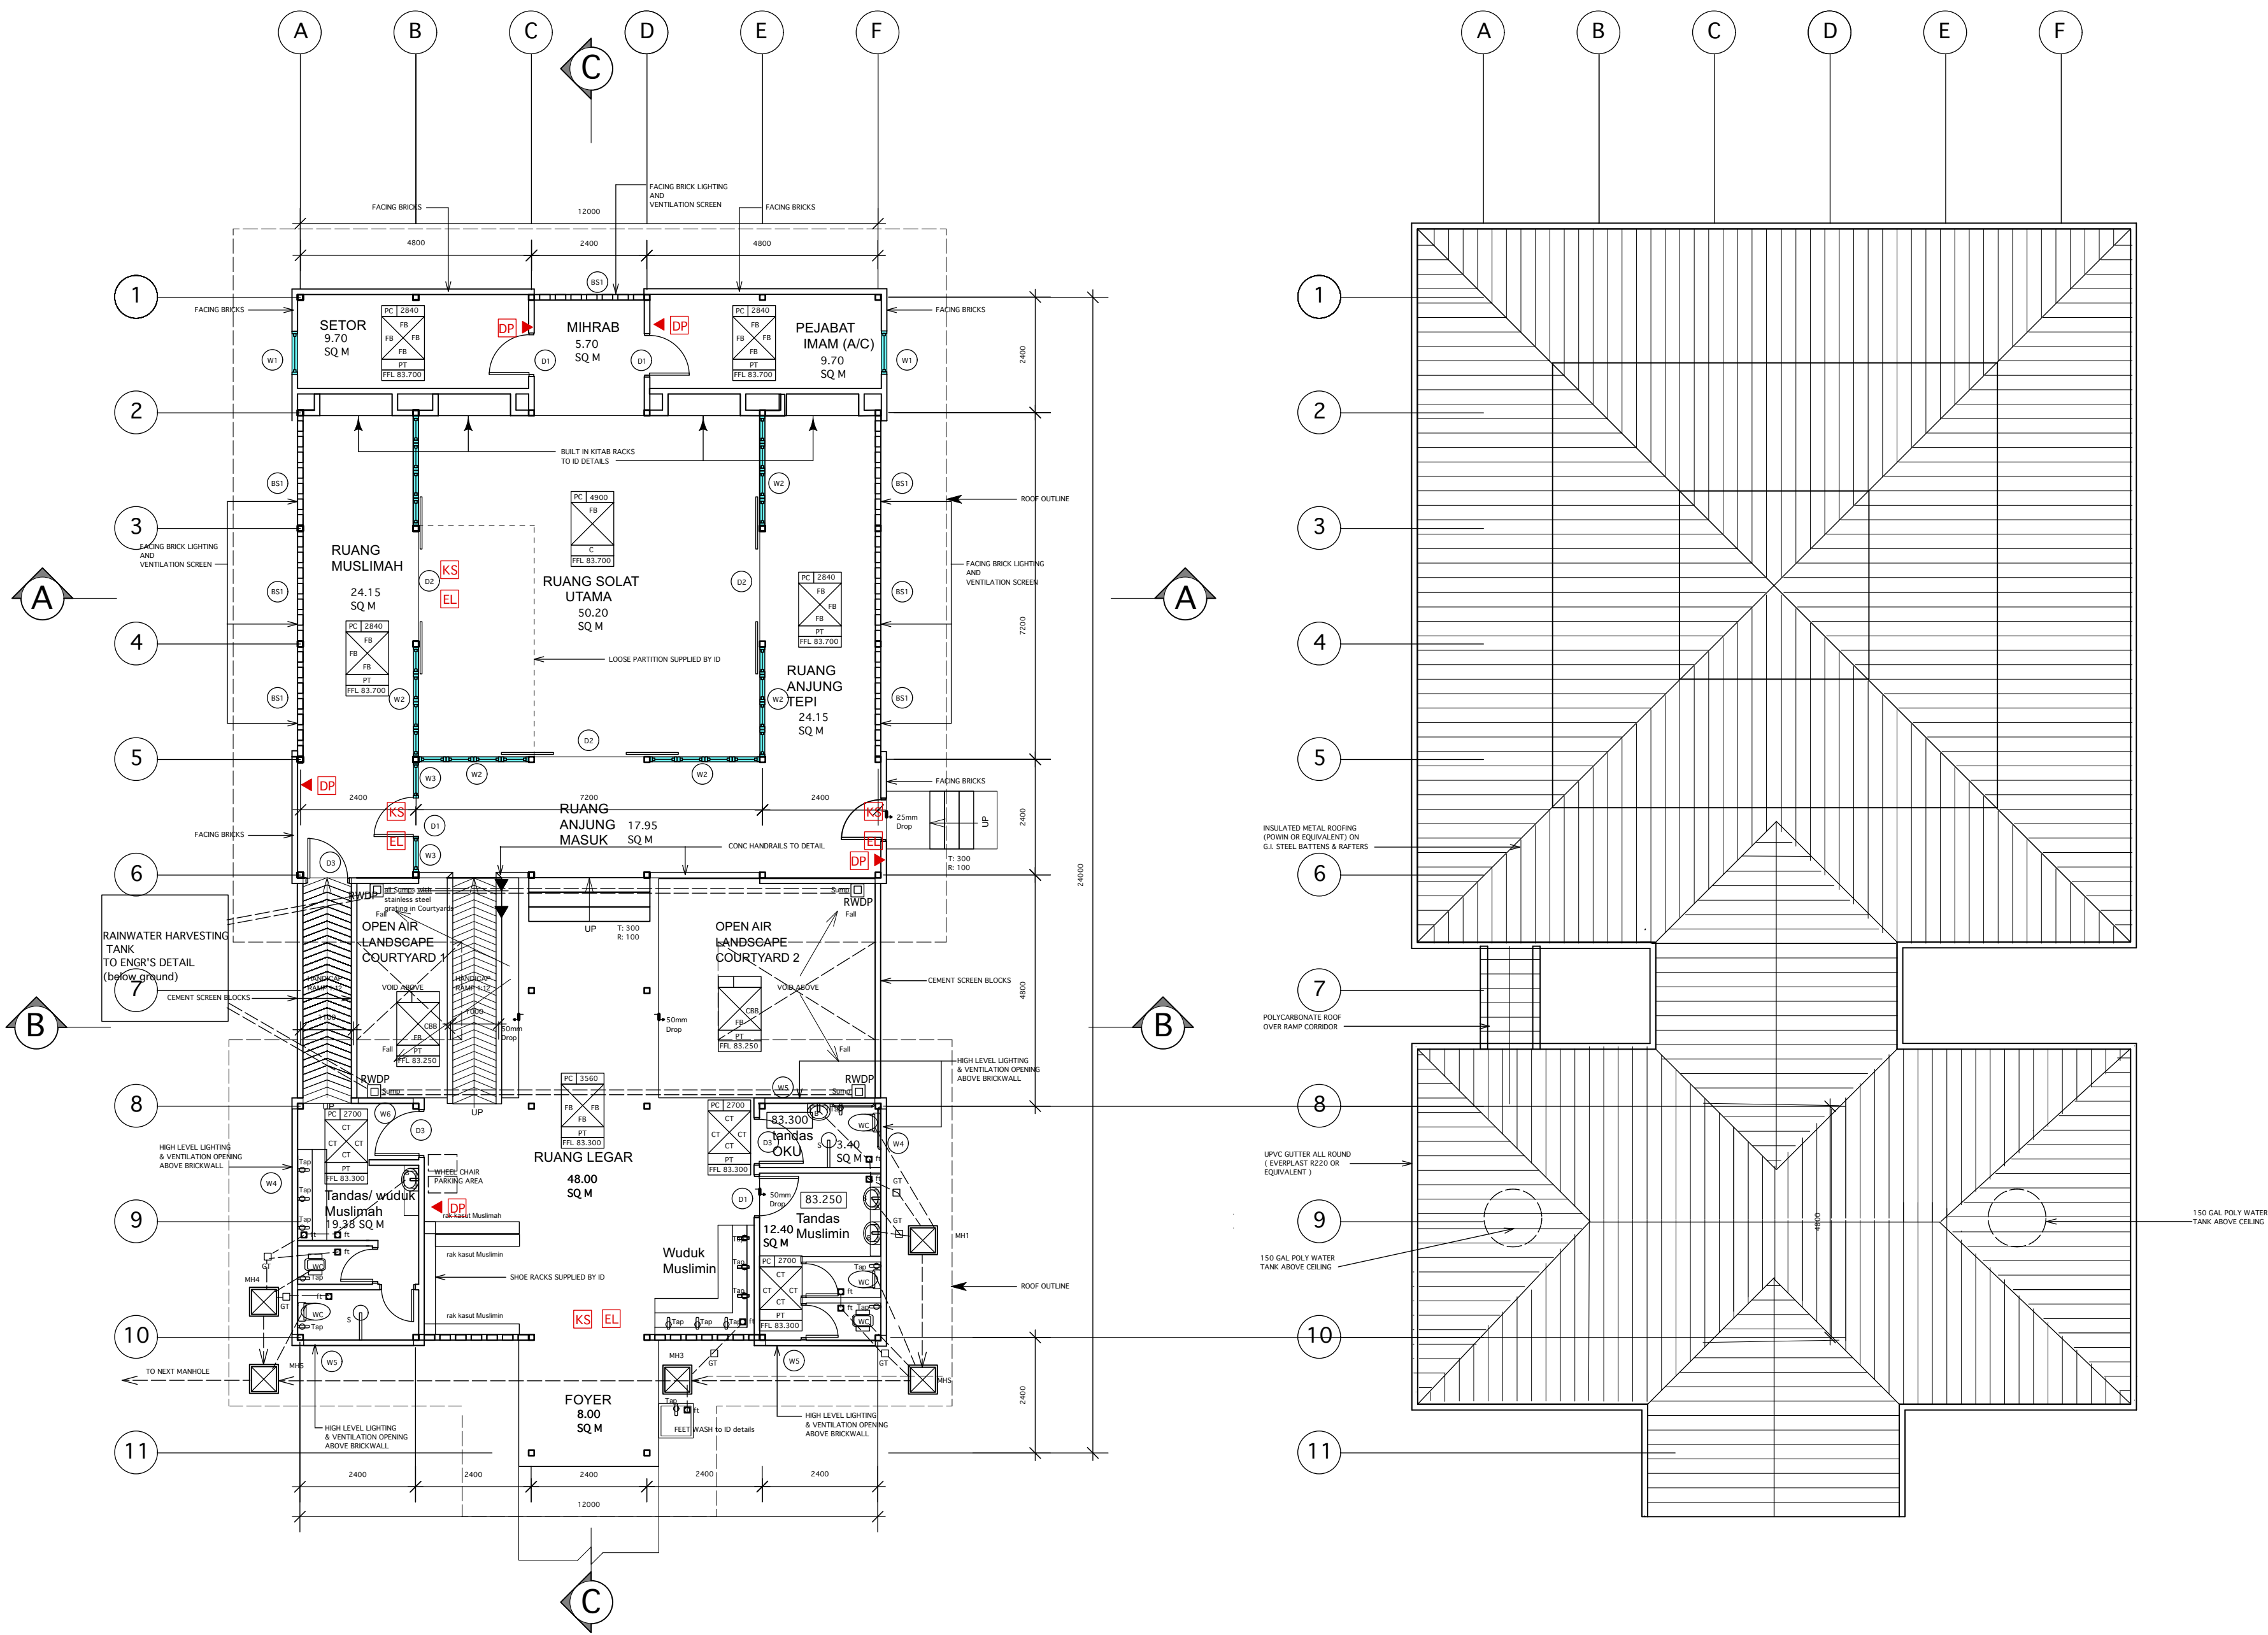

LEGEND

FINISHES REFERENCE (PETUNJUK KEMASAN BANGUNAN)																						
	CEILING FINISHES	<table><tr><td>X</td><td>XXX.XXX</td></tr><tr><td></td><td>X</td></tr><tr><td>X</td><td></td></tr><tr><td></td><td>X</td></tr><tr><td>X</td><td></td></tr><tr><td></td><td>X</td></tr><tr><td>X</td><td></td></tr><tr><td></td><td>X</td></tr><tr><td>FFL</td><td>XXX.XXX</td></tr></table>	X	XXX.XXX		X	X			X	X			X	X			X	FFL	XXX.XXX	CEILING HEIGHT	
X	XXX.XXX																					
	X																					
X																						
	X																					
X																						
	X																					
X																						
	X																					
FFL	XXX.XXX																					
	WALL FINISHES C		WALL FINISHES A																			
	WALL FINISHES D		WALL FINISHES B																			

