

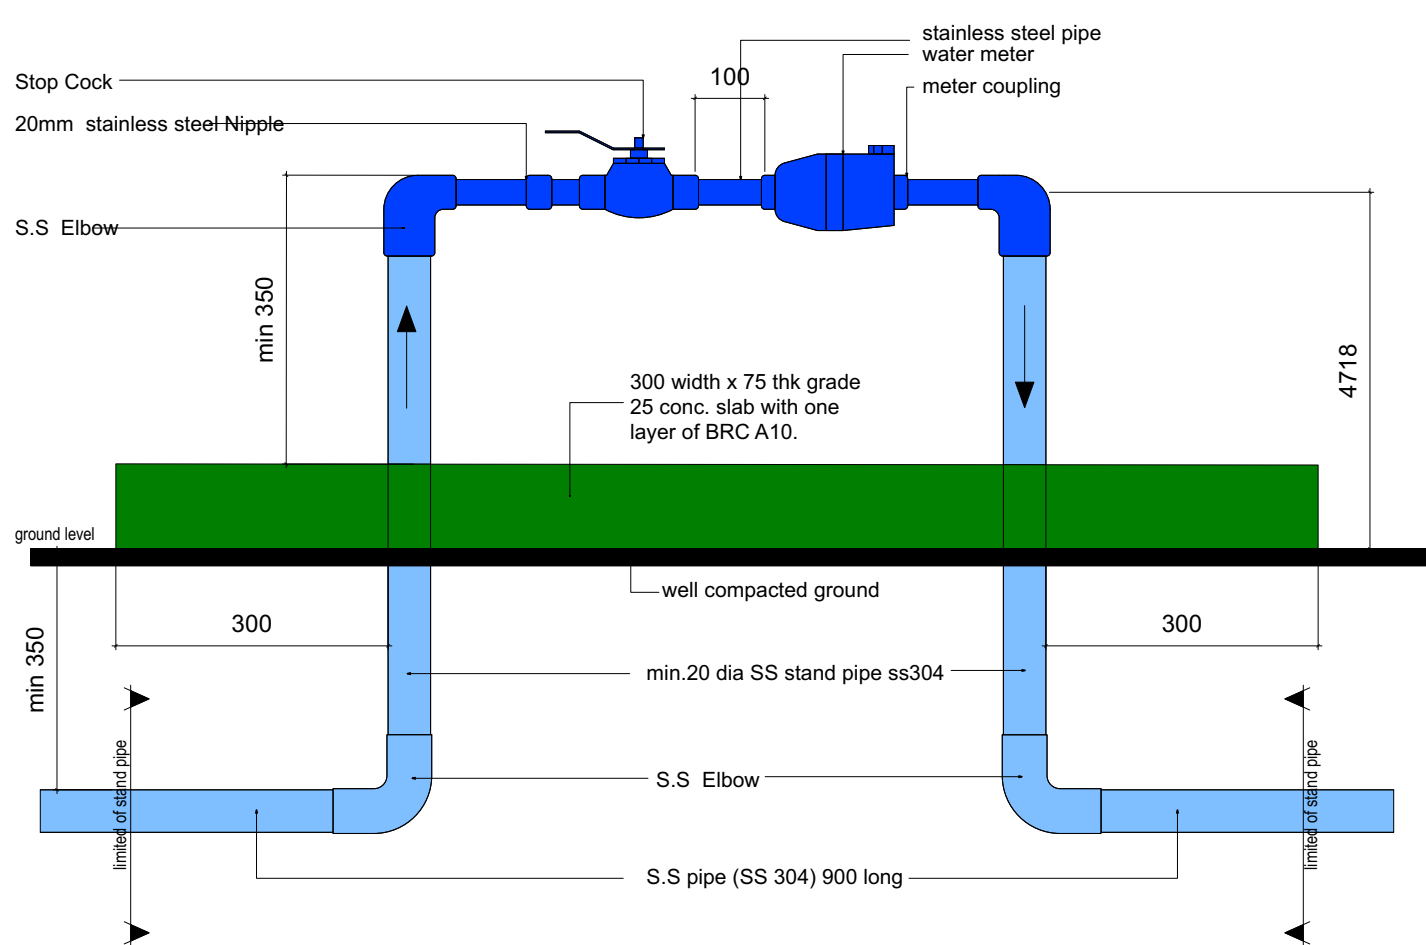
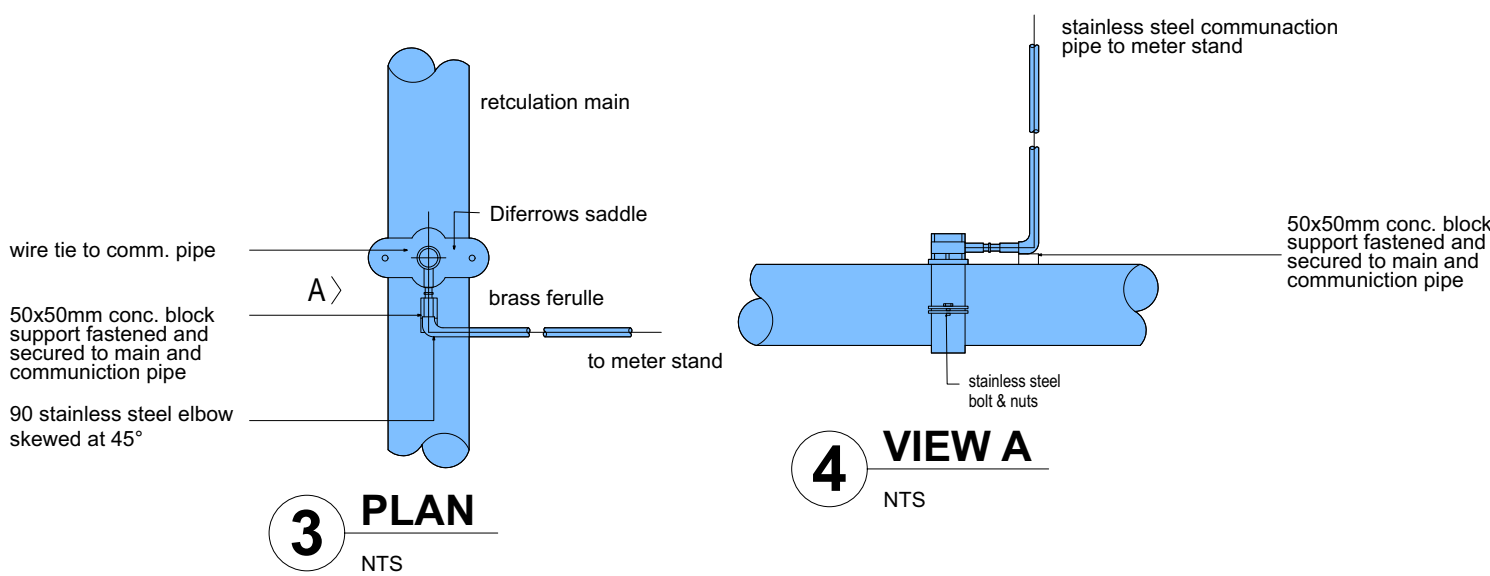


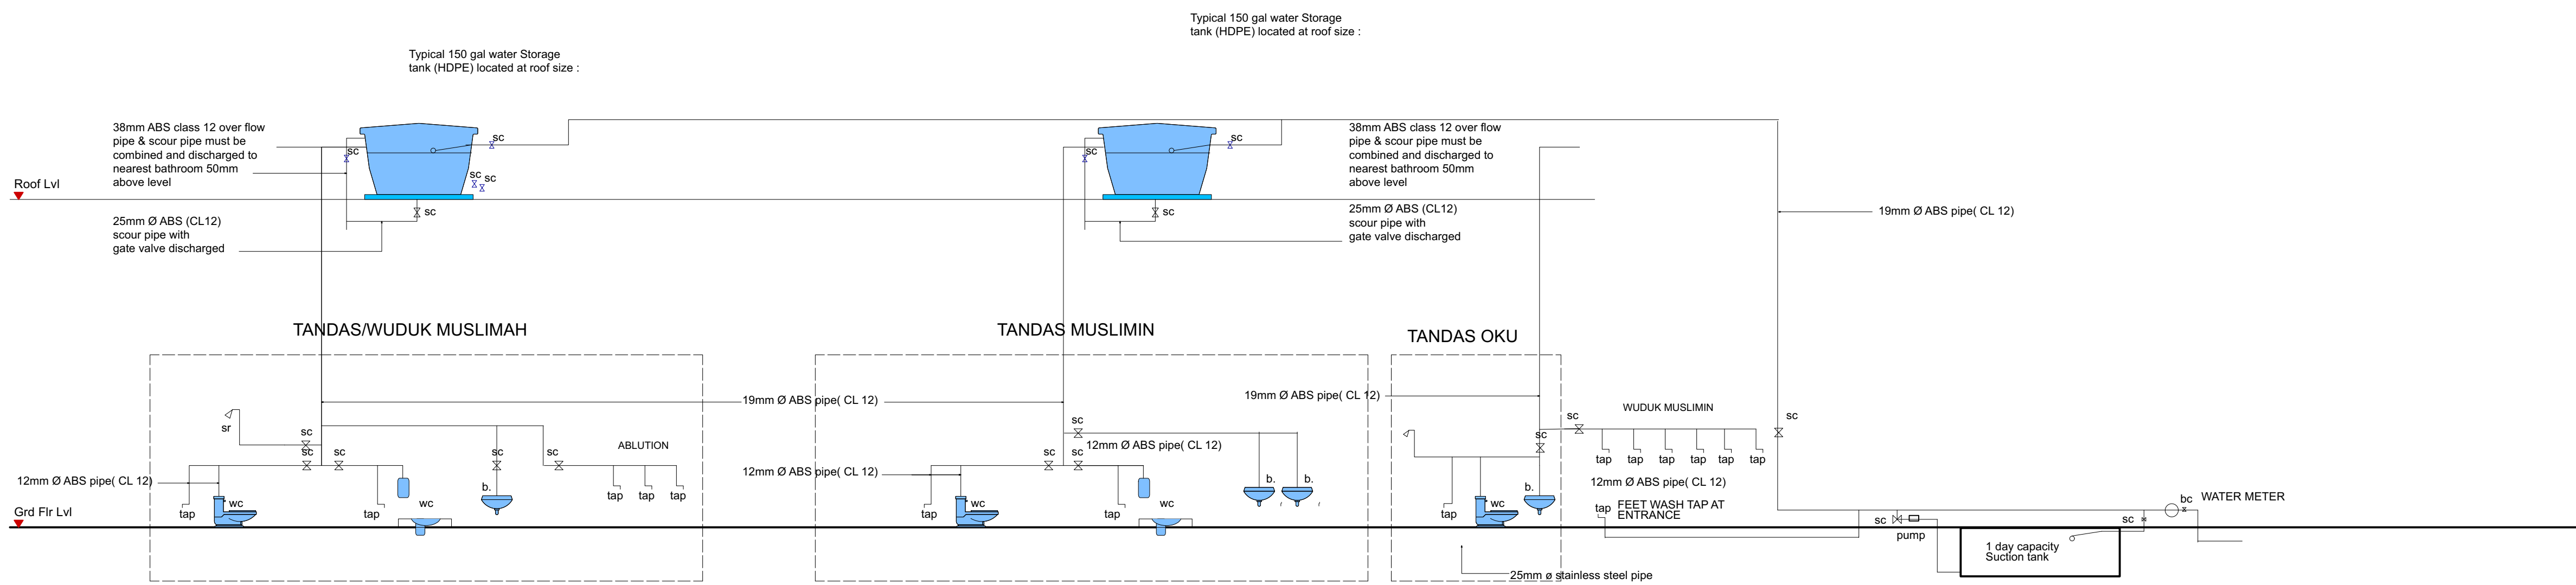

NOTE :

ALL FITTINGS SHALL BE OF STAINLESS STEEL

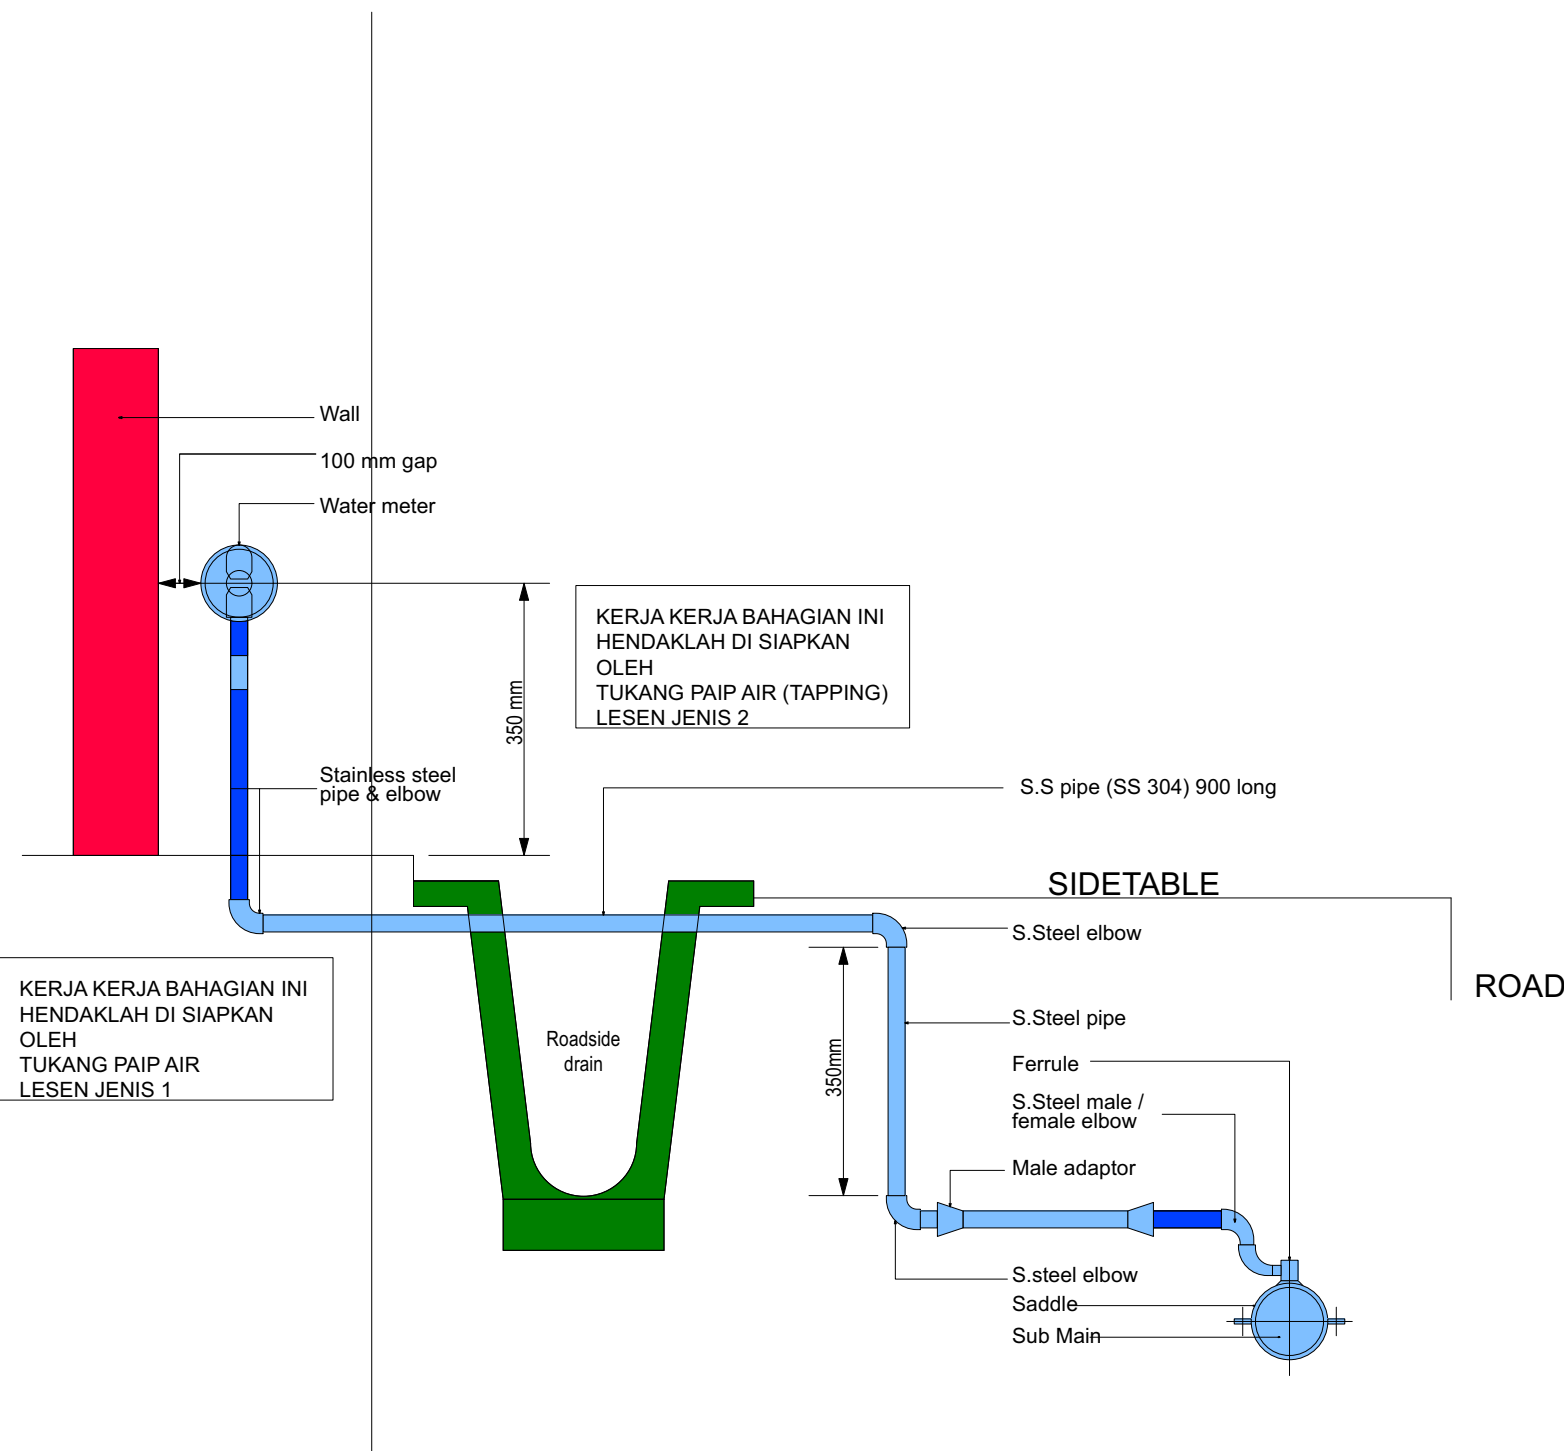

1 PELAN SUSUNATUR PLUMBING NTS

NO FILE RUJUKAN :

UNTUK KEGUNAAN MDKP

TAJUK PROJEK:

CADANGAN MEMBINA 1 UNIT SURAU 1 TINGKAT
DIATAS LOT 20093,
TAMAN JUASSEH SENTOSA,
PEKAN JUASSEH, DAERAH KUALA PILAH
NEGERI SEMBILAN DARUL KHUSUS
UNTUK
TETUAN JABATAN HAL EHWAL AGAMA ISLAM
NEGERI SEMBILAN

TANDATANGAN PEMILIK TANAH / BANGUNAN :

"Saya/Kami bersetuju untuk mematuhi pelan bangunan yang diluluskan. Dengan ini saya/kami bersetuju untuk dikenakan tindakan undang-undang yang berkaitan dengannya jika gagal mematuhiinya".

JABATAN HAL EHWAL AGAMA ISLAM

KUALA PILAH NEGERI SEMBILAN

PEGAWAI AGAMA DAERAH :

NO. K/P :

NO TEL :

EMAIL :

ALAMAT :

HARDI BIN MOHAMAD SADALI

750098-10-5965

06-46211029

padkualapilah.jheains@ns.gov.my

JHEAINS Kuala Pilah, 70200 Kuala Pilah


Negeri Sembilan

ARKITEK:

"SAYA MEMPERAKUI BAHAWA BUTIRAN - BUTIRAN DI DALAM PELAN - PELAN INI ADALAH MENURUT KEHENDAK - KEHENDAK UNDANG - UNDANG KECIL BANGUNAN SERAGAM (PBTNS) 1986 DAN SAYA SETUJU TERIMA TANGGUNGJAWAB PENUH DENGAN SEWAJARNYA"



Ar. Wan Azami Bin Hamzah
ARKITEK PROFESIONAL
No Pendaftaran LAM: A/W 56

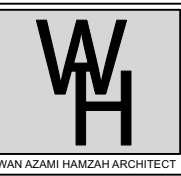

NO. 2 JALAN MERAH PELANGI SATU
U9/19a KELAB GOLF MONTEREZ
40150 SHAH ALAM, SELANGOR MALAYSIA
NO. TEL : 019 2063 100 / 012 324 0914
EMAIL : wah.architect@gmail.com

STATUS LUKISAN :

☐ PRELIMINARY ☒ SUBMISSION ☐ CONSTRUCTION
☐ INFORMATION ☐ TENDER ☐ DEVELOPMENT ORDER

TAJUK LUKISAN:

SANITARY PLUMBING SCHEMATIC
AMD WATER METER

DILUKIS OLEH	JW
DISEMAK OLEH	WA
TARIKH	DEC 2025
SKALA	1:100
NO DWG.	SJS/BP/004