GULLY TRAP DETAIL

SCALE 1 : 25

FLOOR TRAP DETAIL

SCALE 1 : 25

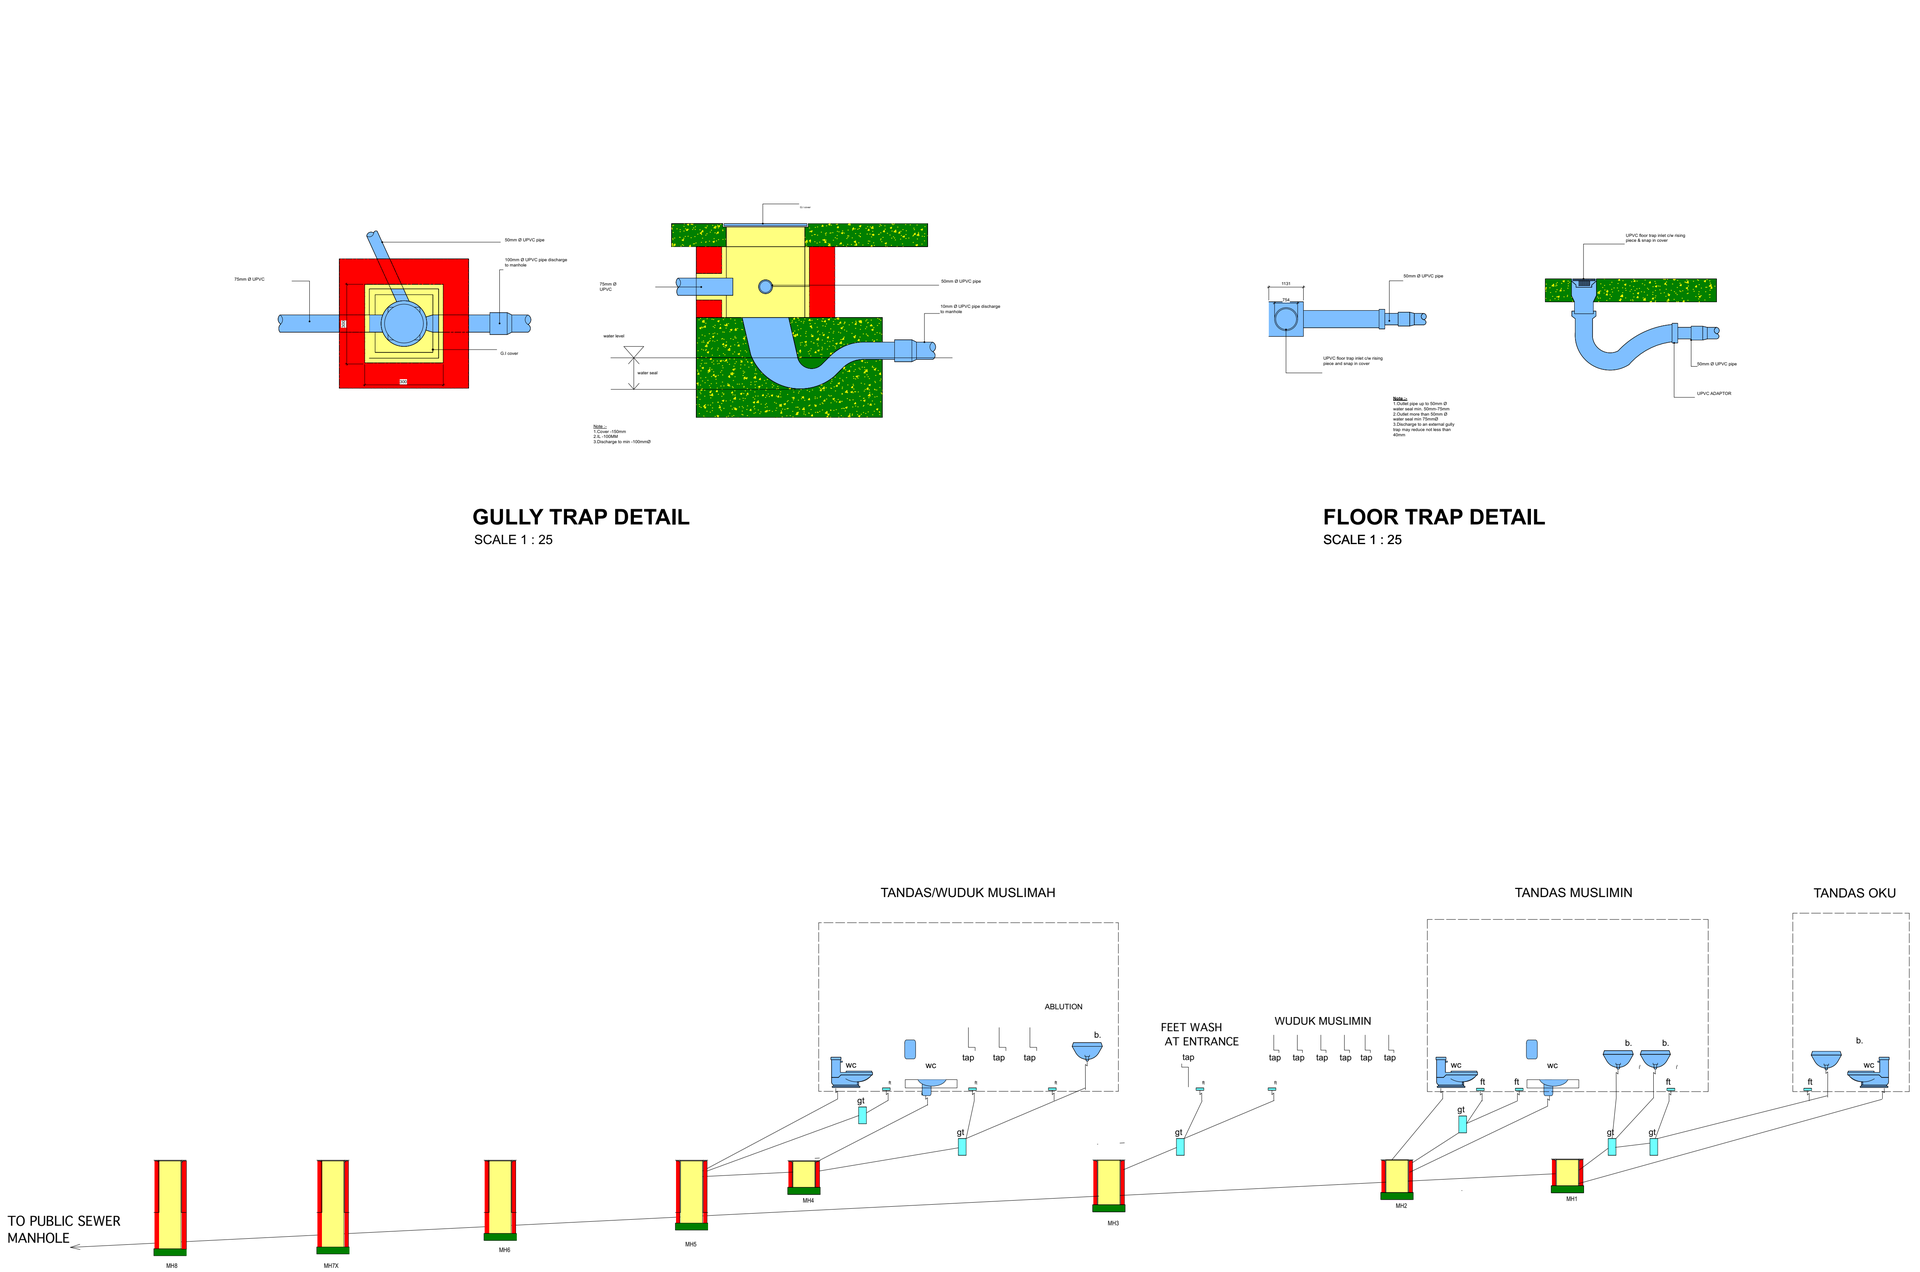

SANITARY DIAGRAMATIC

NTS

NO FILE RUJUKAN :

UNTUK KEGUNAAN MDKP

TAJUK PROJEK:

CADANGAN MEMBINA 1 UNIT SURAU 1 TINGKAT DIATAS LOT 20093, TAMAN JUASSEH SENTOSA, PEKAN JUASSEH, DAERAH KUALA PILAH NEGERI SEMBILAN DARUL KHUSUS UNTUK TETUAN JABATAN HAL EHWAL AGAMA ISLAM NEGERI SEMBILAN

TANDATANGAN PEMILIK TANAH / BANGUNAN :

"Saya/Kami bersetuju untuk mematuhi pelan bangunan yang diluluskan. Dengan ini saya/kami bersetuju untuk dikenakan tindakan undang-undang yang berkaitan dengannya jika gagal mematuhinya".

JABATAN HAL EHWAL AGAMA ISLAM
KUALA PILAH NEGERI SEMBILAN

PEGAWAI AGAMA DAERAH	:	HARDI BIN MOHAMAD SADALI
NO. K/P	:	750908-10-5965
NO TEL	:	06-4821029
EMAIL	:	paidkualapilah.jheains@ns.gov.my
ALAMAT	:	JHEAINS Kuala Pilah, 70200 Kuala Pilah Negeri Sembilan

ARKITEK:

"SAYA MEMPERAKUI BAHAWA BUTIRAN - BUTIRAN DI DALAM PELAN - PELAN INI ADALAH MENURUT KEHENDAK - KEHENDAK UNDANG - UNDANG KECIL BANGUNAN SERAGAM (PBT:NS) 1986 DAN SAYA SETUJU TERIMA TANGGUNGJAWAB PENUH DENGAN SEWAJARNYA"

LEMBAGA ARKITEK MALAYSIA

Ar. Wan Azami Bin Hamzah
ARKITEK PROFESIONAL
No Pendaftaran LAM : A/W 56

WAN AZAMI HAMZAH ARCHITECT
NO. 2 JALAN MERAH PELANGI SATU
U9/19a KELAB GOLF MONTEREZ
40150 SHAH ALAM, SELANCOR **MALAYSIA**
NO. TEL : 019 2063 100 / 012 324 0914
EMAIL : wah.architect@gmail.com

STATUS LUKISAN :

☐ PRELIMINARY ■ SUBMISSION ☐ CONSTRUCTION
☐ INFORMATION ☐ TENDER ☐ DEVELOPMENT ORDER

TAJUK LUKISAN:

SEWERAGE SCHEMATIC

DILUKIS OLEH	JW
DISEMAK OLEH	WA
TARIKH	DEC 2025
SKALA	AS SHOWN
NO DWG.	SJS/BP/005