
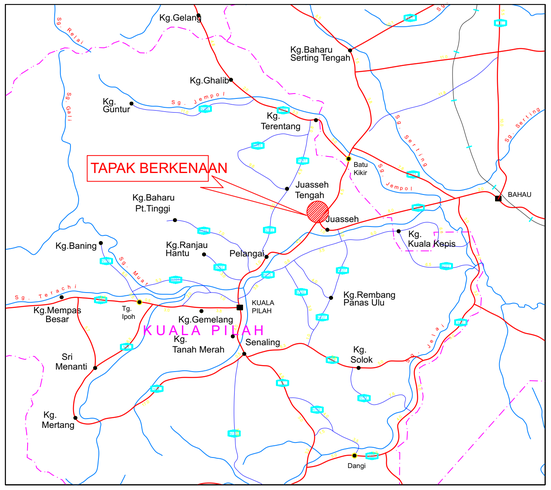


U

PELAN KUNCI


SKALA : TANPA SKALA

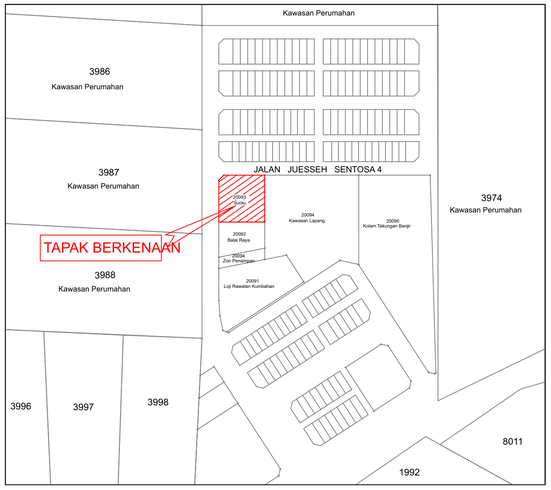


U

PELAN LOKASI

SKALA : 8 RANTAI SEINCI

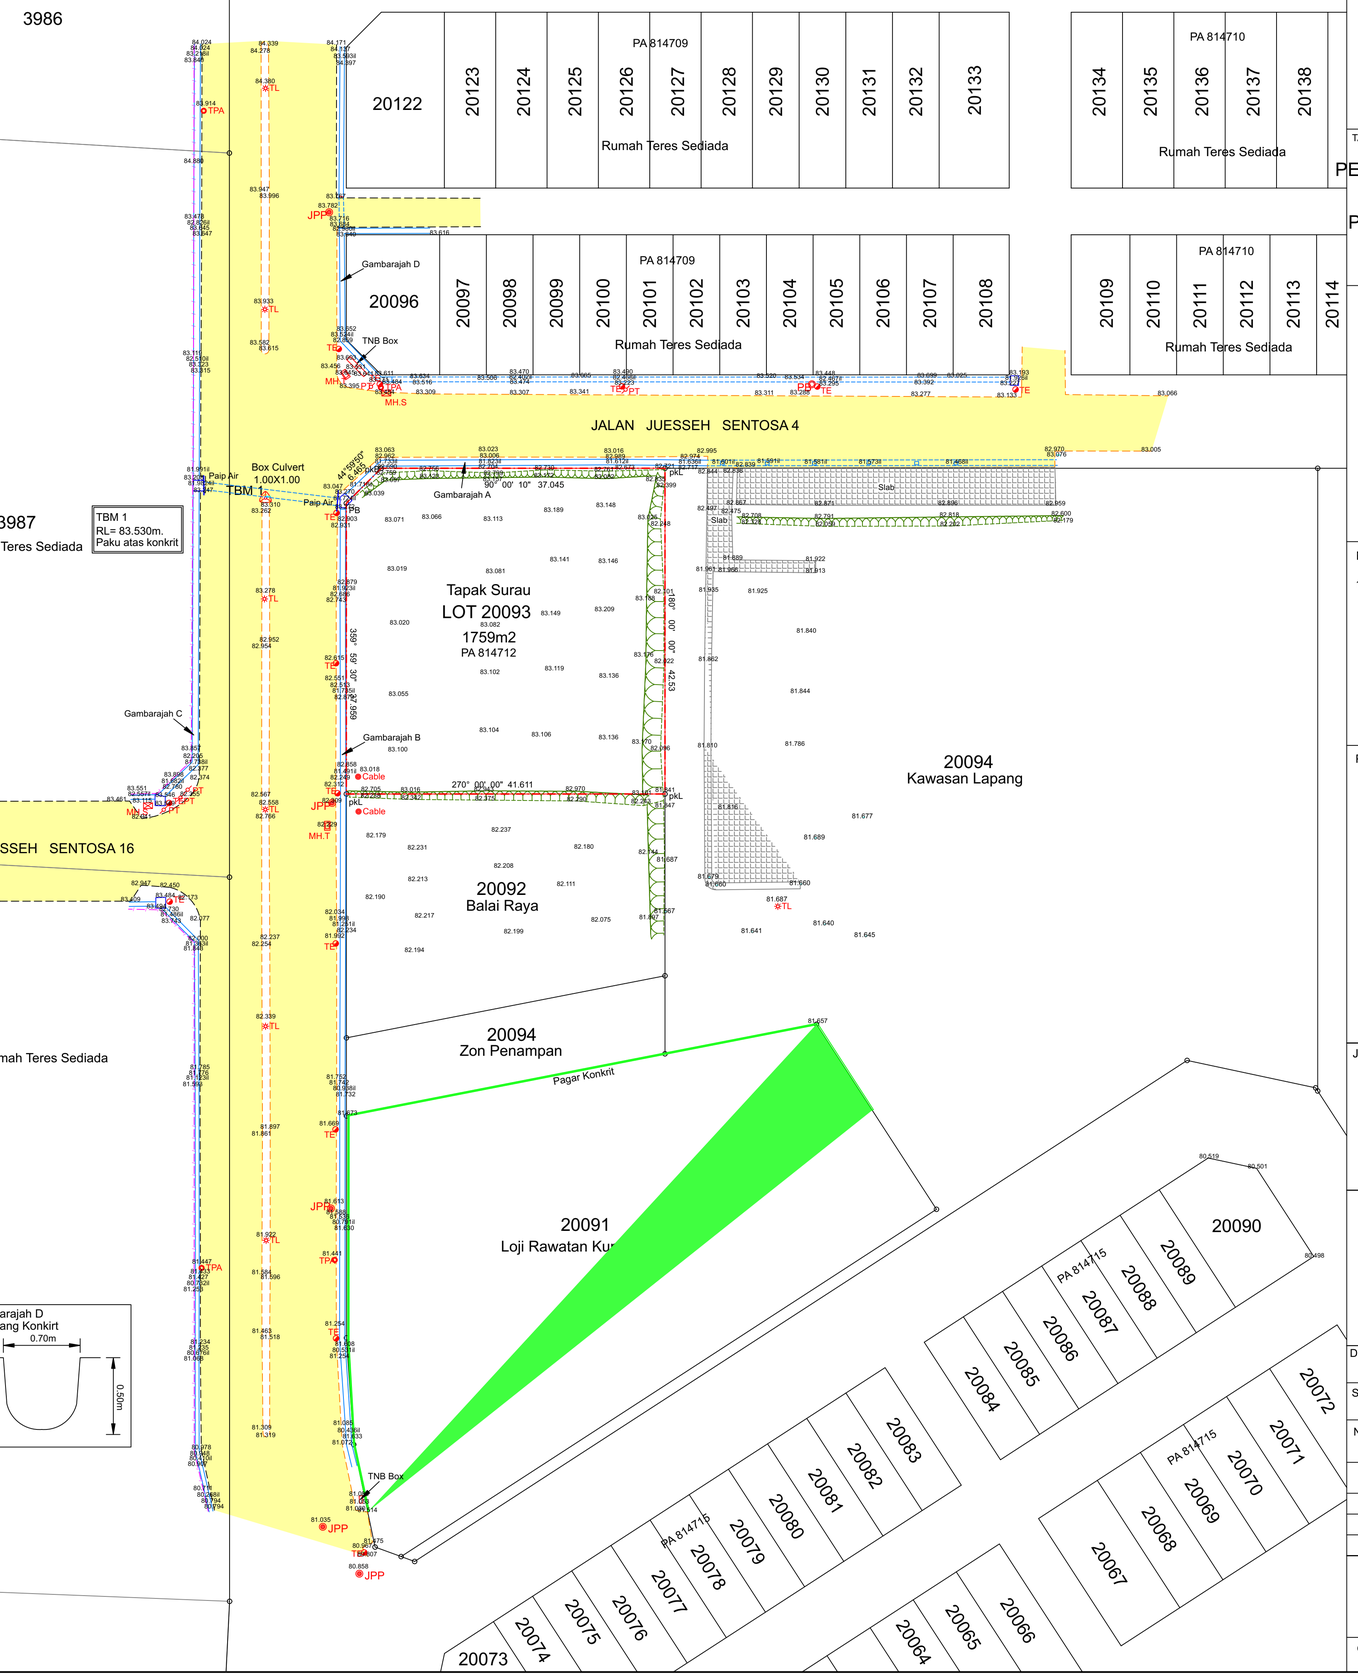

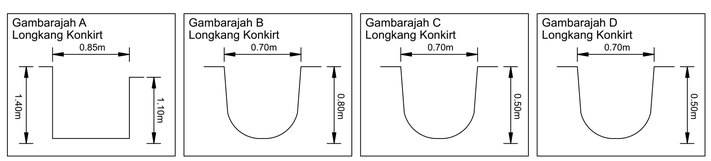

U

Kiblat

SKALA 1 : 400 (A1)

SYIT PIAWAI : 49-A-II

TAJUK :-

PELAN UKURAN BUTIRAN DAN ARAS LARAS DI ATAS TANAH LOT 20093, PEKAN JUASSEH, DAERAH KUALA PILAH, NEGERI SEMBILAN.

PEMILIK :

NOTA :-

1. SEMUA UKURAN ADALAH DALAM UNIT METER.

PA 814712.

(RL= 80.067M) YANG TERLETAK DI KIRI JALAN KUALA PILAH - BATU KIKIR TERLETAK 80M SELEPAS SIMPANG 3 KE JUESSEH DAN

DAN SAINS KESIHATAN UPM.

PETUNJUK : -

- Jalan Tar
- Divider Jalan
- Slab
- Longkang Konkrit
- Pagar Konkrit
- Pagar Dawai
- Cutting
- Paku Lama (pkL)
- Paku Baru (pkB)
- Paip Baru (PB)
- TE Tiang Elektrik
- TL Tiang Lampu
- PT Papan Tanda
- PB Pili Bomba
- Cable Paip Cable
- TPA Tanda Paip Air
- MH.T Menhole TM
- MH.S Menhole Air
- JPP Menhole Kumbahan
- Sump

JURUKUR BERLESEN :

JURUKUR TEGUH SDN.BHD.
(LJT 155/386711-P)
131-2 & 133-2 JALAN SBC 1,
TAMAN SRI BATU CAVES,
68100 BATU CAVES,
SELANGOR DARUL EHSAN.
TEL. NO. 03-61876687 , FAX : 03-61876687
EMAIL : jurukurteguh@yahoo.com

TANDATANGAN JURUKUR BERLESEN :

HJ. MOHD APANDI HJ. MOHAMAD
No.K/P : 600523-03-5499.
MBA,B.SUR (HONS), LAND, MAALS,MIS(M), MREAAA
Surveyors Licensed
Under Act 458 (Revised 1991)

DIUKUR OLEH :	DILUKIS OLEH :	DI SEMAK OLEH :
SAIDI	EDDY	ABD.HADI

SKALA :	TARIKH :
1 : 400 (A1)	07 2023

NO LUKISAN : JTSEL/2023(07)/ENG/699

NO	TARIKH	CATATAN	DILULUSKAN OLEH

NO. RUJUKAN :

PINDAAN:

CATITAN :